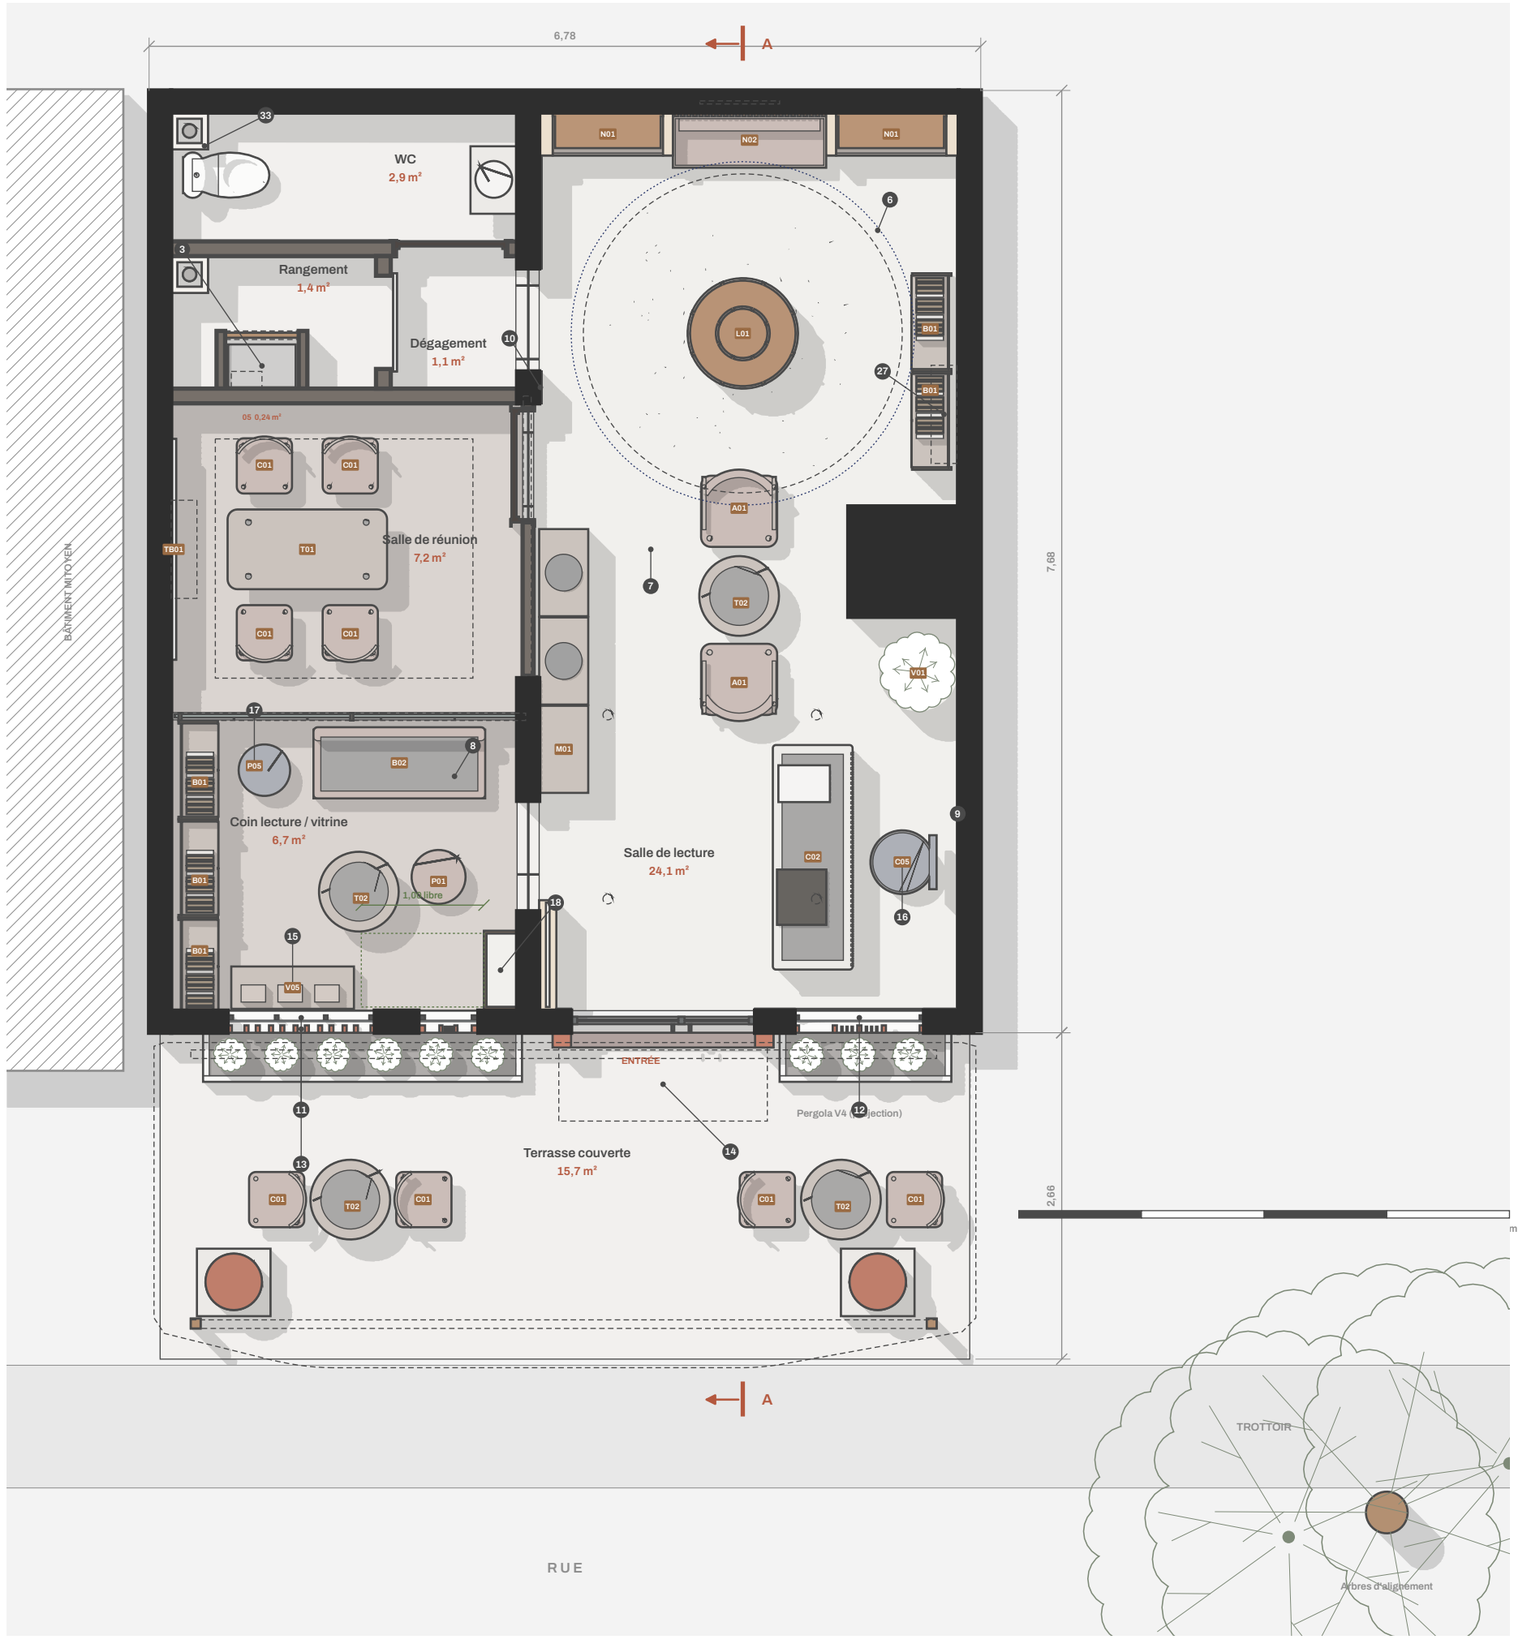


K&Démi

Bibliothèque Decimo

Plan du rez-de-chaussée — aménagement

Esquisse V5 sur existant V4 · Échelle 1/50 (A3) · Plan de coupe à +1,00

ESPACES (IFCSPACE)

01	Salle de lecture	24,07 m²	HSP 3,00
02	Coin lecture / vitrine	6,68 m²	HSP 3,00
03	Salle de réunion	7,21 m²	HSP 3,00
04	Rangement	1,37 m²	HSP 3,00
05	Placard technique	0,24 m²	HSP 3,00
06	Dégagement	1,11 m²	HSP 3,00
07	WC	2,87 m²	HSP 3,00
08	Terrasse couverte (pergola V4)	15,74 m²	HSP 2,90
	Total intérieur (hors terrasse)	43,55 m²	

REPÈRES DE L'AMÉNAGEMENT V5

- 3 Placard technique 0,60 x 0,40 net
- 6 Oculus Ø 2,80 : bandeau iroko, sous-face de …
- 7 Sol terrazzo sable
- 8 Sol parquet iroko
- 9 Enduit terre (argile locale) 15 mm
- 10 Lambris iroko à claire-voie
- 11 Vitrine en arche, châssis acier noir
- 12 Châssis fixes acier noir (baies B, C)
- 13 Claustras terre cuite : inserts Adinkrahene …
- 14 Marquise acier noir (débord 0,60)
- 15 Podium de vitrine iroko (h 0,45 = allège bai…
- 16 Siège agent d'accueil (tissu indigo)
- 17 Pouf de lecture indigo
- 18 Tableau divisionnaire encastré dans habillag…
- 27 Split mural 9 000 BTU/h (2,6 kW)
- 33 Coffrage acoustique 0,30 x 0,30 descente EU/…

MOBILIER (REPÈRES V4 CONSERVÉS)

- A01 Fauteuil × 2
- B01 Rayonnage 800 × 5
- B02 Banquette × 1
- C01 Chaise Courbe × 8
- C02 Comptoir × 1
- C05 Siege Accueil × 1
- L01 Arbre A Livres × 1
- M01 Console Vinyles P40 × 1
- N01 Niche Bibliotheque × 2
- N02 Niche Banquette × 1
- P01 Pouf × 1
- P05 Pouf Indigo × 1
- T01 Reunion 1300 × 1
- T02 Table Ronde × 4
- TB01 Tableau Mural × 1
- V01 Plante × 1
- V05 Podium Vitrine × 1

LÉGENDE

- Existant porteur coupé (V4 inchangé, ne pas toucher)
- Cloison légère coupée (V4 et V5)
- Mobilier, menuiseries, revêtements coupés
- Au-dessus du plan de coupe (marquise, pergola, canopée, split)
- Oculus Ø 2,80 sous dalle (indigo)
- Dégagement 1,00 m devant le tableau divisionnaire

PROJET	Bibliothèque Decimo — RDC sous logements, Abidjan
PHASE	ESQ V5 — aménagement sur existant V4
PLANCHE	A01 — Plan du rez-de-chaussée — aménagement
ÉCHELLE	1/50 · format A3
MAQUETTE	v5/DECIMO_ESQ_V5.ifc (IFC4) · sha256 985f48d48b…
DATE	Octobre 2026 · indice A

Esquisse : cotes et surfaces indicatives, existant V4 à relever sur site.