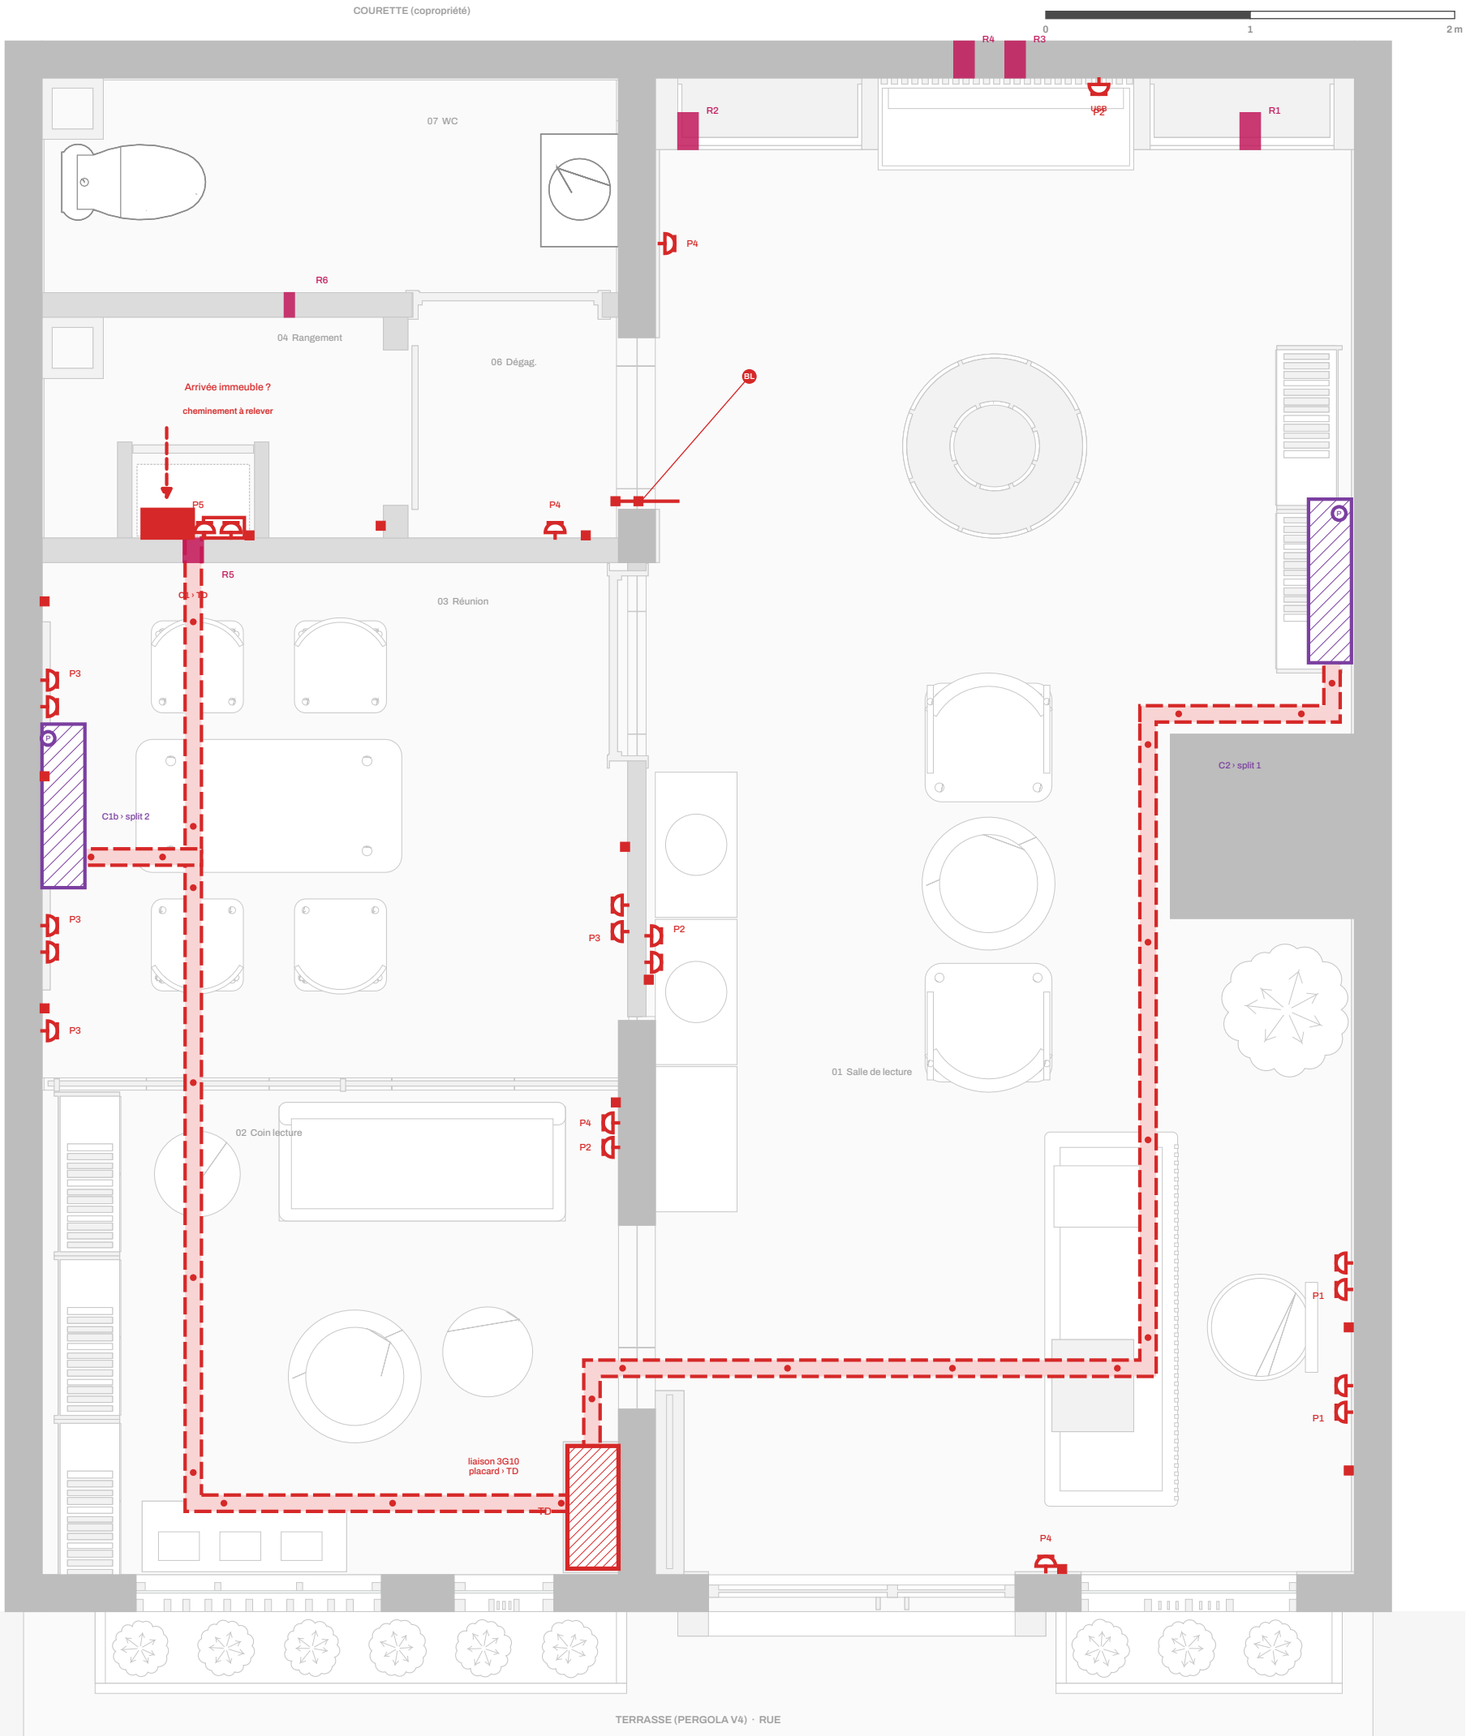


K&Démi

Bibliothèque Decimo

Électricité — courants forts

Plan de coupe +1,00, réseaux en plénum superposés · Échelle 1/30 (A3) · NF C 15-100

LÉGENDE TECHNIQUE		QTÉ
COURANTS FORTS		
	Prise 16 A 2P+T + n° de circuit	6
USB	Prise 16 A 2P+T double	7
	Prise 16 A + USB (mobilier)	1
	Tableau divisionnaire TD (V5)	1
	Coffret arrivée immeuble (placard)	1
	Boîte de dérivation / coffret clim	1
	Chemin de câbles CFO 80 × 40, plénum	3
	Descente en goulotte 40 × 20	14
	Suspente M8, cheville courte	25
CLIMATISATION		
	Split 9 000 BTU/h (circuits C1, C2)	2
	Mini-pompe de relevage condensats	2
RÉSERVATIONS		
	Fourreau / réservation (R5, R6)	6

CIRCUITS PRISES ET SPÉCIALISÉS (REPÈRES DU SCHÉMA T05)

P1	PC accueil (poste agent, imprimante, caisse)	4 socles · 20 A · 2,5 mm²
P2	PC postes de lecture et d'écoute	4 socles · 20 A · 2,5 mm²
P3	PC salle de réunion (écran, portables)	7 socles · 20 A · 2,5 mm²
P4	PC ménage (entrée, coin lecture, fond, dégagement)	4 socles · 20 A · 2,5 mm²
P5	PC baie informatique (onduleur, box, switch PoE)	2 socles · 16 A · 2,5 mm²
C1	Split 1 salle de lecture + mini-pompe 1	1 split + pompe · 16 A · 2,5 mm²
C2	Split 2 salle de réunion + mini-pompe 2	1 split + pompe · 16 A · 2,5 mm²

PRINCIPES

Tableau divisionnaire V5 (rep. TD) alimenté par le coffret d'arrivée du placard technique (disjoncteur de branchement de l'immeuble), liaison 3G10 dans C1. Cheminement de l'arrivée immeuble › placard inconnu : à relever (point ouvert). Câbles U1000 R2V en plénum sur chemins 80 × 40 (C1, C1b, C2), suspentes M8 à cheville courte non traversante ; descentes en goulotte 40 × 20 collée ou derrière le lambris / doublage : aucune saignée dans les porteurs. Appareillage en saillie, axe +0,30 (prises) et +1,10 (commandes). BL : traversée de la baie libre V4 sous le linteau (goulotte collée, h 2,08). R6 : fourreau Ø 50 en plénum dans la cloison placo V4 4350620 (non porteuse), à valider comme R5 ; sinon goulotte franchissant l'huisserie du WC.

PROJET	Bibliothèque Decimo — RDC sous logements, Abidjan
PHASE	ESQ V5 — lots techniques sur existant V4
PLANCHE	T01 — Électricité — courants forts
ÉCHELLE	1/30 · format A3
MAQUETTE	v5/DECIMO_ESQ_V5_tech.ifc (IFC4) · sha256 2a97083fa5…
DATE	Octobre 2026 · indice A

Esquisse : cotes et surfaces indicatives, existant V4 à relever sur site.