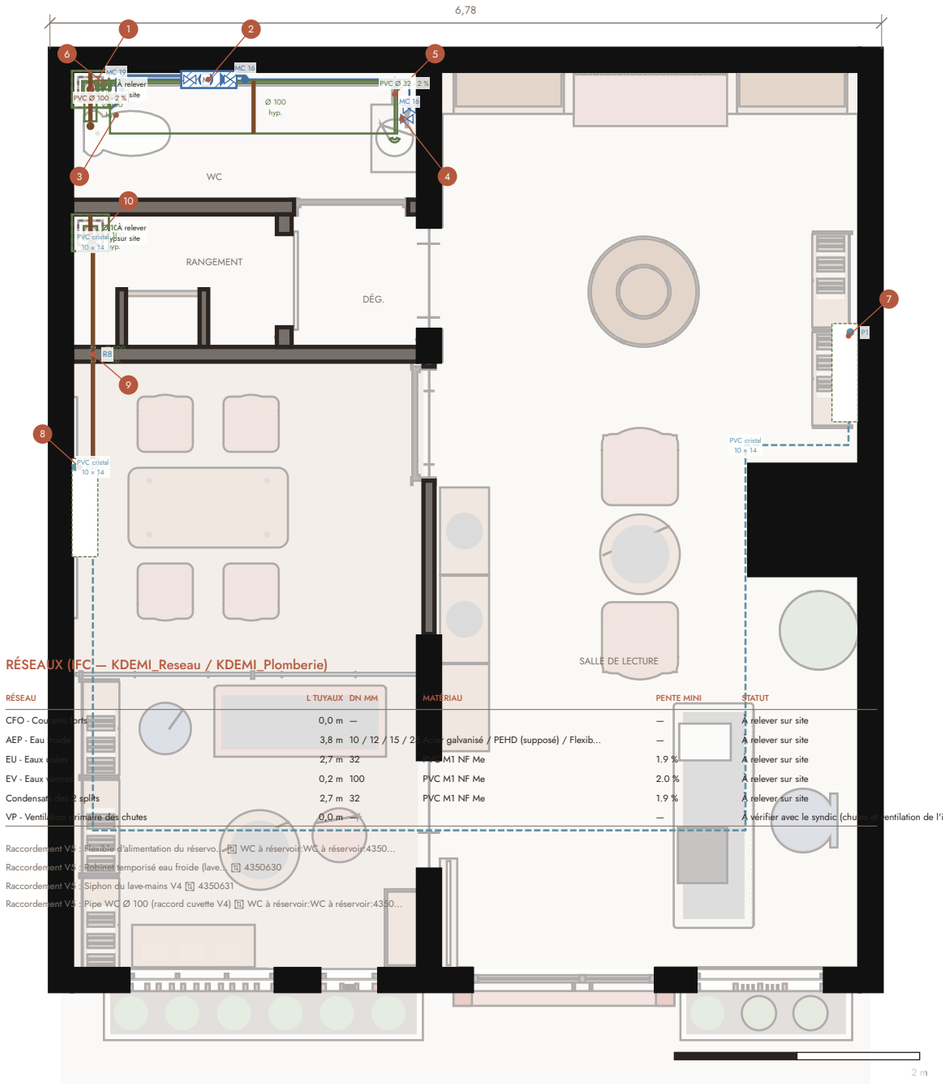



RÉSEAUX (IFC — KDEMI_Reseau / KDEMI_Plomberie)

RÉSEAU	L TUYAUX	DN MM	MATÉRIAU	PENTE MINI	STATUT
CFO - Cou[illegible]orts	0,0 m	—	—	—	À relever sur site
AEP - Eau [illegible]	3,8 m	10 / 12 / 15 / 2[illegible]	[illegible] galvanisé / PEHD (supposé) / Flexib…	—	À relever sur site
EU - Eaux [illegible]	2,7 m	32	PVC M1 NF Me	1.9 %	À relever sur site
EV - Eaux [illegible]	0,2 m	100	PVC M1 NF Me	2.0 %	À relever sur site
Condensats des 2 splits	2,7 m	32	PVC M1 NF Me	1.9 %	À relever sur site
VP - Ventil[illegible] primaire des chutes	0,0 m	—	—	—	À vérifier avec le syndic (chute et ventilation de l'imme[illegible]

Raccordement V5 : Robinet d'alimentation du réservo… [11] WC à réservoir:WC à réservoir:4350…
Raccordement V5 : Robinet temporisé eau froide (lave… [11] 4350630
Raccordement V5 : Siphon du lave-mains V4 [11] 4350631
Raccordement V5 : Pipe WC Ø 100 (raccord cuvette V4) [11] WC à réservoir:WC à réservoir:4350…

ZOOM WC / RANGEMENT — 1/25

ÉLÉVATION MUR NORD WC — 1/25 (V4 conservé)

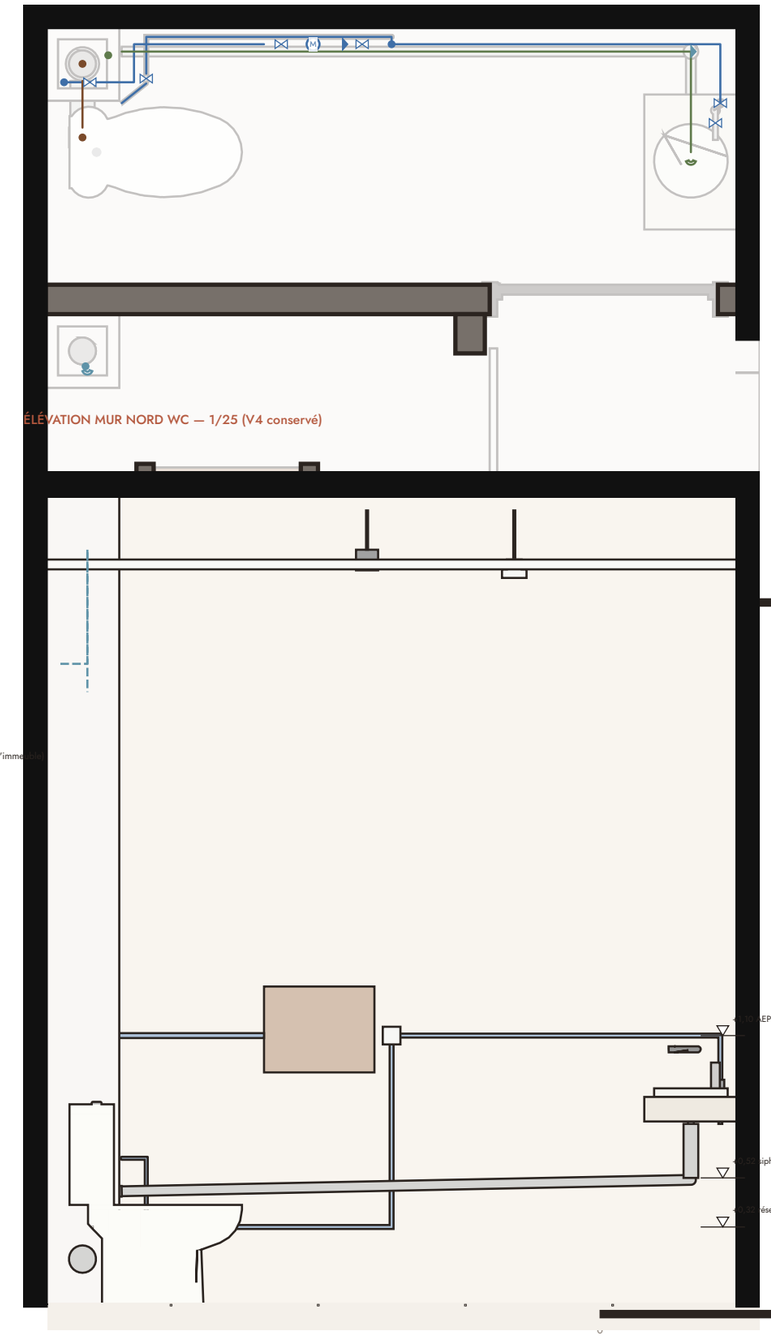

K&Démi

Bibliothèque Decimo

Plomberie — AEP, EU, EV et condensats

Plan sanitaire · Échelle 1/50 et 1/25 (A3) · Coupe à +1,00

SYMBOLES

- Eau froide AEP (multicouche)
- Eaux usées EU (PVC)
- Eaux vannes EV (PVC)
- Condensats (refoulement mini-pompes)
- Ventilation primaire / clapet aérateur
- Tronçon en plénum (z > 2,00) : tirets
- Vanne / robinet d'arrêt
- Compteur divisionnaire
- Clapet (EA, aérateur)
- Té / culotte / piquage
- Siphon / siphon sec

POINTS SINGULIERS

1. Colonne / piquage AEP immeuble (position, DN, pression à relever)
2. Coffret de comptage (vanne, compteur, clapet EA, réducteur si P > 3 bar)
3. WC V4 conservé (4350629), alimentation flexible — non dupliqué
4. Lave-mains V4 conservé (plan 4350630, vasque 4350631), robinet temporisé
5. Siphon lave-mains + clapet aérateur Ø 40 sur antenne EU
6. Culotte / piquage Ø 40 sur descente EU/EV 1 (à relever)
7. Mini-pompe condensats split 1 (refoulement vers collecteur)
8. Mini-pompe condensats split 2
9. R8 Ø 0,04 : passage condensats (cloison placo non porteuse)
10. Siphon sec condensats + piquage sur descente EU/EV 2

PRINCIPES

Pas de chauffe-eau : un seul lave-mains, eau froide réseau (26-30 °C à Abidjan), pas de circuit 20 A dédié ni de stockage d'eau chaude (légionelles).
WC et lave-mains V4 conservés, non dupliqués : raccordements V5 via IfcRelConnectsElements « Raccordement V5 sur appareil V4 conservé ».
Branchements immeuble / descentes EU·EV : position et diamètres à relever.
Réducteur de pression posé seulement si P mesurée > 3 bar.
Condensats refoulés par mini-pompes vers la descente EU/EV 2 (siphon sec).

PROJET	Bibliothèque Decimo — RDC sous logements, Abidjan
PHASE	ESQ V5 — aménagement sur existant V4
PLANCHE	A10 — Plomberie — AEP, EU, EV et condensats
ÉCHELLE	1/50 et 1/25 · format A3
MAQUETTE	v5/DECIMO_ESQ_V5.ifc (IFC4) · sha256 88ef6d0a1f…
DATE	Octobre 2026 · indice A

Esquisse : cotes et surfaces indicatives, existant V4 à relever sur site.