K&Démi

# Bibliothèque Decimo

## Esquisse V5 · aménagement intérieur et devanture

Local en rez-de-chaussée sous logements
Deux Plateaux, Abidjan

**DOSSIER DE PRÉSENTATION**

D.A · plans · coupe · élévations · vues 3D · axonométries · électricité · plomberie · détails techniques

15 octobre 2026 · indice A

En couverture : l'arbre à livres sous l'oculus indigo, rendu tiré de la vue 04 de la maquette IFC V5



La devanture sous la pergola conservée de la V4, rendu tiré de la vue 01 de la maquette

## Le lieu

Un local commercial de 6,78 × 7,68 m au rez-de-chaussée d'un immeuble de logements, à Deux Plateaux. Poteaux, voiles et dalle haute appartiennent à l'immeuble et restent intacts : le projet est un aménagement, pas une construction.

## Le programme

Une bibliothèque de quartier : une salle de lecture autour de l'arbre à livres, un coin lecture en vitrine, une salle de réunion, un seul WC, un rangement et un placard technique. La terrasse couverte prolonge la lecture sur la rue.

## Le parti

Terre, ombre et bois. La claustra en terre cuite filtre le soleil, l'iroko habille tout ce qui se touche et la chaux tout ce qui se voit. L'arbre à livres et son oculus indigo sont le seul objet fort de la salle.

**43,55 m²**
surface intérieure, 7 espaces

**15,74 m²**
terrasse couverte sous pergola

**3,00 m**
hauteur sous faux-plafond

**141 / 141**
éléments existants V4 conservés à l'identique

K&Démi

# Le projet

## Une salle de lecture fraîche en pied d'immeuble

Esquisse V5 · existant V4 inchangé

SOMMAIRE


| | |
|---|---|
| Couverture | 01 |
| Le projet | 02 |
| Identité K&Démi | 03 |
| D.A de la bibliothèque | 04 |
| A01 Plan du RDC, aménagement | 05 |
| A02 Faux-plafond et réseaux | 06 |
| A03 Coupe AA | 07 |
| A04 Élévation de la devanture | 08 |
| A05 Élévations intérieures Est, Nord | 09 |
| A06 Élévations intérieures Sud, Ouest | 10 |
| A07 Vues 3D de la maquette | 11 |
| A08 Axonométries | 12 |
| R1 Rendu de la devanture | 13 |
| R2 Rendus intérieurs | 14 |
| R3 L'arbre à livres | 15 |
| T01 Courants forts | 16 |
| T02 Courants faibles et éclairage | 17 |
| T03 Plomberie AEP, EU, EV | 18 |
| T04 Détails techniques | 19 |
| T05 Unifilaire et bilan de puissance | 20 |
| Cohérence et points ouverts | 21 |


ESPACES (IFCSPACE DE LA MAQUETTE)

| | |
|---|---|
| 01 Salle de lecture | 24,07 m² |
| 02 Coin lecture, vitrine | 6,68 m² |
| 03 Salle de réunion | 7,21 m² |
| 04 Rangement | 1,37 m² |
| 05 Placard technique | 0,24 m² |
| 06 Dégagement | 1,11 m² |
| 07 WC | 2,87 m² |
| Total intérieur | 43,55 m² |
| 08 Terrasse couverte | 15,74 m² |

| | |
|---|---|
| PROJET | Bibliothèque Decimo · RDC sous logements, Deux Plateaux, Abidjan |
| PHASE | ESQ V5 · aménagement sur existant V4 |
| PLANCHE | 02 · Le projet |
| ÉCHELLE | sans échelle · format A3 paysage |
| MAQUETTE | v5/DECIMO_ESQ_V5.ifc (IFC4) |
| DATE | 15 octobre 2026 · indice A |




Version principale : encre sur blanc chaux, « & » en terre cuite. Zone de protection : la moitié de la hauteur du carré tout autour.

**Encre**
#2B2420 · texte, traits

**Terre cuite**
#B4583E · signature

**Iroko**
#9A6B43 · bois, repères

**Sable**
#E6D6BF · aplats

**Sable clair**
#F4EDE2 · fonds

**Blanc chaux**
#FBF8F3 · page

**Taupe**
#7D7168 · texte 2

**Olive**
#5F7A4B · végétal, rare

## DM Serif Display

Titres, chiffres clés, 18 à 36 pt

## Jost

Texte 8 à 10 pt, légendes 7 pt, capitales espacées

## Manrope

Réservée au nom K&Démi dans le logo







K&Démi

# Identité K&Démi

## L'arche dans le carré

Logo v3 A choisi le 14 octobre 2026

### LE LOGO

Une arche découpée dans un carré, lue comme une porte. Le nom est composé en Manrope, l'esperluette en terre cuite. C'est le seuil de la devanture Decimo ramené à un signe.

### RÈGLES D'USAGE

01 Le nom est toujours posé à côté du symbole. Le symbole seul est réservé à l'icône d'application et au favicon.

02 30 mm minimum en impression, 120 px à l'écran.

03 Version mono sur fond clair, inversée sur fond sombre. Pas de déformation, d'ombre ni de dégradé.

### LA PAGE

Toutes les pages du dossier partagent la même grille et le même panneau de droite que les planches de dessin : 12 colonnes, marges de 14 mm, gouttières de 5 mm.

| | |
|---|---|
| PROJET | Bibliothèque Decimo · RDC sous logements, Deux Plateaux, Abidjan |
| PHASE | ESQ V5 · aménagement sur existant V4 |
| PLANCHE | 03 · Identité K&Démi |
| ÉCHELLE | sans échelle · format A3 paysage |
| MAQUETTE | v5/DECIMO_ESQ_V5.ifc (IFC4) |
| DATE | 15 octobre 2026 · indice A |



Planche matière : claustra en terre cuite, iroko huilé, chaux sable, enduit terre, grès cérame, acier noir, laine terre cuite, coton indigo, raphia

Terre cuite #B4583E

Iroko #9A6B43

Sable #E6D6BF

Chaux #FBF8F3

Encre #2B2420

Indigo #2F3A56

Olive #5F7A4B

## Matériaux

Terrazzo clair au sol, parquet iroko dans la salle de lecture, enduit terre et chaux sable aux murs, lambris iroko à claire-voie, acier noir mat pour les châssis et la marquise.

## Mobilier

Iroko sur mesure : arbre à livres, rayonnages, banque d'accueil, banquettes. Chaises courbes, assises en raphia, coussins indigo artisanaux.

## Lumière

Tout en 2700 K. Anneau LED sous la canopée de l'arbre, downlights encastrés, suspensions terre cuite au-dessus des tables, réglette de vitrine, spot IP65 sous marquise.

## Végétal

Ficus lyrata, strelitzia, fougères et dracaena en jardinières sur la terrasse. Le vert reste rare à l'intérieur pour laisser la terre et le bois parler.

K&Démi

# D.A de la bibliothèque

Terre, ombre et bois

Direction artistique d'Affoué, visée le 14 octobre 2026

### PRINCIPES

01 Un seuil cintré centré sur la rue cadre l'arbre à livres.

02 Les baies en claustra terre cuite, à motifs inspirés des Adinkra Adinkrahene et Eban, filtrent le soleil de l'après-midi.

03 La canopée de l'arbre et son oculus indigo sont le seul objet fort de la salle.

04 Iroko pour tout ce qui se touche, chaux pour tout ce qui se voit.

05 Ventilation traversante par la claustra et la terrasse, deux splits en appoint dont les unités extérieures vont en courette.

### AMBIANCE

Une pénombre fraîche, une lumière tamisée par la claustra le jour et 2700 K le soir. Aucun dégradé, aucun motif plaqué : les motifs naissent de la matière.

| | |
|---|---|
| PROJET | Bibliothèque Decimo · RDC sous logements, Deux Plateaux, Abidjan |
| PHASE | ESQ V5 · aménagement sur existant V4 |
| PLANCHE | 04 · D.A de la bibliothèque |
| ÉCHELLE | sans échelle · format A3 paysage |
| MAQUETTE | v5/DECIMO_ESQ_V5.ifc (IFC4) |
| DATE | 15 octobre 2026 · indice A |




K&Démi

# Bibliothèque Decimo

## Plan du rez-de-chaussée — aménagement

Esquisse V5 sur existant V4 · Échelle 1/50 (A3) · Plan de coupe à +1,00

### ESPACES (IFCSPACE)

| | | | |
|---|---|---|---|
| 01 | Salle de lecture | 24,07 m² | HSP 3,00 |
| 02 | Coin lecture / vitrine | 6,68 m² | HSP 3,00 |
| 03 | Salle de réunion | 7,21 m² | HSP 3,00 |
| 04 | Rangement | 1,37 m² | HSP 3,00 |
| 05 | Placard technique | 0,24 m² | HSP 3,00 |
| 06 | Dégagement | 1,11 m² | HSP 3,00 |
| 07 | WC | 2,87 m² | HSP 3,00 |
| 08 | Terrasse couverte (pergola V4) | 15,74 m² | HSP 2,90 |
| | **Total intérieur (hors terrasse)** | **43,55 m²** | |

### REPÈRES DE L'AMÉNAGEMENT V5

- 3 Placard technique 0,60 x 0,40 net
- 6 Oculus Ø 2,80 : bandeau iroko, sous-face de …
- 7 Sol terrazzo sable
- 8 Sol parquet iroko
- 9 Enduit terre (argile locale) 15 mm
- 10 Lambris iroko à claire-voie
- 11 Vitrine en arche, châssis acier noir
- 12 Châssis fixes acier noir (baies B, C)
- 13 Claustras terre cuite : inserts Adinkrahene …
- 14 Marquise acier noir (débord 0,60)
- 15 Podium de vitrine iroko (h 0,45 = allège bai…
- 16 Siège agent d'accueil (tissu indigo)
- 17 Pouf de lecture indigo
- 18 Tableau divisionnaire encastré dans habillag…
- 27 Split mural 9 000 BTU/h (2,6 kW)
- 33 Coffrage acoustique 0,30 x 0,30 descente EU/…

### MOBILIER (REPÈRES V4 CONSERVÉS)


- A01 Fauteuil × 2
- B01 Rayonnage 800 × 5
- B02 Banquette × 1
- C01 Chaise Courbe × 8
- C02 Comptoir × 1
- C05 Siege Accueil × 1
- L01 Arbre A Livres × 1
- M01 Console Vinyles P40 × 1
- N01 Niche Bibliotheque × 2
- N02 Niche Banquette × 1
- P01 Pouf × 1
- P05 Pouf Indigo × 1
- T01 Reunion 1300 × 1
- T02 Table Ronde × 4
- TB01 Tableau Mural × 1
- V01 Plante × 1
- V05 Podium Vitrine × 1

### LÉGENDE

- Existant porteur coupé (V4 inchangé, ne pas toucher)
- Cloison légère coupée (V4 et V5)
- Mobilier, menuiseries, revêtements coupés
- Au-dessus du plan de coupe (marquise, pergola, canopée, split)
- Oculus Ø 2,80 sous dalle (indigo)
- Dégagement 1,00 m devant le tableau divisionnaire

| | |
|---|---|
| PROJET | Bibliothèque Decimo — RDC sous logements, Abidjan |
| PHASE | ESQ V5 — aménagement sur existant V4 |
| PLANCHE | A01 — Plan du rez-de-chaussée — aménagement |
| ÉCHELLE | 1/50 · format A3 |
| MAQUETTE | v5/DECIMO_ESQ_V5.ifc (IFC4) · sha256 985f48d48b… |
| DATE | Octobre 2026 · indice A |

Esquisse : cotes et surfaces indicatives, existant V4 à relever sur site.

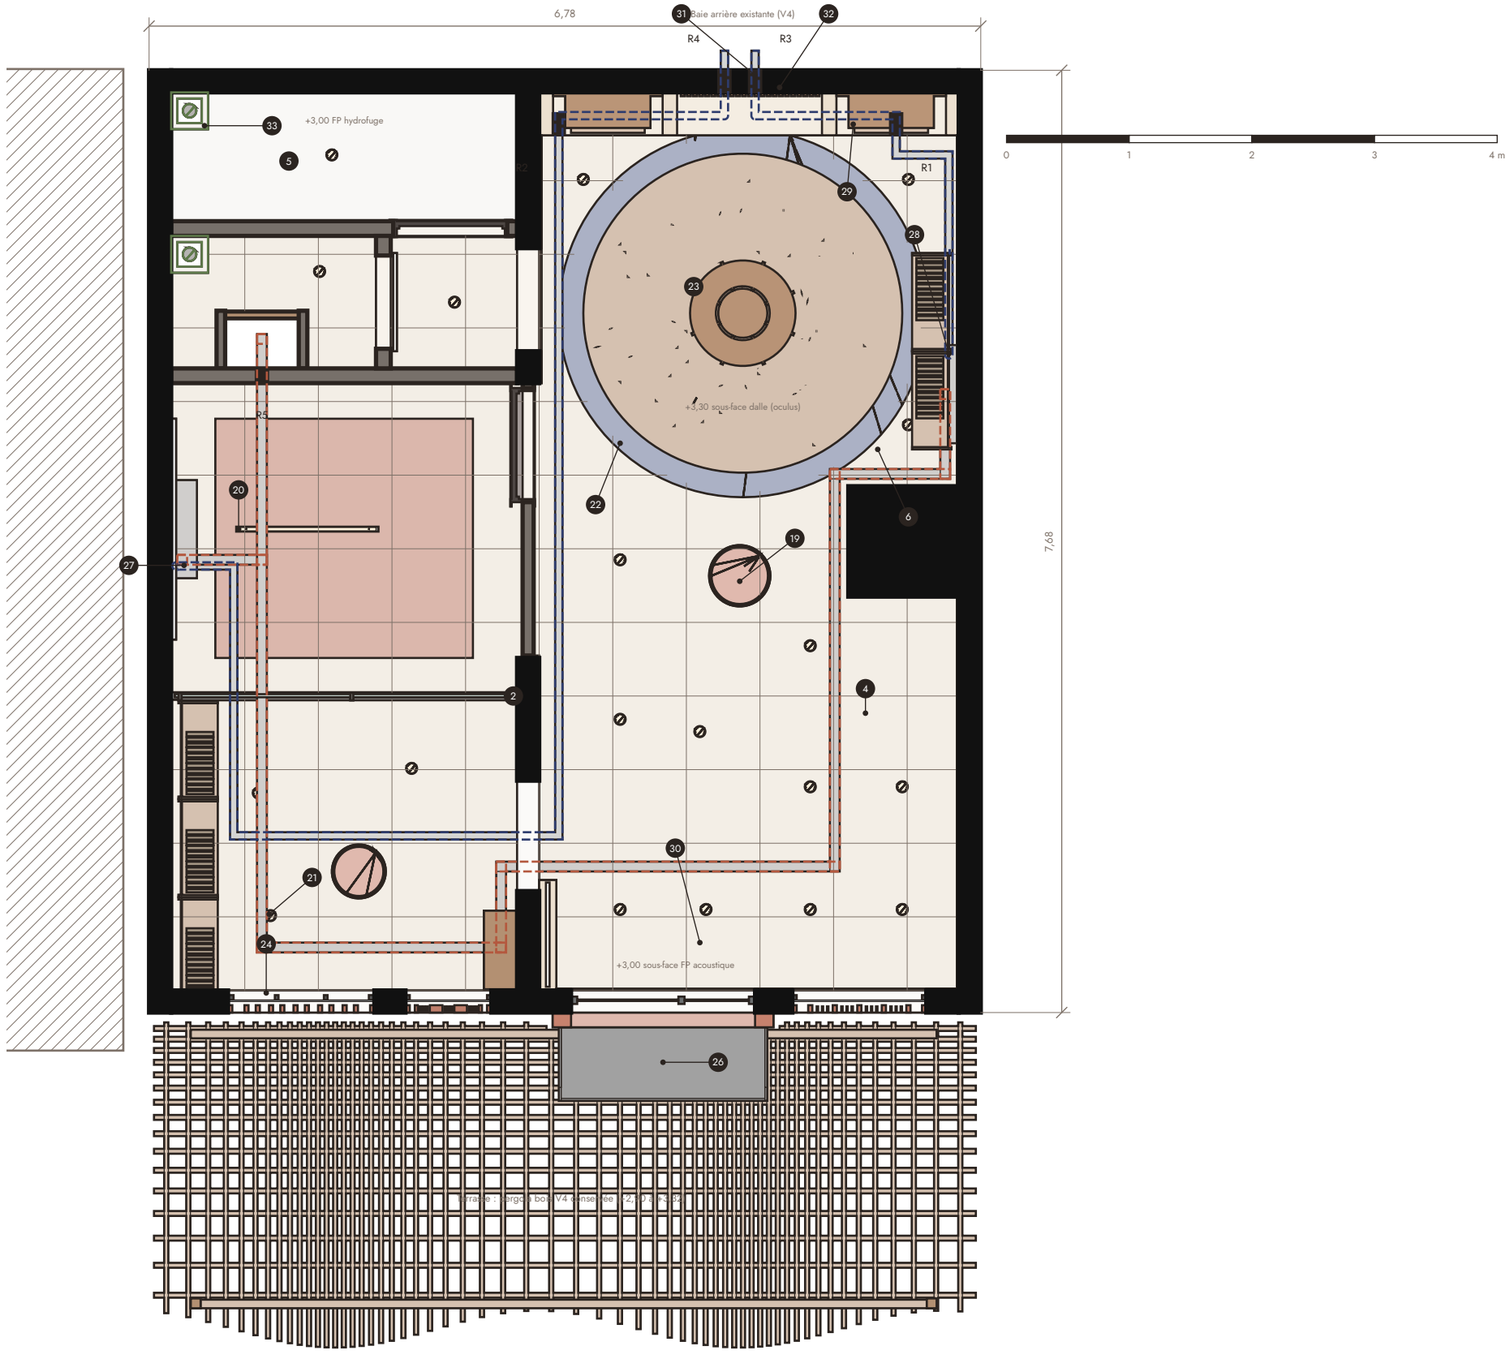


K&Démi

# Bibliothèque Decimo

## Plan de faux-plafond et réseaux

Vu de dessous (plan réfléchi) · Échelle 1/50 (A3) · Coupe à +2,00

### PRINCIPES (HYPOTHÈSES ESQ AHOUA)

Faux-plafond acoustique +3,00 (dalles 0,60, ép. 40 mm) ; plénum 0,26 sous dalle haute (minimum 0,25).
Aucun percement dans poteaux, voiles ni dalle haute : liaisons splits et câbles
cheminent en plénum puis dans le doublage des niches, et sortent par la baie arrière
EXISTANTE (imposte : panneau passe-liaisons 32, réservations R3, R4 Ø 0,10).
Splits 9 000 BTU/h en partie haute de murs pleins, hors aplomb des tables ;
condensats relevés par mini-pompe (pas d'évacuation gravitaire possible).
Câbles : placard technique › plénum (R5 dans cloison placo) › tableau divisionnaire.
Descentes EU/EV de l'immeuble : coffrages 0,30 × 0,30, position à relever sur site.

### REPÈRES DE L'AMÉNAGEMENT V5


- 2 Cloison légère / retombée BA13 (ajout V5)
- 4 Faux-plafond acoustique (+3,00, plénum 0,26)
- 5 Faux-plafond hydrofuge WC (+3,00)
- 6 Oculus Ø 2,80 : bandeau iroko, sous-face de dalle indigo
- 19 Suspension terre cuite 2700 K
- 20 Linéaire suspendu acier noir 2700 K
- 21 Downlight encastré Ø 90, 2700 K
- 22 Anneau LED indirect de l'oculus
- 23 Anneau LED sous la canopée
- 24 Réglette LED de vitrine
- 26 Spot sous marquise IP65
- 27 Split mural 9 000 BTU/h (2,6 kW)
- 28 Mini-pompe de relevage des condensats
- 29 Liaisons split (faux-plafond -> doublage -> baie arrière)
- 30 Chemin de câbles 80 x 40 en plénum
- 31 Réservation Ø 0,10 (hors structure)
- 32 Panneau passe-liaisons en imposte de la baie arrière
- 33 Coffrage acoustique 0,30 x 0,30 descente EU/EV (à relever)

### LÉGENDE

- Existant porteur coupé à +2,00
- Faux-plafond acoustique, trame 0,60
- Liaisons frigorifiques + condensats (plénum, doublage)
- Chemin de câbles 80 × 40 en plénum
- Descente EU/EV Ø 100 en coffrage (hypothèse)

| | |
|---|---|
| PROJET | Bibliothèque Decimo — RDC sous logements, Abidjan |
| PHASE | ESQ V5 — aménagement sur existant V4 |
| PLANCHE | A02 — Plan de faux-plafond et réseaux |
| ÉCHELLE | 1/50 · format A3 |
| MAQUETTE | v5/DECIMO_ESQ_V5.ifc (IFC4) · sha256 985f48d48b… |
| DATE | Octobre 2026 · indice A |

Esquisse : cotes et surfaces indicatives, existant V4 à relever sur site.

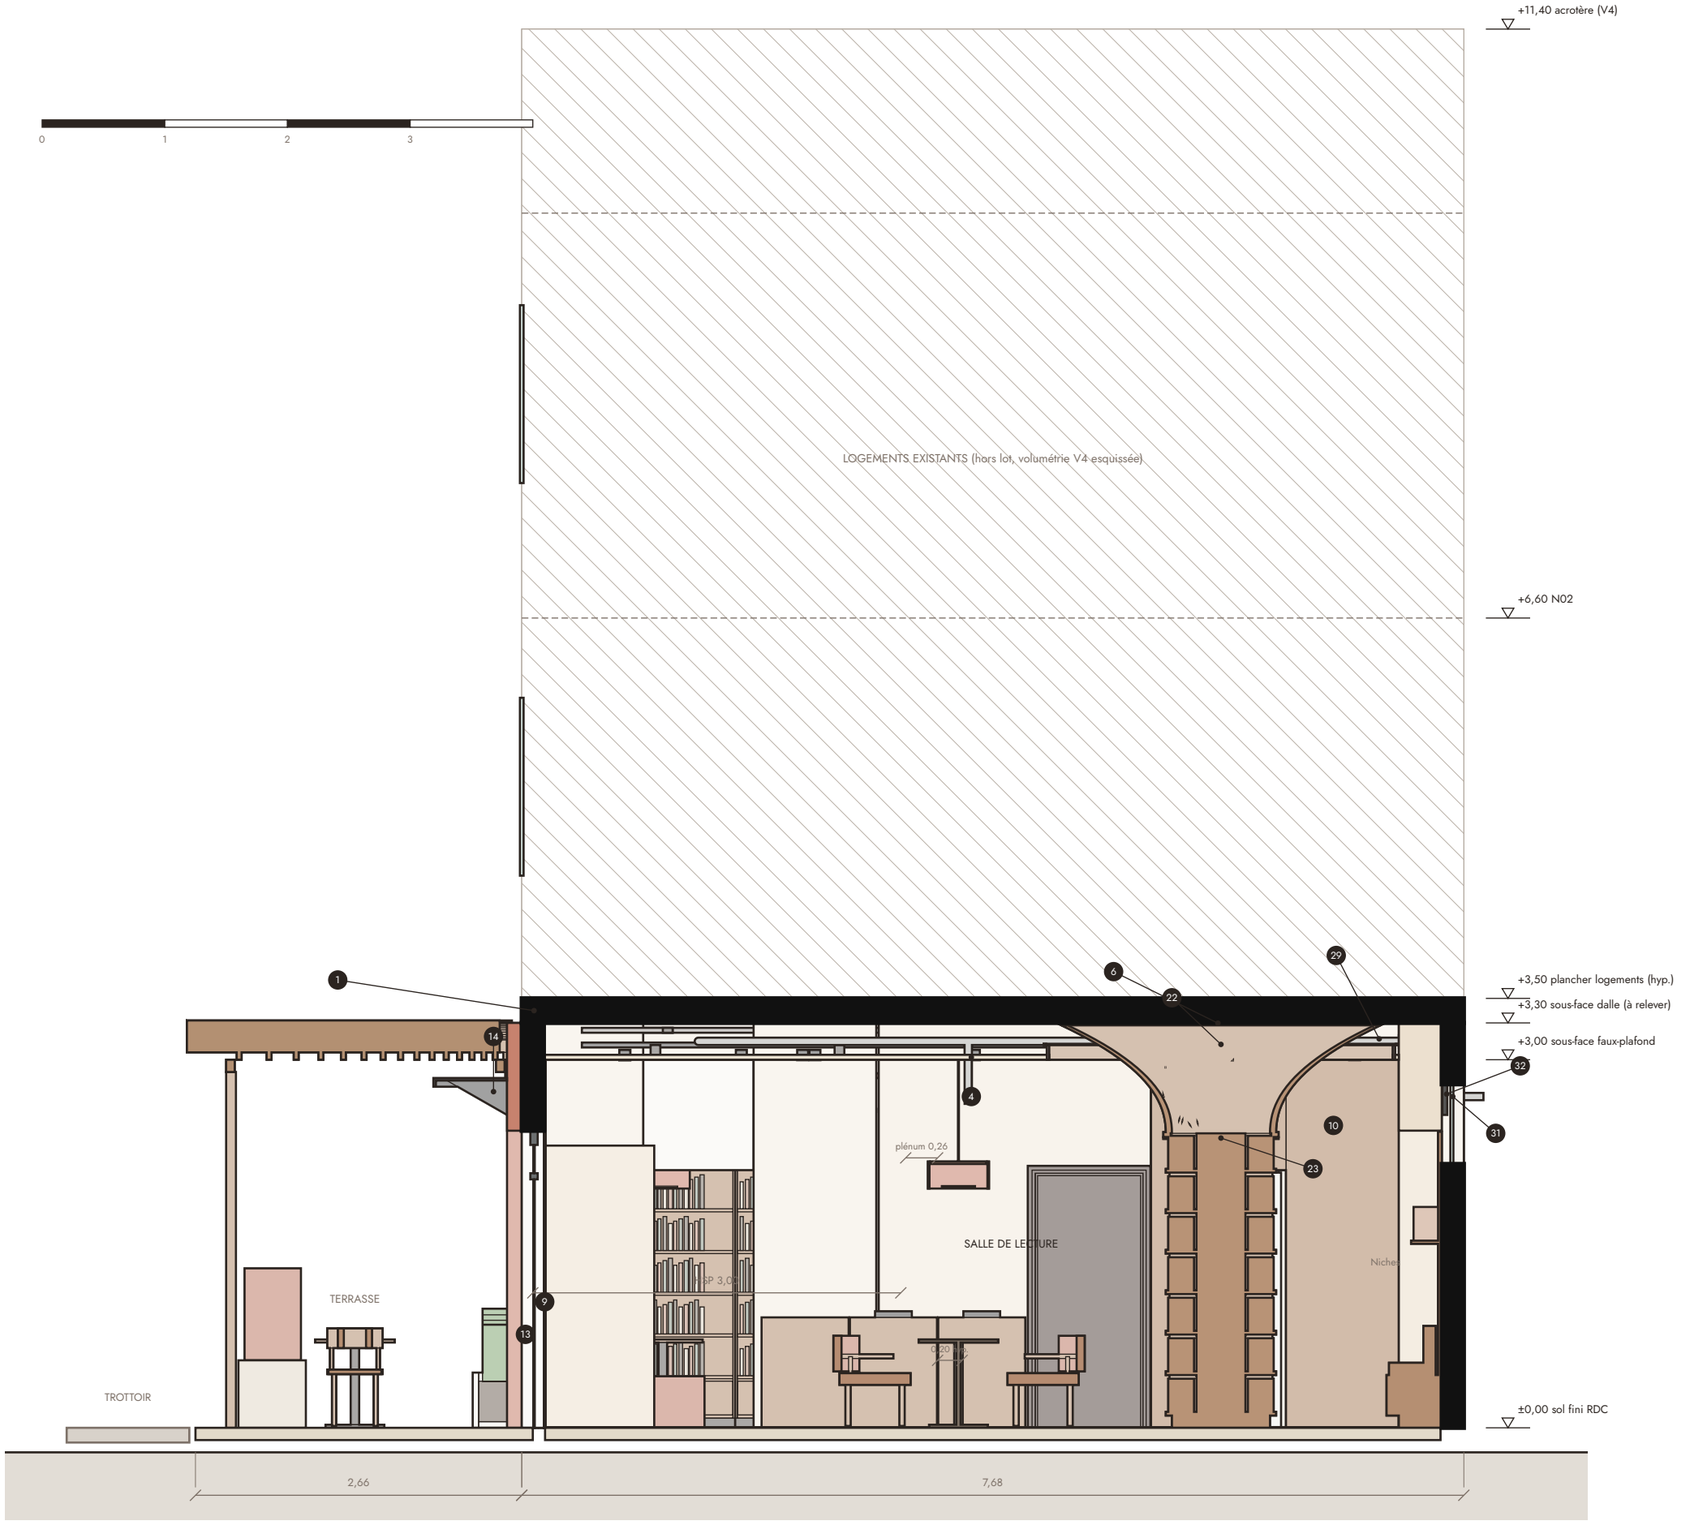


K&Démi

# Bibliothèque Decimo

## Coupe AA sur l'arbre à livres

Coupe x = 4,75 vers l'ouest · Échelle 1/50 (A3) · Logements existants esquissés

### LECTURE DE LA COUPE

Gros œuvre V4 repris tel quel (GlobalId, placements, géométrie : écarts nuls).
Dalle haute absente de la V4 : ajoutée sans modifier l'emprise (rep. 1), épaisseur 0,20 en hypothèse ; elle double la base du volume « logements » V4.
Faux-plafond acoustique abaissé à +3,00 : plénum 0,26 (minimum exigé 0,25).
Oculus Ø 2,80 autour de l'arbre à livres : sous-face de dalle laquée indigo, bandeau iroko et anneau LED indirect 2700 K (rep. 6, 22).
Liaisons split en plénum › doublage cintré des niches › imposte de la baie arrière existante (panneau 32, réservations R3/R4 Ø 0,10) : aucune traversée de poteau, voile ou dalle.

### REPÈRES DE L'AMÉNAGEMENT V5

1. Dalle haute existante (ajoutée, hypothèse ép. 0,20)
4. Faux-plafond acoustique (+3,00, plénum 0,26)
6. Oculus Ø 2,80 : bandeau iroko, sous-face de dalle indigo
9. Enduit terre (argile locale) 15 mm
10. Lambris iroko à claire-voie
13. Claustras terre cuite : inserts Adinkrahene et Eban
14. Marquise acier noir (débord 0,60)
22. Anneau LED indirect de l'oculus
23. Anneau LED sous la canopée
29. Liaisons split (faux-plafond -> doublage -> baie arrière)
31. Réservation Ø 0,10 (hors structure)
32. Panneau passe-liaisons en imposte de la baie arrière

### LÉGENDE

- Existant porteur coupé et dalle haute (hypothèse)
- Logements existants (volumétrie V4, hors lot)
- Planchers des logements (esquisse)

| | |
|---|---|
| PROJET | Bibliothèque Decimo — RDC sous logements, Abidjan |
| PHASE | ESQ V5 — aménagement sur existant V4 |
| PLANCHE | A03 — Coupe AA sur l'arbre à livres |
| ÉCHELLE | 1/50 · format A3 |
| MAQUETTE | v5/DECIMO_ESQ_V5.ifc (IFC4) · sha256 985f48d48b… |
| DATE | Octobre 2026 · indice A |

Esquisse : cotes et surfaces indicatives, existant V4 à relever sur site.




K&Démi

# Bibliothèque Decimo

## Élévation de la devanture sur rue

Vue depuis la rue · Échelle 1/50 (A3) · Logements existants esquissés au-dessus

### DEVANTURE (DANS LES BAIES V4 EXISTANTES)

Baies cintrées A, B, C et portail d'entrée : ouvertures V4 inchangées.
A — vitrine en arche : châssis acier noir posé derrière le vitrage V4 (rep. 11), podium iroko à hauteur d'allège ; claustra V4 maintenu en avant (point ouvert).
B, C — châssis fixes acier noir fins (rep. 12).
Claustras terre cuite V4 conservés ; motifs géométriques d'inspiration Adinkra ajoutés en inserts : Adinkrahene (cercles concentriques) dans les anneaux, Eban (carrés emboîtés) dans les interstices (rep. 13).
Marquise acier noir fine au-dessus de la porte cintrée, débord 0,60 (rep. 14).
Pergola bois V4, jardinières et mobilier de terrasse conservés (vus en coupe à y = −2,95, au droit du trottoir).

### REPÈRES DE L'AMÉNAGEMENT V5

- 11 Vitrine en arche, châssis acier noir
- 12 Châssis fixes acier noir (baies B, C)
- 13 Claustras terre cuite : inserts Adinkrahene et Eban
- 14 Marquise acier noir (débord 0,60)
- 24 Réglette LED de vitrine
- 26 Spot sous marquise IP65


### LÉGENDE

- Coupé (poteaux de pergola, plan y = −2,95)
- Terre cuite (portail, claustras)
- Iroko (pergola, menuiseries)
- Vitrage V4
- Arbres d'alignement (contexte V4)


| | |
|---|---|
| PROJET | Bibliothèque Decimo — RDC sous logements, Abidjan |
| PHASE | ESQ V5 — aménagement sur existant V4 |
| PLANCHE | A04 — Élévation de la devanture sur rue |
| ÉCHELLE | 1/50 · format A3 |
| MAQUETTE | v5/DECIMO_ESQ_V5.ifc (IFC4) · sha256 985f48d48b… |
| DATE | Octobre 2026 · indice A |

Esquisse : cotes et surfaces indicatives, existant V4 à relever sur site.

Élévation intérieure Est — mur mitoyen enduit terre

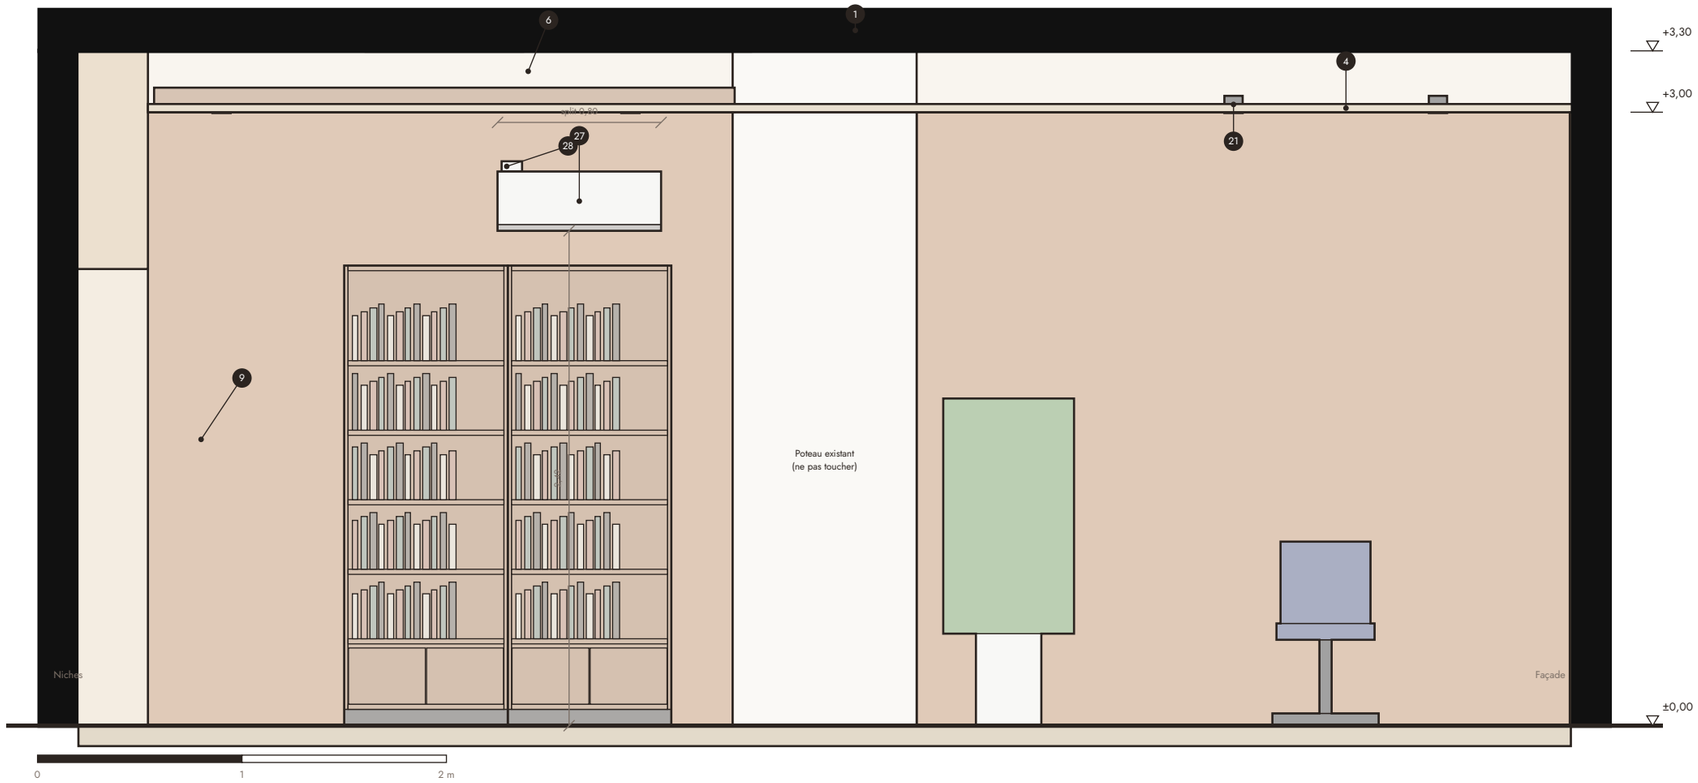


Élévation intérieure Nord — niches cintrées et baie arrière existante

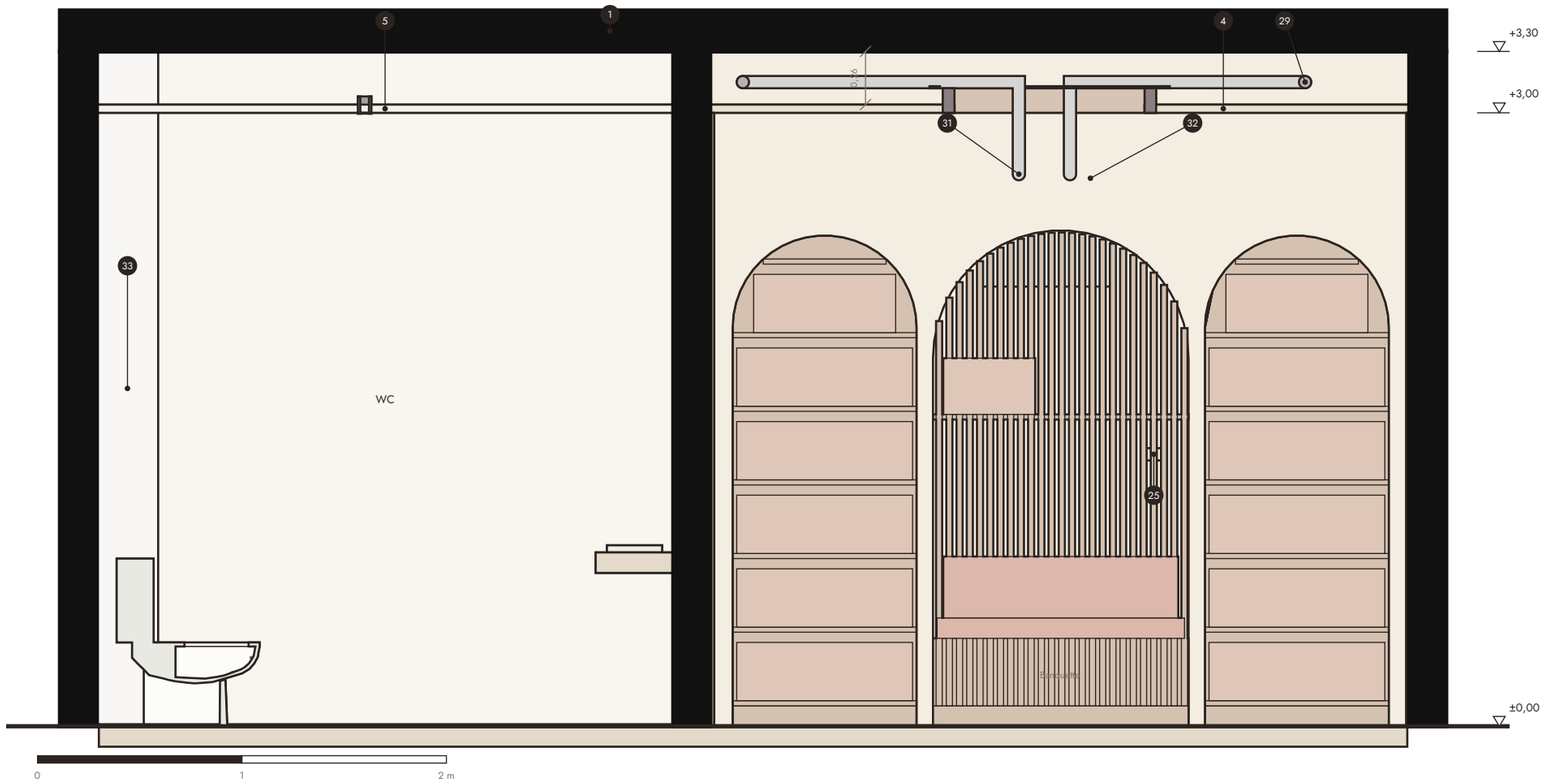


K&Démi

# Bibliothèque Decimo

## Élévations intérieures Est et Nord

Salle de lecture · Échelle 1/30 (A3)

### FINITIONS

Mur mitoyen est : enduit terre (argile locale) 15 mm, teinte sable (rep. 9).
Refend 4350608 côté lecture : lambris iroko à claire-voie (rep. 10).
Sols : terrazzo sable (salle de lecture), parquet iroko (coin lecture, réunion).
Faux-plafond acoustique blanc cassé +3,00 ; WC : plaque hydrofuge.
Split 1 en partie haute du mur est, au-dessus des rayonnages B01 et hors aplomb des tables ; mini-pompe de relevage (rep. 28).
Fond : niches V4 et doublage cintré conservés ; liaisons dans le doublage, sortie par l'imposte de la baie arrière existante (rep. 31, 32).

### REPÈRES DE L'AMÉNAGEMENT V5

- 1 Dalle haute existante (ajoutée, hypothèse ép. 0,20)
- 4 Faux-plafond acoustique (+3,00, plénum 0,26)
- 5 Faux-plafond hydrofuge WC (+3,00)
- 6 Oculus Ø 2,80 : bandeau iroko, sous-face de dalle indigo
- 9 Enduit terre (argile locale) 15 mm
- 21 Downlight encastré Ø 90, 2700 K
- 25 Liseuse de lecture
- 27 Split mural 9 000 BTU/h (2,6 kW)
- 28 Mini-pompe de relevage des condensats
- 29 Liaisons split (faux-plafond -> doublage -> baie arrière)
- 31 Réservation Ø 0,10 (hors structure)
- 32 Panneau passe-liaisons en imposte de la baie arrière
- 33 Coffrage acoustique 0,30 x 0,30 descente EU/EV (à relever)


### LÉGENDE

- Existant porteur et dalle haute coupés
- Cloison légère coupée
- Faux-plafond, revêtements coupés


| | |
|---|---|
| PROJET | Bibliothèque Decimo — RDC sous logements, Abidjan |
| PHASE | ESQ V5 — aménagement sur existant V4 |
| PLANCHE | A05 — Élévations intérieures Est et Nord |
| ÉCHELLE | 1/30 · format A3 |
| MAQUETTE | v5/DECIMO_ESQ_V5.ifc (IFC4) · sha256 985f48d48b… |
| DATE | Octobre 2026 · indice A |

Esquisse : cotes et surfaces indicatives, existant V4 à relever sur site.

Élévation intérieure Sud — façade vue de l'intérieur (coupe y = 0,80)

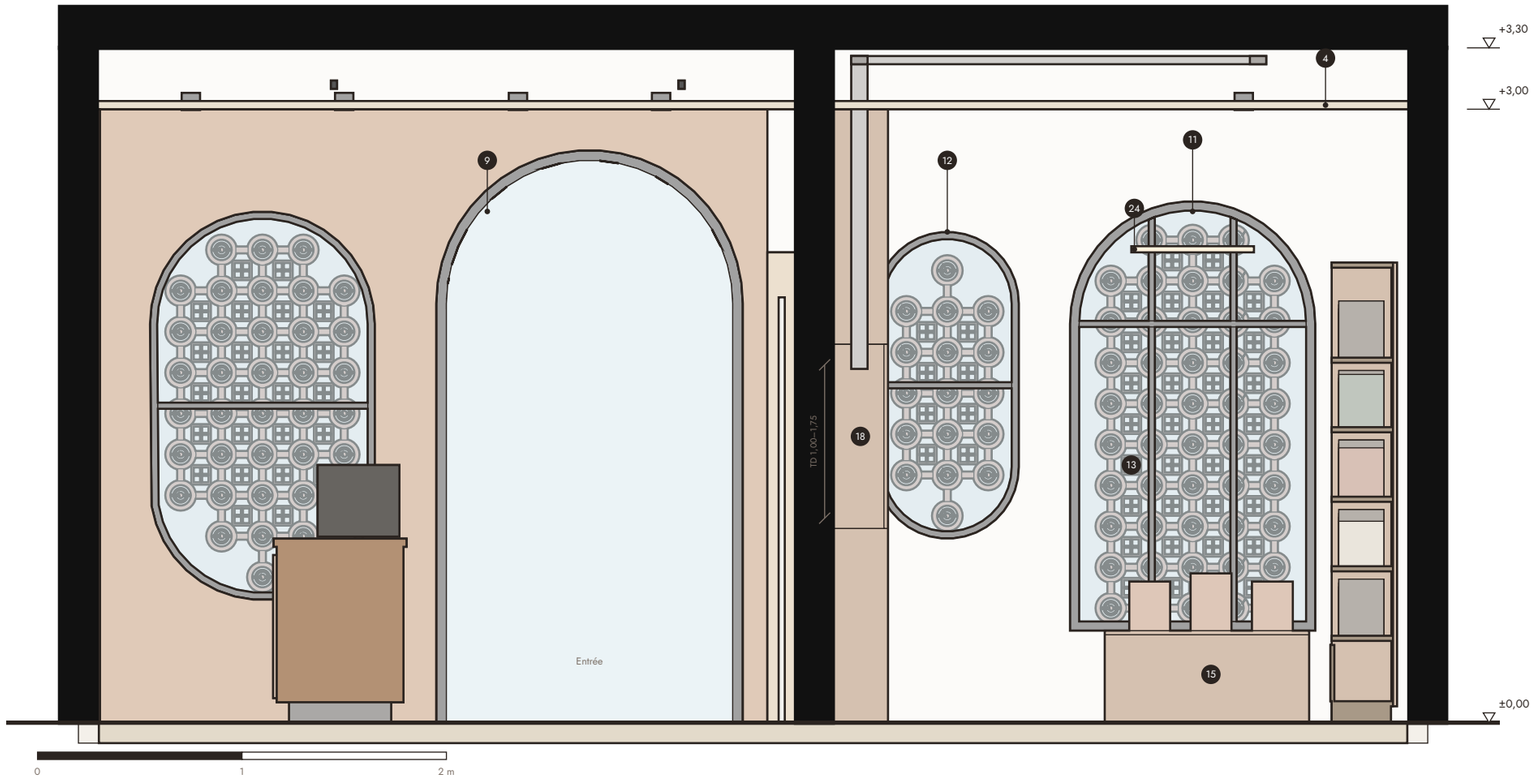


Élévation intérieure Ouest — coin lecture, réunion, rangement, WC (coupe x = 2,85)

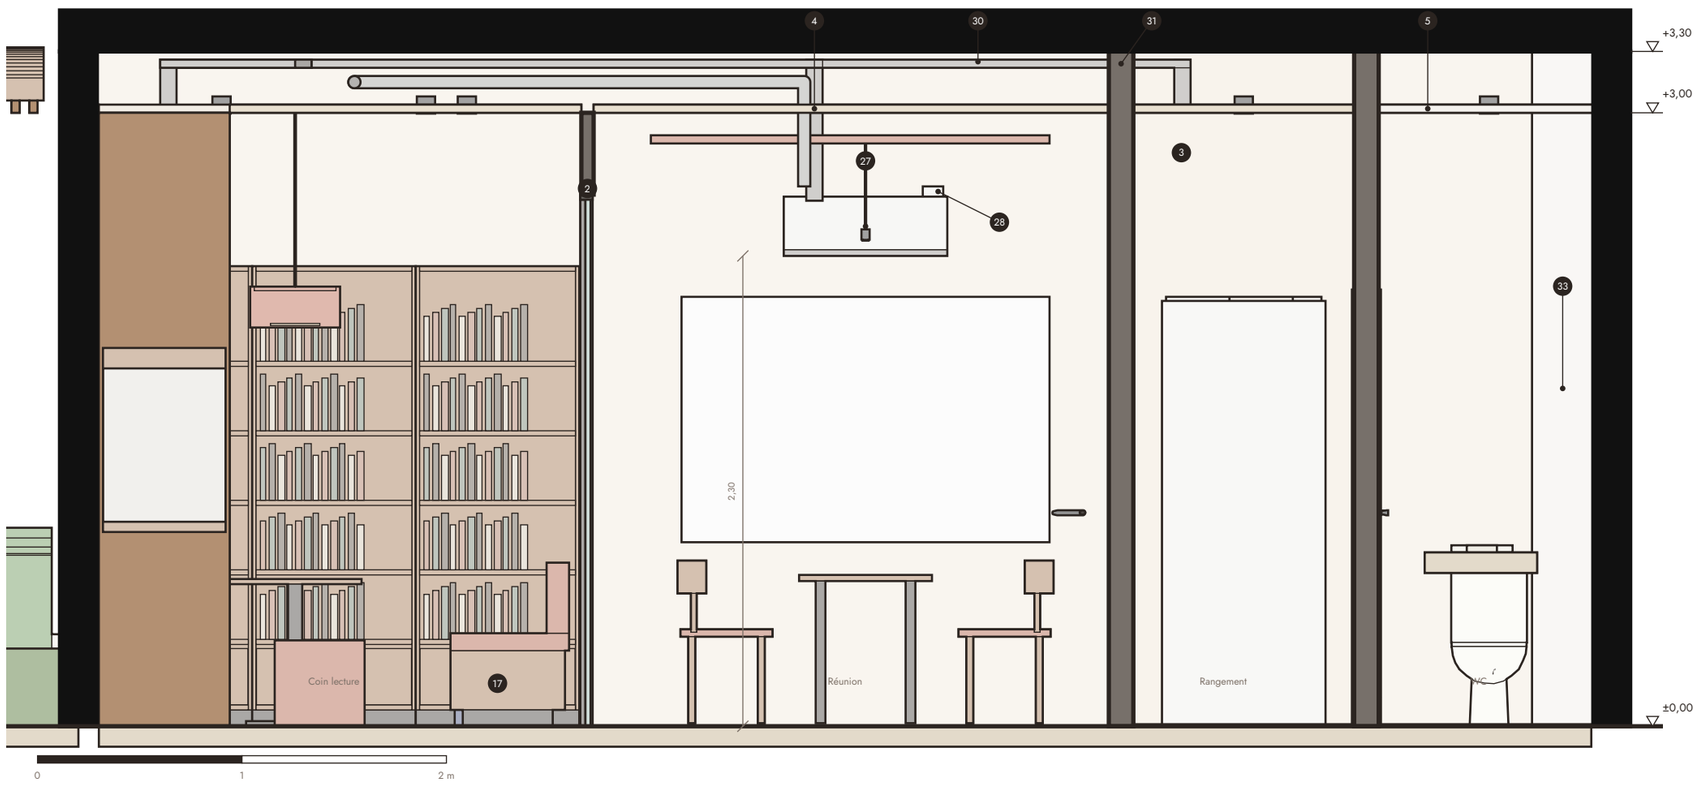


K&Démi

# Bibliothèque Decimo

## Élévations intérieures Sud et Ouest

Façade intérieure, coin lecture, réunion, locaux de service · Échelle 1/30 (A3)

### TECHNIQUE (HYPOTHÈSES ESQ AHOUA)

Tableau divisionnaire ~0,60 × 0,25 encastré dans un habillage iroko près de l'entrée (coin lecture), 1,00 m libre devant, loin de tout point d'eau (rep. 18).
Placard technique 0,60 × 0,40 net, porte pleine : arrivée électrique de l'immeuble, baie informatique, coffret des liaisons clim (rep. 3).
Split 2 en partie haute du mur mitoyen de la réunion, hors aplomb de la table.
Coffrages acoustiques 0,30 × 0,30 des descentes EU/EV (rep. 33) : « À relever sur site ». Pas de TGBT ni de groupe électrogène.

### REPÈRES DE L'AMÉNAGEMENT V5

- 2 Cloison légère / retombée BA13 (ajout V5)
- 3 Placard technique 0,60 x 0,40 net
- 4 Faux-plafond acoustique (+3,00, plénum 0,26)
- 5 Faux-plafond hydrofuge WC (+3,00)
- 9 Enduit terre (argile locale) 15 mm
- 11 Vitrine en arche, châssis acier noir
- 12 Châssis fixes acier noir (baies B, C)
- 13 Claustras terre cuite : inserts Adinkrahene et Eban
- 15 Podium de vitrine iroko (h 0,45 = allège baie A)
- 17 Pouf de lecture indigo
- 18 Tableau divisionnaire encastré dans habillage iroko
- 24 Réglette LED de vitrine
- 27 Split mural 9 000 BTU/h (2,6 kW)
- 28 Mini-pompe de relevage des condensats
- 30 Chemin de câbles 80 x 40 en plénum
- 31 Réservation Ø 0,10 (hors structure)
- 33 Coffrage acoustique 0,30 x 0,30 descente EU/EV (à relever)

### LÉGENDE

- Existant porteur coupé
- Cloison légère coupée
- Vitrage

| | |
|---|---|
| PROJET | Bibliothèque Decimo — RDC sous logements, Abidjan |
| PHASE | ESQ V5 — aménagement sur existant V4 |
| PLANCHE | A06 — Élévations intérieures Sud et Ouest |
| ÉCHELLE | 1/30 · format A3 |
| MAQUETTE | v5/DECIMO_ESQ_V5.ifc (IFC4) · sha256 985f48d48b… |
| DATE | Octobre 2026 · indice A |


Esquisse : cotes et surfaces indicatives, existant V4 à relever sur site.




01 · Devanture sur rue, vue piéton



02 · Intérieur depuis l'entrée

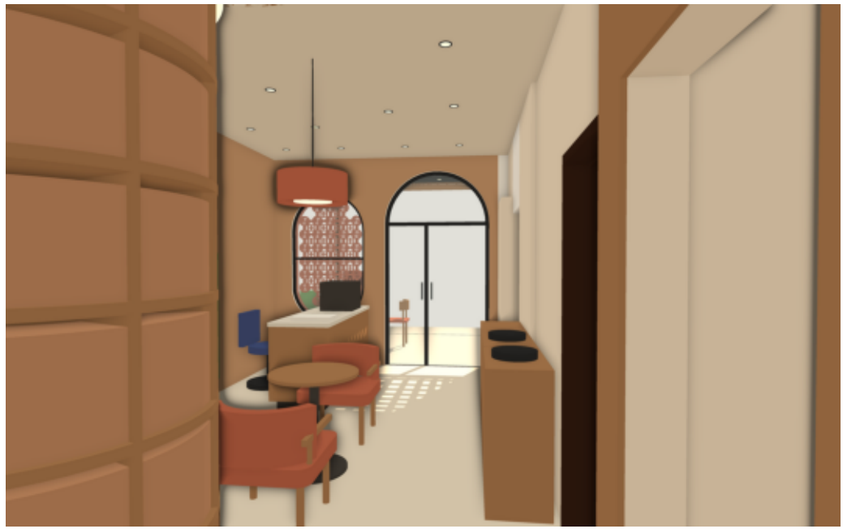

03 · Intérieur vers la devanture

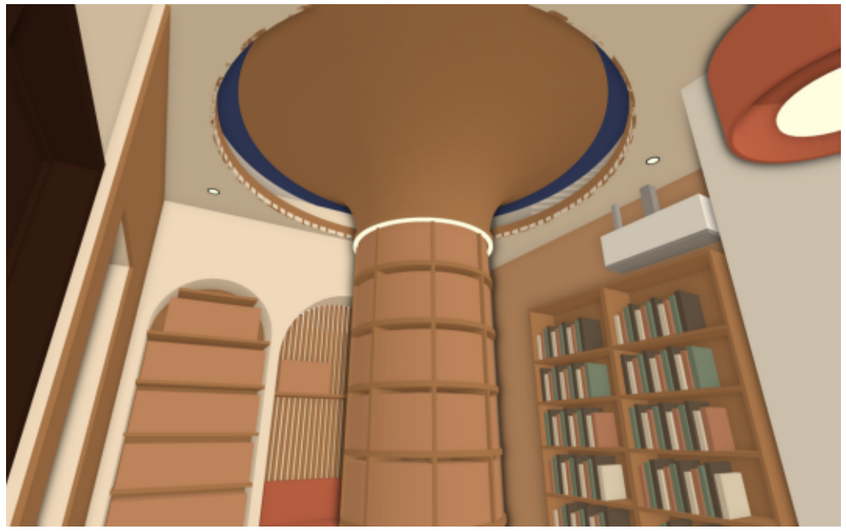

04 · Arbre à livres et oculus indigo



05 · Coin lecture et vitrine en arche



06 · Coin lecture — traits

K&Démi

# Bibliothèque Decimo

## Vues 3D de la maquette

Rendus OpenGL tirés de l'IFC V5 (v5/vues_rendu) · sans échelle


### VUES POUR LES RENDUS FINAUX

Cinq cadrages fixes, exportés en 2560 × 1600 px dans v5/vues_rendu : <nom>_ombre.png (couleurs matériaux IFC, ombre portée, sans légende), <nom>_traits.png (silhouettes et arêtes) et <nom>_camera.json (position, cible, FOV, focale équivalente 24 × 36) pour un cadrage reproductible lors de la génération des rendus (fal).


Les vues sont recalculées à partir de l'IFC par :
python3 v5/scripts/vues_rendu.py

| | |
|---|---|
| PROJET | Bibliothèque Decimo — RDC sous logements, Abidjan |
| PHASE | ESQ V5 — aménagement sur existant V4 |
| PLANCHE | A07 — Vues 3D de la maquette |
| ÉCHELLE | sans échelle · format A3 |
| MAQUETTE | v5/DECIMO_ESQ_V5.ifc (IFC4) · sha256 985f48d48b… |
| DATE | Octobre 2026 · indice A |

Esquisse : cotes et surfaces indicatives, existant V4 à relever sur site.

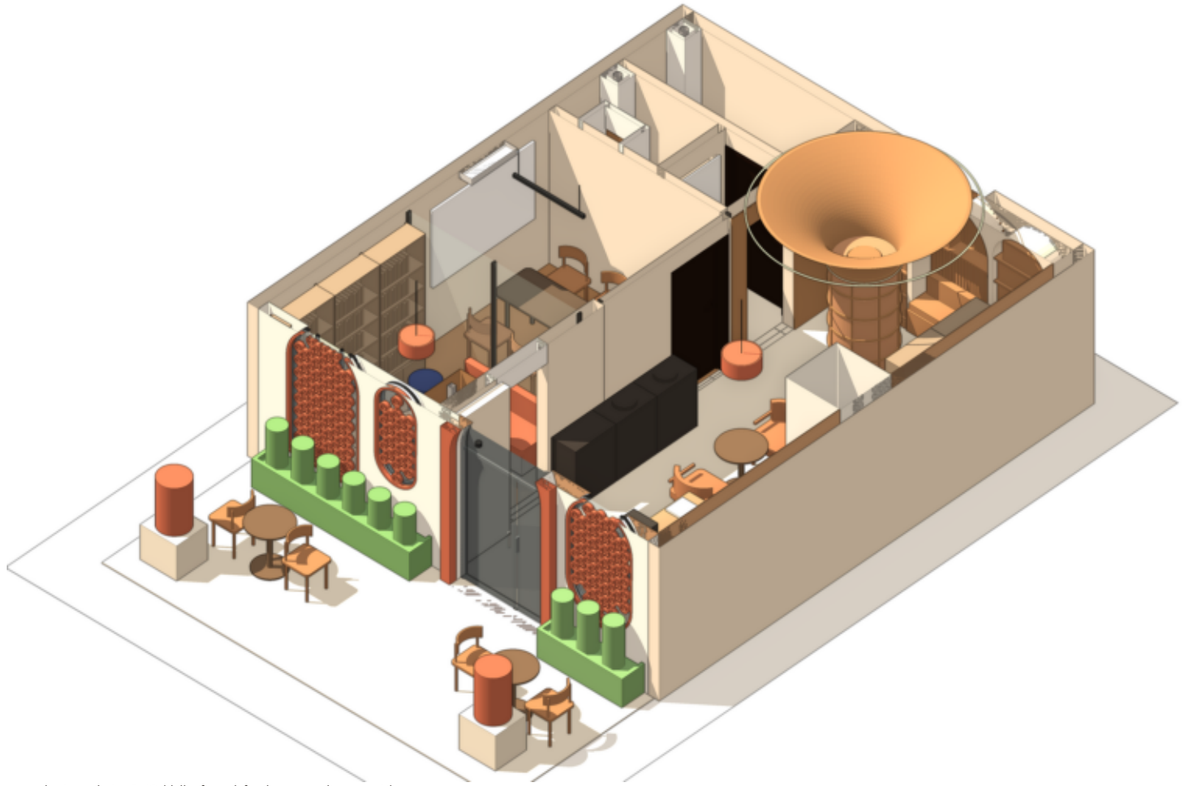

Axonométrie de l'aménagement, coupe horizontale à +2,40 (dalle, faux-plafonds et pergola masqués)

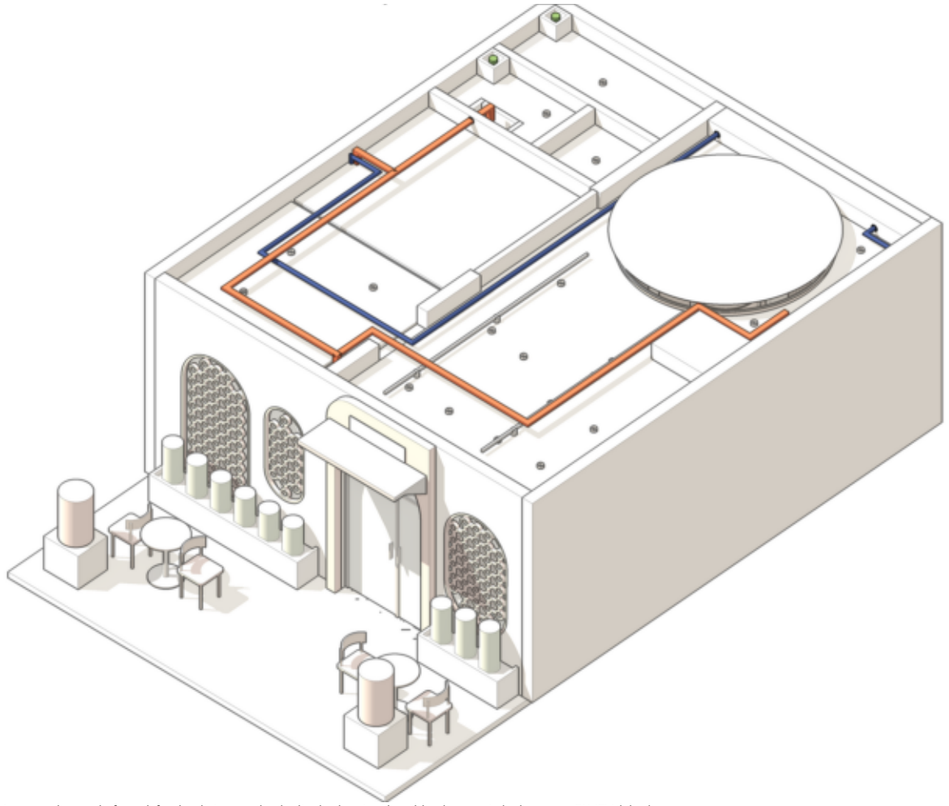

Axonométrie technique, dalle masquée : réseaux en plénum au-dessus du faux-plafond — liaisons splits (indigo), chemins de câbles (terre cuite), descentes EU/EV (olive)

K&Démi

# Bibliothèque Decimo

## Axonométries

Aménagement coupé à +2,40 · Réseaux techniques en plénum · sans échelle

### LECTURE

Haut : volumes de l'aménagement dans l'existant V4 — arbre à livres, niches, rayonnages, comptoir, coin lecture, réunion, placard technique.
Bas : le cheminement des réseaux reste dans le plénum (+3,04 à +3,30) puis dans le doublage des niches, et sort par l'imposte de la baie arrière existante ; aucun poteau, voile ou dalle n'est traversé (vérification booléenne : v5/rapports/verif_v4_v5.md).
Vue orthographique depuis le sud-est, sans échelle.

| | |
|---|---|
| PROJET | Bibliothèque Decimo — RDC sous logements, Abidjan |
| PHASE | ESQ V5 — aménagement sur existant V4 |
| PLANCHE | A08 — Axonométries |
| ÉCHELLE | sans échelle · format A3 |
| MAQUETTE | v5/DECIMO_ESQ_V5.ifc (IFC4) · sha256 985f48d48b… |
| DATE | Octobre 2026 · indice A |

Esquisse : cotes et surfaces indicatives, existant V4 à relever sur site.



R1 · Devanture sur rue, vue piéton depuis le trottoir opposé, œil à 1,60 m



Vue source 01 : maquette IFC V5 ombrée, même caméra



Vue source 01 : traits et silhouettes

K&Démi

# La devanture

## Le seuil cintré sous la pergola

Rendu tiré de la maquette IFC V5

### CE QUE L'ON VOIT

Les quatre baies existantes de la V4 gardent leur forme. La vitrine en arche et son châssis en acier noir se posent dans la baie A, la porte vitrée dans le portail en enduit terre cuite. Les deux baies de claustra reçoivent les inserts Adinkra. La pergola en bois de la V4 abrite la terrasse de lecture.

### CONTRÔLE

Même caméra, mêmes baies, même pergola que la vue source. Le rendu ajoute la matière et la lumière. Les balcons qu'il avait inventés sur l'immeuble voisin ont été retirés : la maquette y montre un mur plein. Écart restant : les jardinières basses de la terrasse sont rendues comme des banquettes. La maquette fait foi.


### MÉTHODE

Chaque rendu part d'une vue exportée de l'IFC (v5/vues_rendu, position, cible et focale enregistrées). L'image est retravaillée en matière et lumière sans rien ajouter ni déplacer, puis comparée à sa vue source avant d'entrer au dossier.

| | |
|---|---|
| PROJET | Bibliothèque Decimo · RDC sous logements, Deux Plateaux, Abidjan |
| PHASE | ESQ V5 · aménagement sur existant V4 |
| PLANCHE | 13 · R1 Rendu de la devanture |
| ÉCHELLE | sans échelle · format A3 paysage |
| MAQUETTE | v5/DECIMO_ESQ_V5.ifc (IFC4) |
| DATE | 15 octobre 2026 · indice A |



R2a · Depuis l'entrée : la banque d'accueil, la salle de lecture et l'arbre à livres au fond

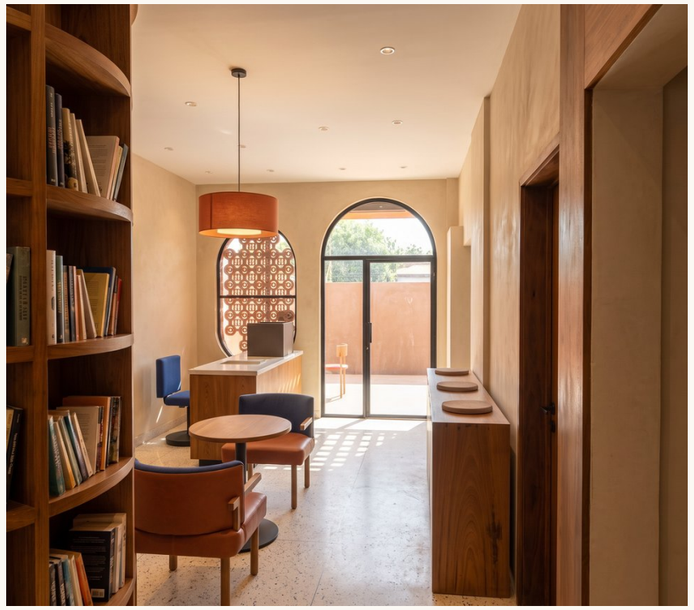

R2b · Vers la devanture : la porte cintrée et la claustra



R2c · Le coin lecture en vitrine, banquette et rayonnages iroko

K&Démi

# Les intérieurs

## Une pénombre fraîche, du bois et des livres

Rendus tirés des vues 02, 03 et 05 de la maquette

### MATIÈRES

Terrazzo clair au sol, enduit terre et chaux aux murs, iroko huilé pour la banque d'accueil, les rayonnages et les banquettes. Le faux-plafond acoustique à +3,00 garde 0,26 m de plénum sous la dalle de l'immeuble.

### LUMIÈRE

Downlights 2700 K encastrés, suspensions en terre cuite au-dessus des tables, lumière du jour filtrée par la claustra. Les splits sont posés en hauteur sur des murs pleins, jamais au-dessus des tables.


### CONTRÔLE

Comparés à leurs vues sources : murs, baies, mobilier et luminaires sont à leur place. Seuls les livres sur les étagères et la végétation sont ajoutés au rendu.

| | |
|---|---|
| PROJET | Bibliothèque Decimo · RDC sous logements, Deux Plateaux, Abidjan |
| PHASE | ESQ V5 · aménagement sur existant V4 |
| PLANCHE | 14 · R2 Rendus intérieurs |
| ÉCHELLE | sans échelle · format A3 paysage |
| MAQUETTE | v5/DECIMO_ESQ_V5.ifc (IFC4) |
| DATE | 15 octobre 2026 · indice A |




R3 · L'arbre à livres et l'oculus indigo de 2,80 m, anneau LED 2700 K

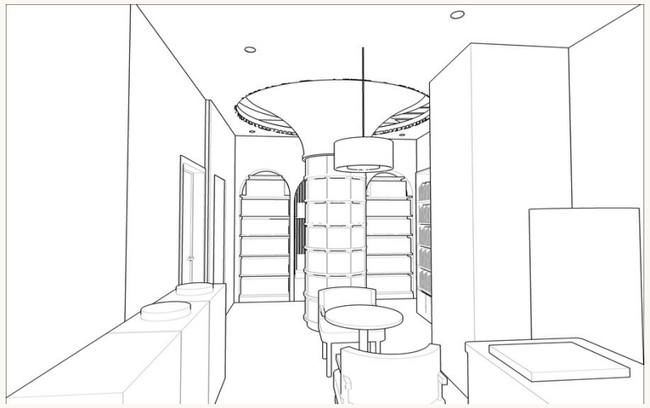

Vue source 02, traits



Vue source 03, traits

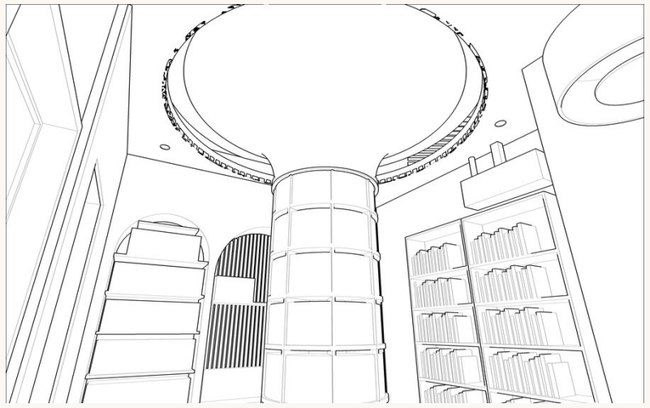

Vue source 04, traits

Les vues sources sont recalculées depuis l'IFC par v5/scripts/vues_rendu.py, avec la position, la cible et la focale enregistrées pour chaque caméra.

K&Démi

# L'arbre à livres

## Le seul objet fort de la salle

Rendu tiré de la vue 04 de la maquette

### L'OBJET

Un fût d'iroko porte des étagères circulaires et s'évase en canopée sous un oculus de 2,80 m. La sous-face de dalle est laquée indigo et un anneau LED indirect dessine le bord de l'oculus.

### DANS LA MAQUETTE

Modélisé en IfcFurniture sculptural au centre de la salle de lecture, avec l'oculus en IfcCovering et l'anneau en IfcLightFixture. Il est fixé sous la dalle sans la traverser : la charge, l'ancrage et la réaction au feu restent à valider par le BET.

| | |
|---|---|
| PROJET | Bibliothèque Decimo · RDC sous logements, Deux Plateaux, Abidjan |
| PHASE | ESQ V5 · aménagement sur existant V4 |
| PLANCHE | 15 · R3 L'arbre à livres |
| ÉCHELLE | sans échelle · format A3 paysage |
| MAQUETTE | v5/DECIMO_ESQ_V5.ifc (IFC4) |
| DATE | 15 octobre 2026 · indice A |

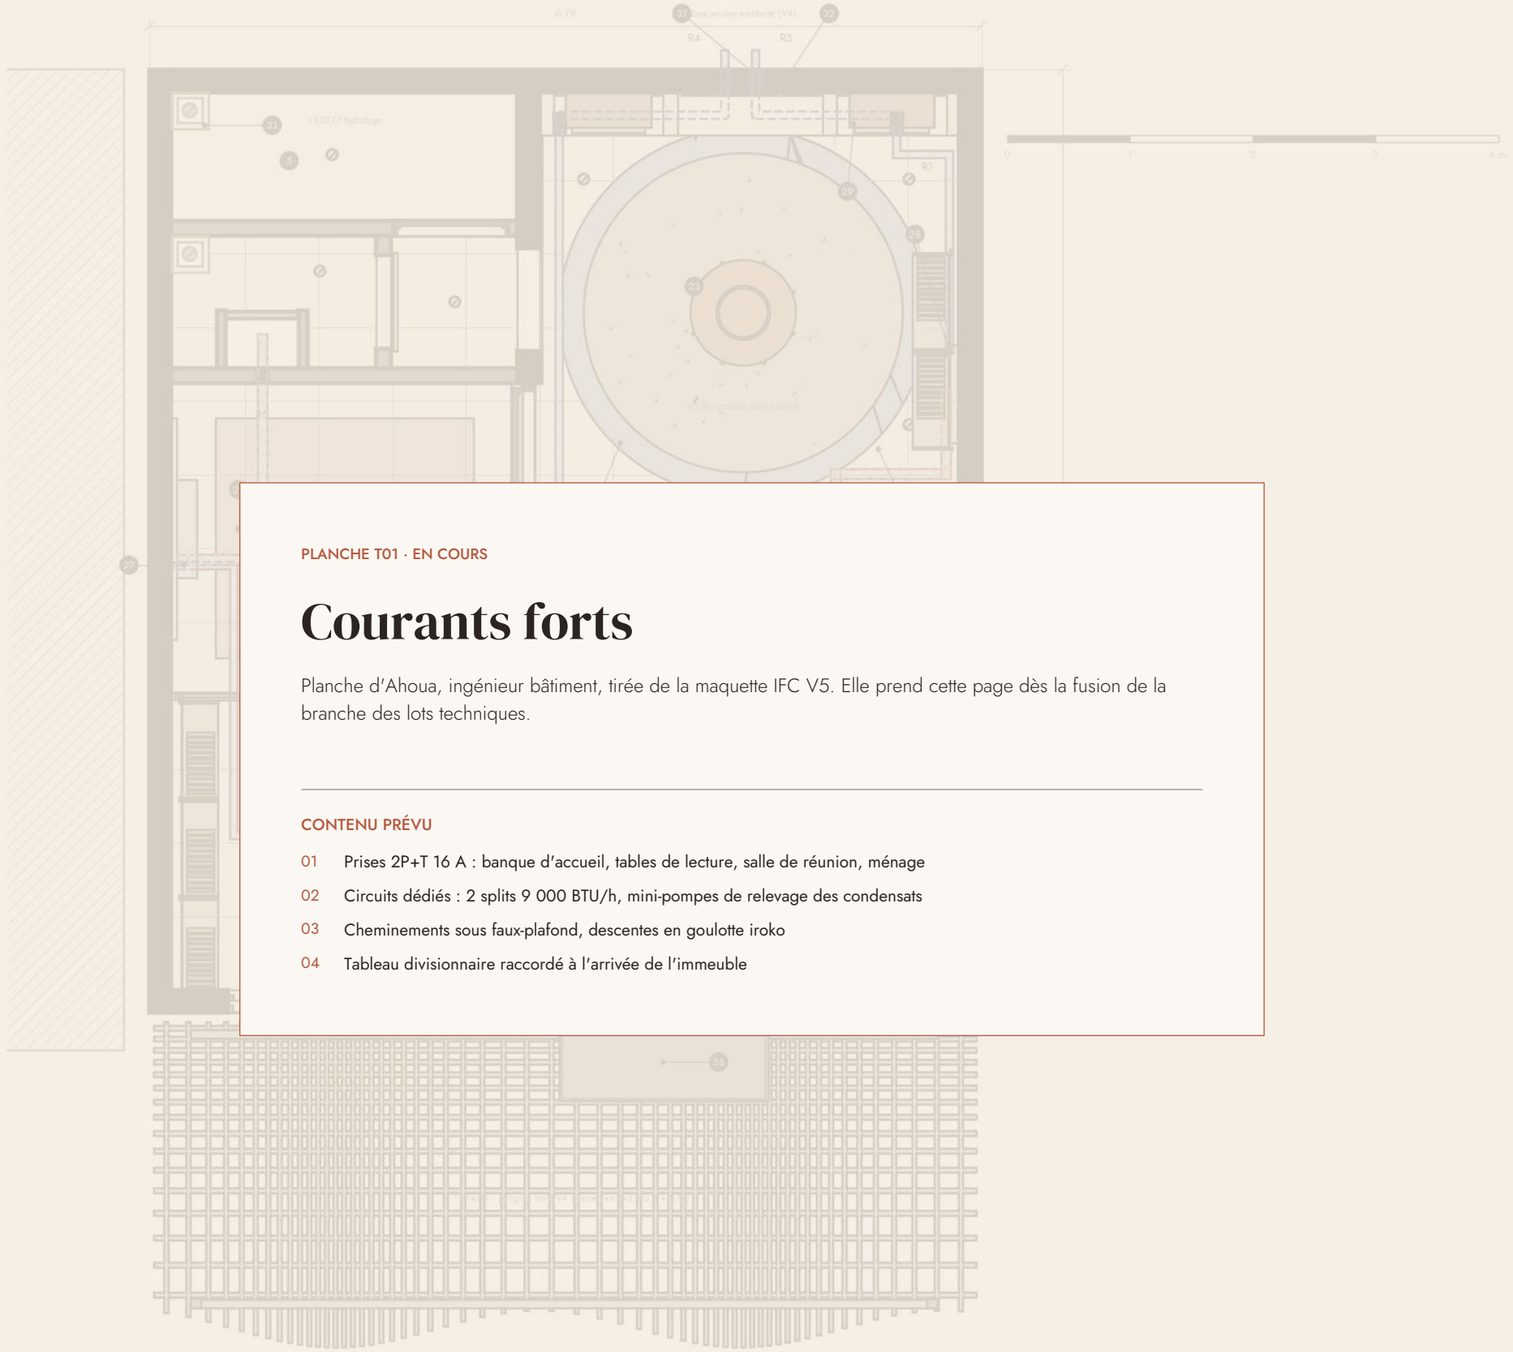


PLANCHE T01 · EN COURS

# Courants forts

Planche d'Ahoua, ingénieur bâtiment, tirée de la maquette IFC V5. Elle prend cette page dès la fusion de la branche des lots techniques.

## CONTENU PRÉVU

01 Prises 2P+T 16 A : banque d'accueil, tables de lecture, salle de réunion, ménage

02 Circuits dédiés : 2 splits 9 000 BTU/h, mini-pompes de relevage des condensats

03 Cheminements sous faux-plafond, descentes en goulotte iroko

04 Tableau divisionnaire raccordé à l'arrivée de l'immeuble

En fond : planche A02 de la maquette V5, à titre de repère

K&Démi

# Courants forts

## Proposition technique

T01 · Ahoua, ingénieur bâtiment

### DÉJÀ FIXÉ DANS LA MAQUETTE V5

| | |
|---|---|
| Tableau divisionnaire | 1 · 1,00 m dégagé |
| Splits muraux 9 000 BTU/h | 2 |
| TGBT, groupe électrogène | aucun, côté immeuble |
| Distance tableau / WC | 5,92 m |

### CADRE

Local commercial unique en RDC sous logements. L'immeuble porte le TGBT, le groupe et les colonnes : le projet part de ses attentes. Rien ne traverse la structure existante.

| | |
|---|---|
| PROJET | Bibliothèque Decimo · RDC sous logements, Deux Plateaux, Abidjan |
| PHASE | ESQ V5 · aménagement sur existant V4 |
| PLANCHE | 16 · T01 Courants forts |
| ÉCHELLE | sans échelle · format A3 paysage |
| MAQUETTE | v5/DECIMO_ESQ_V5.ifc (IFC4) |
| DATE | 15 octobre 2026 · indice A |



PLANCHE T02 · EN COURS

# Courants faibles et éclairage

Planche d'Ahoua, ingénieur bâtiment, tirée de la maquette IFC V5. Elle prend cette page dès la fusion de la branche des lots techniques.

## CONTENU PRÉVU

01 RJ45 cat. 6 : accueil, tables de travail, salle de réunion, point d'accès Wi-Fi en plafond

02 Baie de brassage murale dans le placard technique

03 Éclairage 2700 K : downlights, suspensions terre cuite, anneau LED de l'oculus, réglette de vitrine

04 Commandes par zone et détection au WC

En fond : planche A02 de la maquette V5, à titre de repère

K&Démi

# Courants faibles et éclairage

## Proposition technique

T02 · Ahoua, ingénieur bâtiment

### DÉJÀ FIXÉ DANS LA MAQUETTE V5

| | |
|---|---|
| Luminaires IfcLightFixture | 27 |
| Température de couleur | 2700 K |
| Placard technique net | 0,60 × 0,40 m |
| Plénum sous dalle | 0,26 m |

### CADRE

Local commercial unique en RDC sous logements. L'immeuble porte le TGBT, le groupe et les colonnes : le projet part de ses attentes. Rien ne traverse la structure existante.

| | |
|---|---|
| PROJET | Bibliothèque Decimo · RDC sous logements, Deux Plateaux, Abidjan |
| PHASE | ESQ V5 · aménagement sur existant V4 |
| PLANCHE | 17 · T02 Courants faibles et éclairage |
| ÉCHELLE | sans échelle · format A3 paysage |
| MAQUETTE | v5/DECIMO_ESQ_V5.ifc (IFC4) |
| DATE | 15 octobre 2026 · indice A |




En fond : planche A01 de la maquette V5, à titre de repère

PLANCHE T03 · EN COURS

# Plomberie AEP, EU, EV

Planche d'Ahoua, ingénieur bâtiment, tirée de la maquette IFC V5. Elle prend cette page dès la fusion de la branche des lots techniques.

## CONTENU PRÉVU

01 Alimentation eau froide depuis l'attente de l'immeuble, vanne d'arrêt et compteur divisionnaire

02 WC 4350629 et lave-mains 4350630/4350631 de la V4 conservés

03 EU/EV vers les descentes existantes en coffrage 0,30 × 0,30

04 Condensats des splits relevés par mini-pompes vers EU

K&Démi

# Plomberie AEP, EU, EV

## Proposition technique

T03 · Ahoua, ingénieur bâtiment

### DÉJÀ FIXÉ DANS LA MAQUETTE V5

| | |
|---|---|
| Appareils sanitaires | WC + lave-mains (V4) |
| Coffrages EU/EV | 2 · à relever sur site |
| Réservations Ø 0,10 | 5 · hors structure |
| Pénétration dans la structure | 0 |

### CADRE

Local commercial unique en RDC sous logements. L'immeuble porte le TGBT, le groupe et les colonnes : le projet part de ses attentes. Rien ne traverse la structure existante.

| | |
|---|---|
| PROJET | Bibliothèque Decimo · RDC sous logements, Deux Plateaux, Abidjan |
| PHASE | ESQ V5 · aménagement sur existant V4 |
| PLANCHE | 18 · T03 Plomberie AEP, EU, EV |
| ÉCHELLE | sans échelle · format A3 paysage |
| MAQUETTE | v5/DECIMO_ESQ_V5.ifc (IFC4) |
| DATE | 15 octobre 2026 · indice A |

PLANCHE T04 · EN COURS

# Détails techniques

Planche d'Ahoua, ingénieur bâtiment, tirée de la maquette IFC V5. Elle prend cette page dès la fusion de la branche des lots techniques.


## CONTENU PRÉVU

01 Fixation non traversante de l'arbre à livres et de l'oculus sous dalle

02 Faux-plafond acoustique +3,00 et trappes de visite des splits

03 Châssis acier noir dans les baies cintrées V4, inserts claustra Adinkra

04 Passage des liaisons frigorifiques par la baie arrière existante

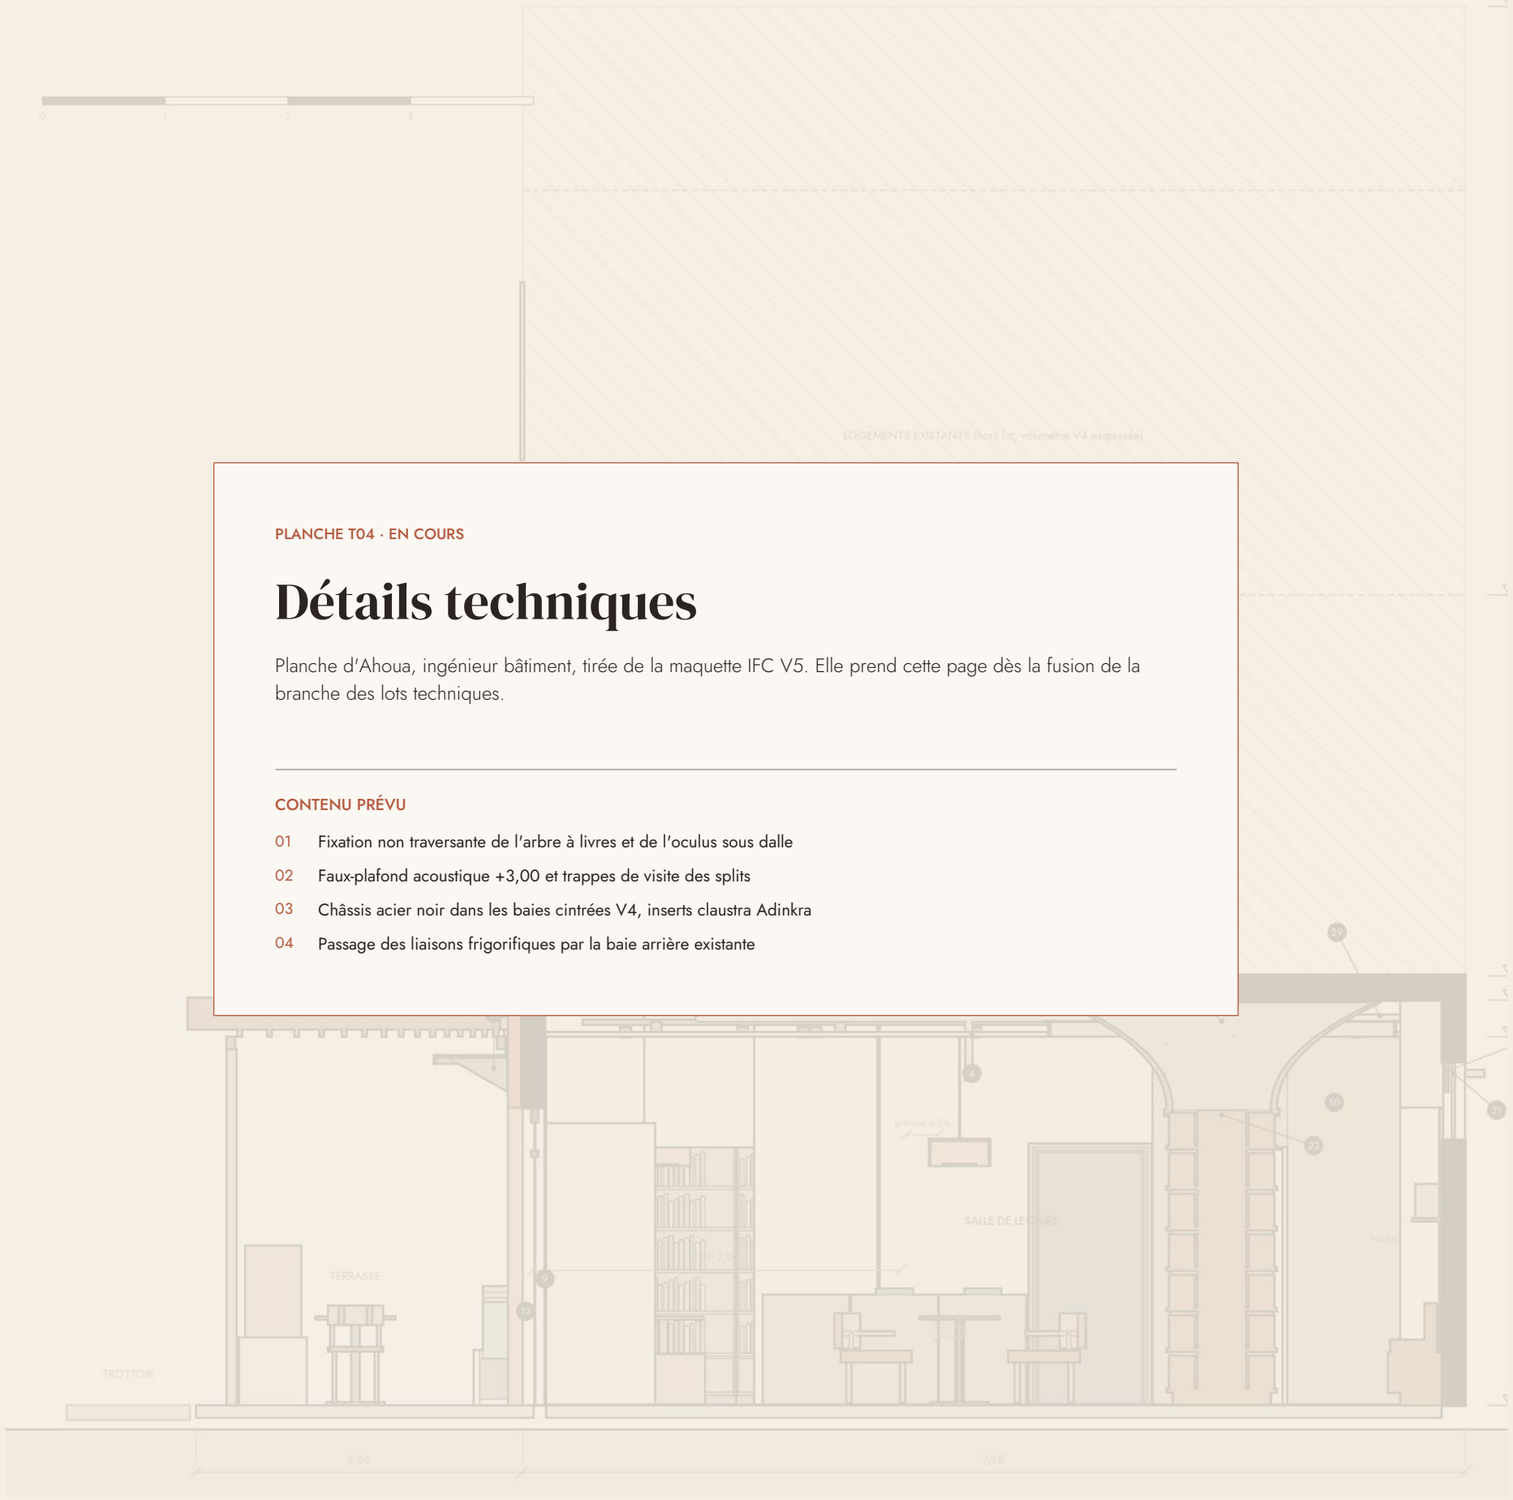


En fond : planche A03 de la maquette V5, à titre de repère

K&Démi

# Détails techniques

## Proposition technique

T04 · Ahoua, ingénieur bâtiment

### DÉJÀ FIXÉ DANS LA MAQUETTE V5

| | |
|---|---|
| Faux-plafond | +3,00 / +3,04 |
| Sous-face de dalle (hypothèse) | +3,30 |
| Liaisons frigorifiques | 2 faisceaux |
| Intersections structure | 0 |

### CADRE

Local commercial unique en RDC sous logements. L'immeuble porte le TGBT, le groupe et les colonnes : le projet part de ses attentes. Rien ne traverse la structure existante.

| | |
|---|---|
| PROJET | Bibliothèque Decimo · RDC sous logements, Deux Plateaux, Abidjan |
| PHASE | ESQ V5 · aménagement sur existant V4 |
| PLANCHE | 19 · T04 Détails techniques |
| ÉCHELLE | sans échelle · format A3 paysage |
| MAQUETTE | v5/DECIMO_ESQ_V5.ifc (IFC4) |
| DATE | 15 octobre 2026 · indice A |



PLANCHE T05 · EN COURS

# Unifilaire et bilan de puissance

Planche d'Ahoua, ingénieur bâtiment, tirée de la maquette IFC V5. Elle prend cette page dès la fusion de la branche des lots techniques.

## CONTENU PRÉVU

01 Schéma unifilaire du tableau divisionnaire : interrupteurs différentiels 30 mA, départs par usage

02 Bilan de puissance : éclairage, prises, climatisation, informatique

03 Puissance à demander au syndic et section du câble d'alimentation

04 Note technique et contrôle V4/V5 à 0 écart

En fond : planche A02 de la maquette V5, à titre de repère

K&Démi

# Unifilaire et bilan de puissance

## Proposition technique

T05 · Ahoua, ingénieur bâtiment

### DÉJÀ FIXÉ DANS LA MAQUETTE V5

| | |
|---|---|
| Départs clim dédiés | 2 |
| Protection des personnes | DDR 30 mA |
| Puissance souscrite | à confirmer |
| Écart V4/V5 | 0 |

### CADRE

Local commercial unique en RDC sous logements. L'immeuble porte le TGBT, le groupe et les colonnes : le projet part de ses attentes. Rien ne traverse la structure existante.

| | |
|---|---|
| PROJET | Bibliothèque Decimo · RDC sous logements, Deux Plateaux, Abidjan |
| PHASE | ESQ V5 · aménagement sur existant V4 |
| PLANCHE | 20 · T05 Unifilaire et bilan de puissance |
| ÉCHELLE | sans échelle · format A3 paysage |
| MAQUETTE | v5/DECIMO_ESQ_V5.ifc (IFC4) |
| DATE | 15 octobre 2026 · indice A |

| ÉLÉMENT | D.A | MAQUETTE IFC V5 | PLANS | RENDUS |
|---|---|---|---|---|
| Devanture : 4 baies V4, vitrine en arche, portail terre cuite, claustra Adinkra | p. 04 | IfcWindow, IfcDoor, IfcMember dans les baies V4 | A01, A04 | R1 |
| Arbre à livres et oculus indigo Ø 2,80 | p. 04 | IfcFurniture, IfcCovering, anneau IfcLightFixture | A01, A02, A03 | R2, R3 |
| Matériaux : terrazzo, iroko, enduit terre, chaux, acier noir | p. 04 | IfcMaterial et styles de surface D.A | A05, A06 | R1 à R3 |
| Lumière 2700 K | p. 04 | 27 IfcLightFixture | A02 | R2, R3 |
| Programme du 14/10 : un seul WC, salle de réunion | · | IfcSpace 03 et 07 | A01 | · |
| Climatisation : 2 splits 9 000 BTU/h sur murs pleins, hors tables | p. 04 | 2 IfcUnitaryEquipment, 2 mini-pompes | A02 | R2 |
| Tableau divisionnaire, 1,00 m dégagé, loin de l'eau | · | IfcElectricDistributionBoard | A01, A02 | · |
| Placard technique 0,60 × 0,40, porte pleine | · | IfcSpace 05 et IfcDoor | A01, A02 | · |
| Descentes EU/EV de l'immeuble en coffrage 0,30 × 0,30 | · | Coffrages « à relever sur site » | A02 | · |
| Existant V4 : murs, poteau, ouvertures, emprise 6,78 × 7,68 | · | 141 / 141 identiques, 0 pénétration | toutes | toutes |
| Lots techniques : électricité, CFA, AEP, EU, EV, détails | · | branche lots techniques d'Ahoua, en cours | T01 à T05 | · |

## Points ouverts, à lever en APS

01 Relevé de l'existant : dalle haute (épaisseur 0,20 et sous-face +3,30 en hypothèse), descentes EU/EV, arrivée électrique de l'immeuble.

02 BET : statut porteur des refends en agglos, fixations non traversantes sous dalle, charge et ancrage de l'arbre à livres et de l'oculus.

03 Copropriété : sortie des liaisons de clim et des unités extérieures en courette, adaptation de l'imposte de la baie arrière.

04 MOA : maintien des claustras V4 devant la vitrine de la baie A, fabrication des inserts Adinkra avec l'artisan.

05 APS : reprise des rails et suspensions V4 qui tombent dans le plénum, condensats relevés par mini-pompes faute de pente gravitaire.

06 Accessibilité PMR du WC et réaction au feu des éléments en bois à vérifier.

07 Planches T01 à T05 d'Ahoua (courants forts, courants faibles et éclairage, AEP/EU/EV, détails, unifilaire et bilan) à insérer pages 16 à 20.

08 Rendu R1 : jardinières de la terrasse rendues en banquettes, à reprendre pour coller à la maquette.

**0 erreur**
validation IFC4, natif et variante Revit

**141 / 141**
produits V4 identiques en V5

**0**
pénétration d'un ajout dans la structure

**8**
espaces IfcSpace nommés et métrés

K&Démi

# Cohérence

## D.A, maquette, plans et technique

Contrôle croisé du 15 octobre 2026

### VALIDATIONS

IFC4 natif et variante maillée pour Revit : 0 erreur au validateur ifcopenshell 0.9.0, schéma et règles EXPRESS. Contre-vérification indépendante sur main : les 141 produits V4 sont retrouvés par GlobalId, placements et géométries identiques (écart 0), emprise 6,78 × 7,68 m, WC 4350629 et lave-mains 4350630/4350631 conservés.

### LIVRABLES

Maquette v5/DECIMO_ESQ_V5.ifc et sa variante maillée pour Revit, planches A01 à A08 en PDF, PNG et SVG, vues de rendu avec leurs caméras, rapports de vérification. Tout est sur la branche main du dépôt jeemake/bibliothequeNandjuiS.Simon.

### LECTURE

Les cotes et surfaces sont indicatives au stade de l'esquisse. L'existant V4 reste à relever sur site avant l'APS.

| | |
|---|---|
| PROJET | Bibliothèque Decimo · RDC sous logements, Deux Plateaux, Abidjan |
| PHASE | ESQ V5 · aménagement sur existant V4 |
| PLANCHE | 21 · Cohérence et points ouverts |
| ÉCHELLE | sans échelle · format A3 paysage |
| MAQUETTE | v5/DECIMO_ESQ_V5.ifc (IFC4) |
| DATE | 15 octobre 2026 · indice A |