


D1 — Faux-plafond acoustique et plénum · échelle 1/10

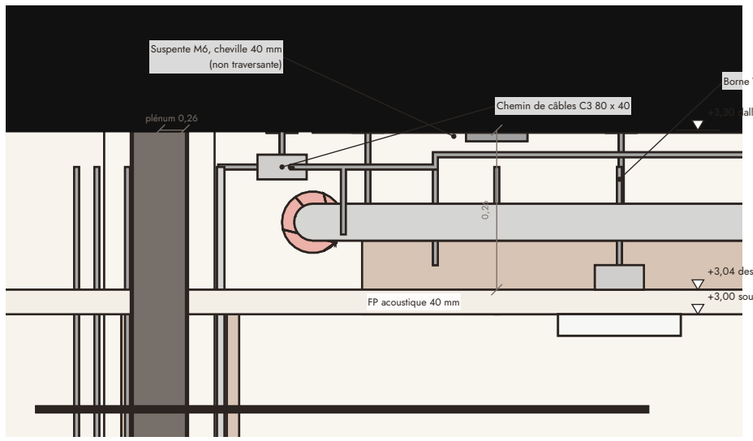


D3 — Placard technique (vue vers la cloison arrière) · échelle 1/20

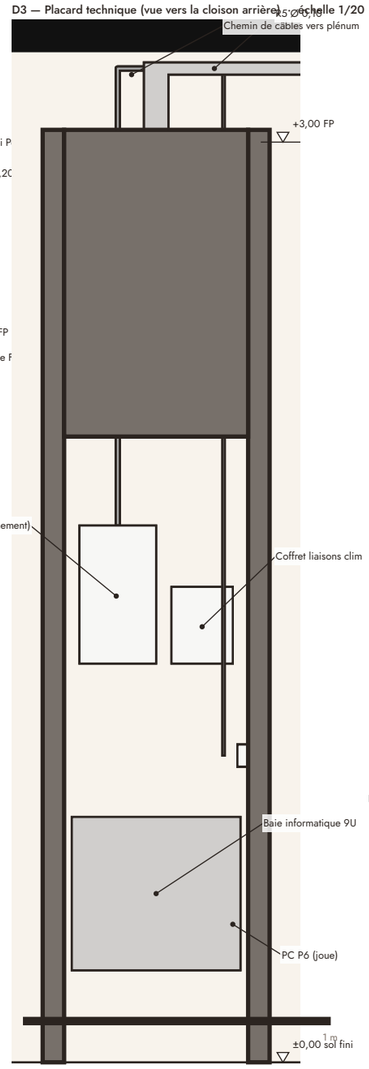


D4 — Fixations non traversantes (oculus / canopée) · échelle 1/10

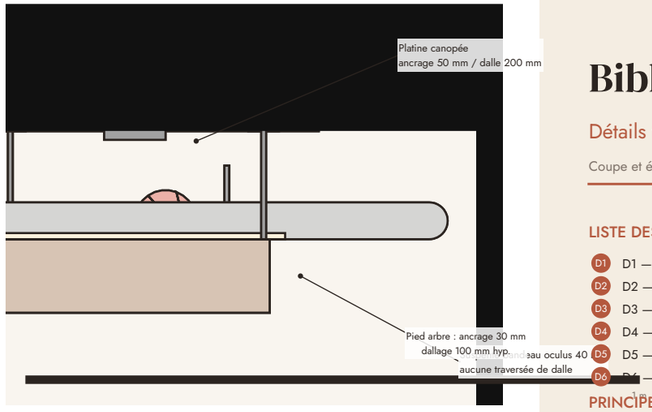


D5 — Seuil de vitrine baie A · échelle 1/10

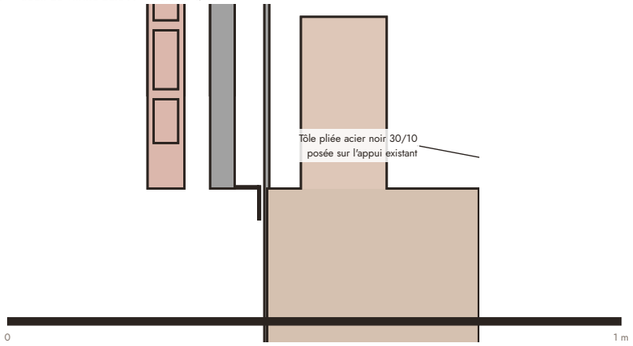

D6 — Panneau passe-liaisons (baie arrière V4) · échelle 1/10

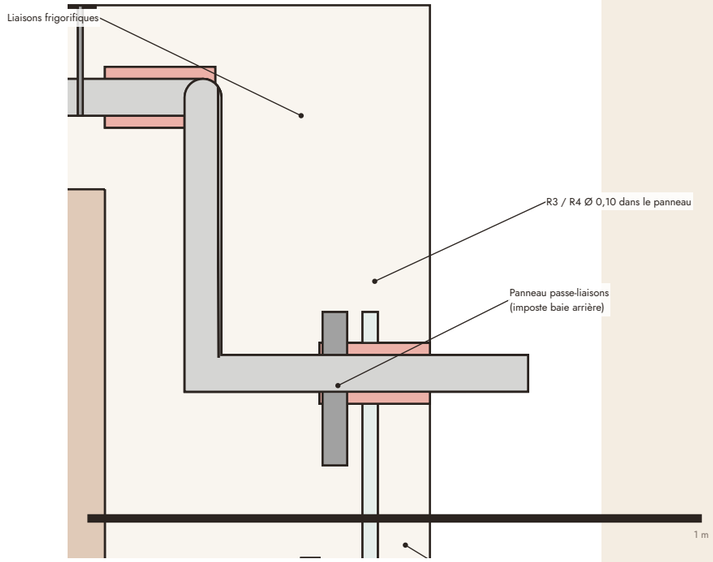

D2 — Coffrage acoustique descente EU/EV 1 · échelle 1/10

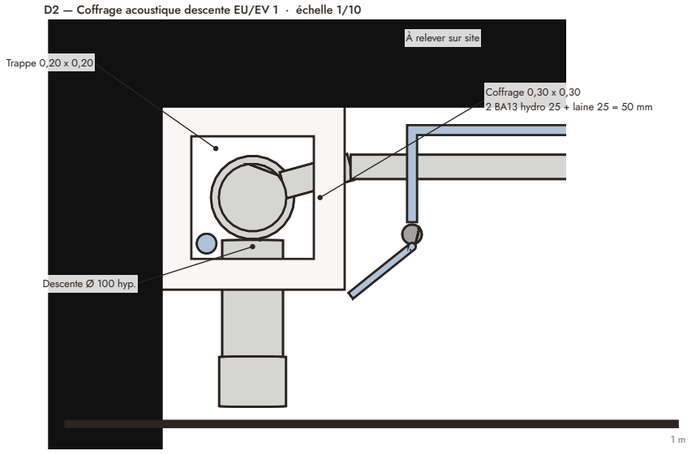

Ouverture V4 inchangée

K&Démi

Bibliothèque Decimo

Détails techniques

Coupe et élévations tirées de l'IFC · Échelles 1/10 et 1/20 (A3)

LISTE DES DÉTAILS

- D1 — Plénum acoustique, chemin C3, suspentes 40 mm
- D2 — Coffrage descente EU/EV 1 (50 mm, trappe)
- D3 — Placard technique (AGCP, clim, 9U, TD)
- D4 — Fixations canopée / oculus / pied arbre (KDEMI_Fixation)
- D5 — Seuil tôle acier baie A
- D6 — Panneau passe-liaisons imposte baie arrière

PRINCIPES

Aucun percement de poteau, voile ni dalle porteuse.
Fixations : chevilles non traversantes, ancrage au plus 1/3 du support (30, 40, 50 mm dans l'IFC).
Valeurs lues sur KDEMI_Fixation (Traversant = False).
Réseaux : voir A09 (électricité), A10 (plomberie).

PROJET	Bibliothèque Decimo — RDC sous logements, Abidjan
PHASE	ESQ V5 — aménagement sur existant V4
PLANCHE	A11 — Détails techniques
ÉCHELLE	1/10 et 1/20 · format A3
MAQUETTE	v5/DECIMO_ESQ_V5.ifc (IFC4) · sha256 88ef6d0a1f…
DATE	Octobre 2026 · indice A

Esquisse : cotes et surfaces indicatives, existant V4 à relever sur site.