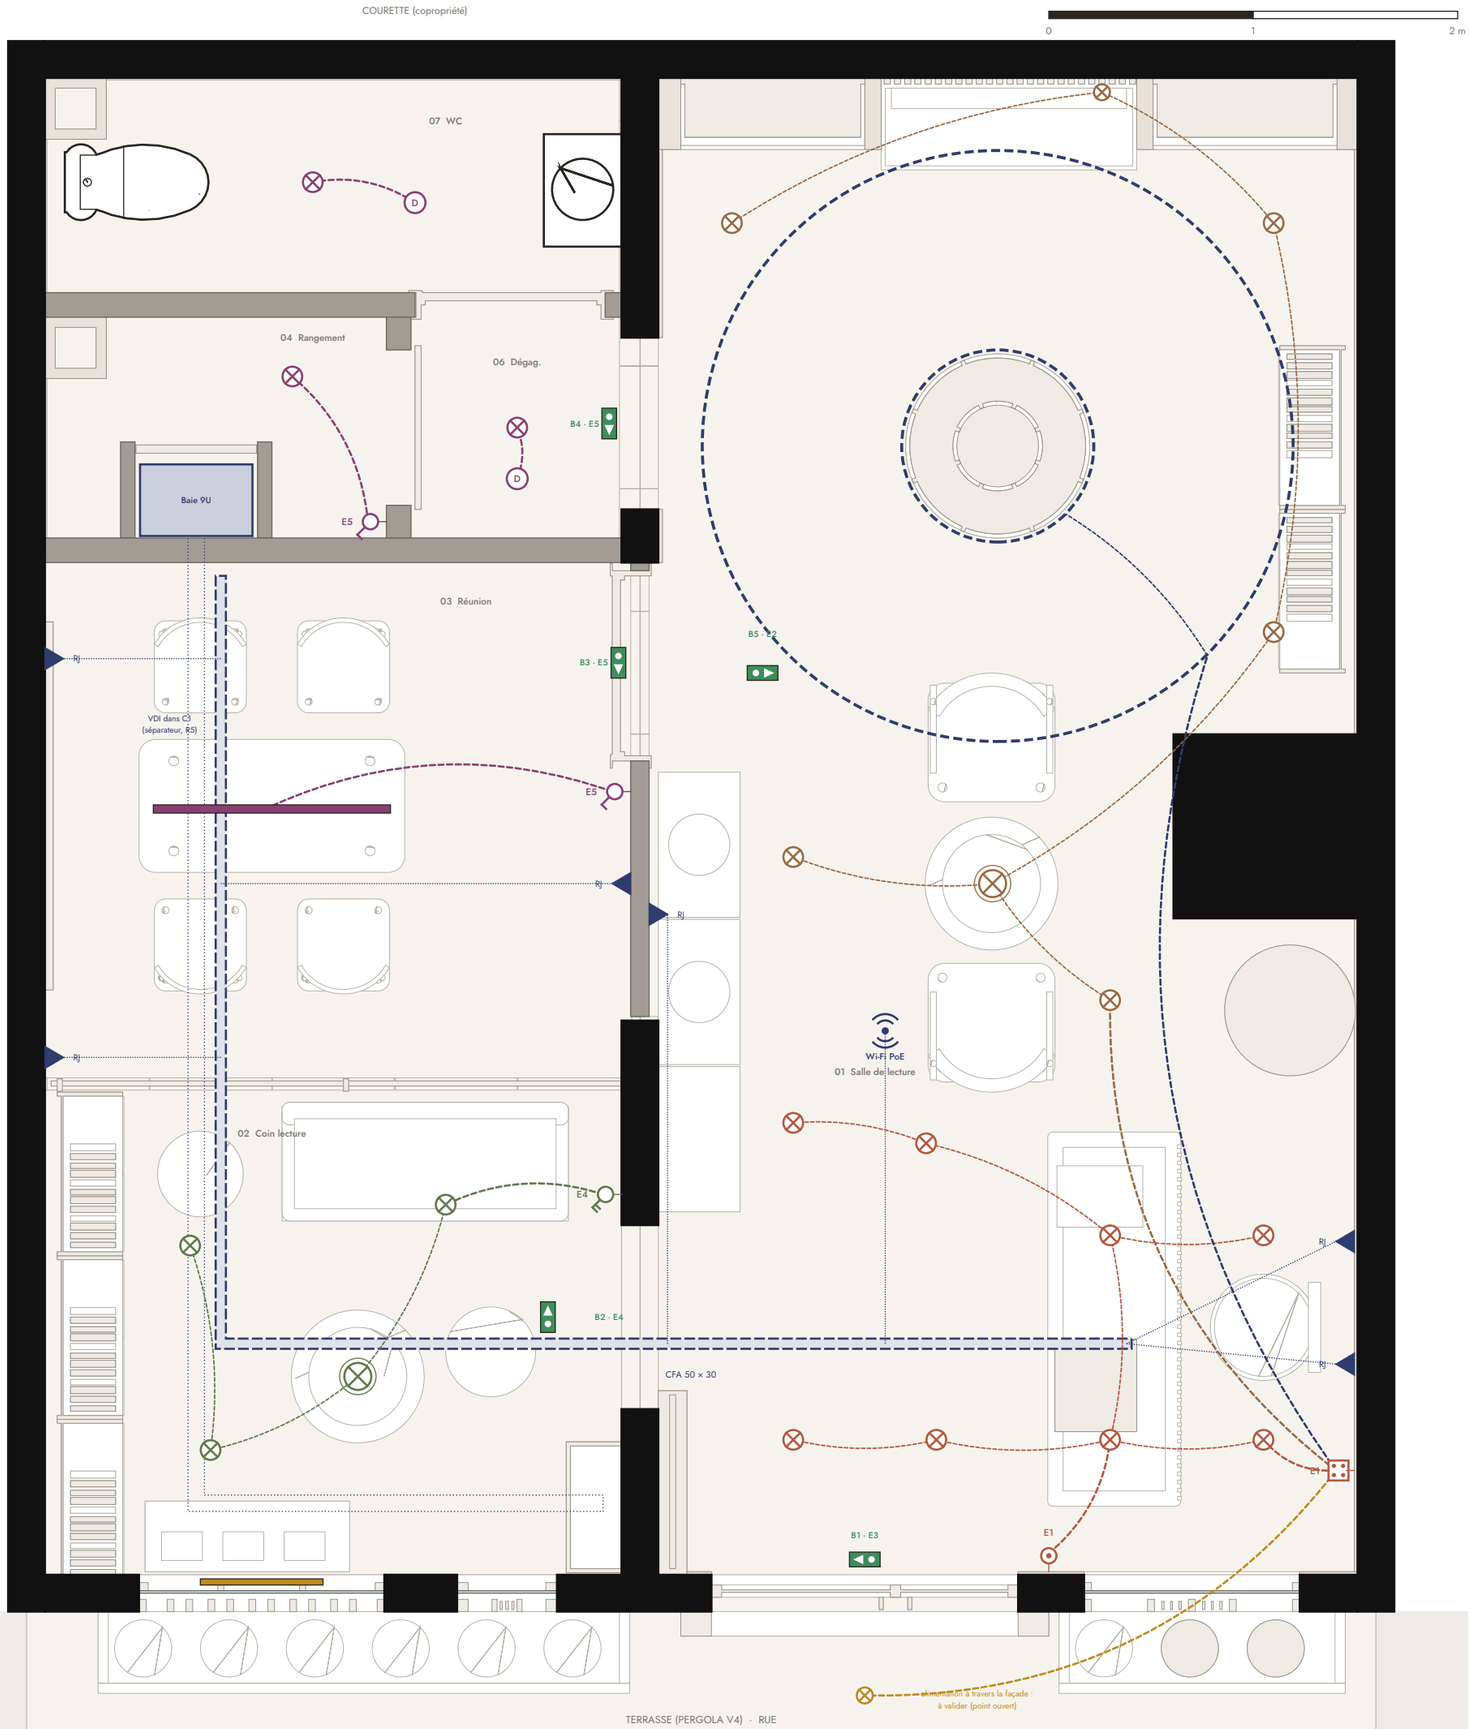


K&Démi

Bibliothèque Decimo

Courants faibles, éclairage et sécurité

Plan de coupe +1,00, plafond superposé · Échelle 1/30 (A3) · 27 luminaires 2700 K de la V5

ÉCLAIRAGE (V5) ET COMMANDES

27 luminaires LED 2700 K de la V5 répartis sur 6 circuits 1,5 mm² / 16 A, 8 points max. (BAES compris) ; les grands volumes sur télérupteurs, l'oculus sur variateur, la vitrine et le seuil sur horloge astronomique. Dégagement et WC sur détecteurs. BAES LED 45 lm, 1 h : un à l'issue (porte d'entrée), un par changement de direction ; raccordés en amont des commandes du circuit d'éclairage du local. Courants faibles : baie 9U du placard, câble U/FTP Cat 6A, chemin CFA 50 × 30 à 5 cm min. du CFO ; borne Wi-Fi 6 en PoE sous le faux-plafond de la salle.

CIRCUITS D'ÉCLAIRAGE (LUS DANS L'IFC)

E1	Éclairage salle de lecture, zone entrée / accueil	8 pts · 56 W
E2	Éclairage salle de lecture, zone fond + BAES 5	8 pts · 55 W
E3	Éclairage oculus et canopée (graduable) + BAES 1	3 pts · 82 W
E4	Éclairage coin lecture + BAES 2	5 pts · 35 W
E5	Éclairage réunion, rangement, dégagement, WC + BAE	6 pts · 49 W
E6	Éclairage vitrine et seuil (spot sous marquise)	2 pts · 14 W

LÉGENDE DES SYMBOLES

- Downlight encastré Ø 90
- Linéaire / réglette LED
- Interrupteur simple / double, axe +1,10
- Platine de commande accueil (4 BP)
- Liaison de commande (couleur du circuit)
- Prise RJ45 double Cat 6A, axe +0,30 / +1,10
- Chemin de câbles courants faibles 50 × 30
- Suspension terre cuite
- Anneau LED (oculus, canopée)
- Bouton-poussoir (télérupteur)
- Détecteur de présence au plafond
- BAES d'évacuation (repère · circuit)
- Borne Wi-Fi au plafond (PoE)
- Câble VDI (tracé de principe)

PROJET	Bibliothèque Decimo — RDC sous logements, Abidjan
PHASE	ESQ V5 — lots techniques sur existant V4
PLANCHE	T02 — Courants faibles, éclairage et sécurité
ÉCHELLE	1/30 · format A3
MAQUETTE	v5/DECIMO_ESQ_V5_tech.ifc (IFC4) · sha256 2a97083fa5…
DATE	Octobre 2026 · indice A

Esquisse : cotes et surfaces indicatives, existant V4 à relever sur site.