

Élévation intérieure Sud — façade vue de l'intérieur (coupe y = 0,80)

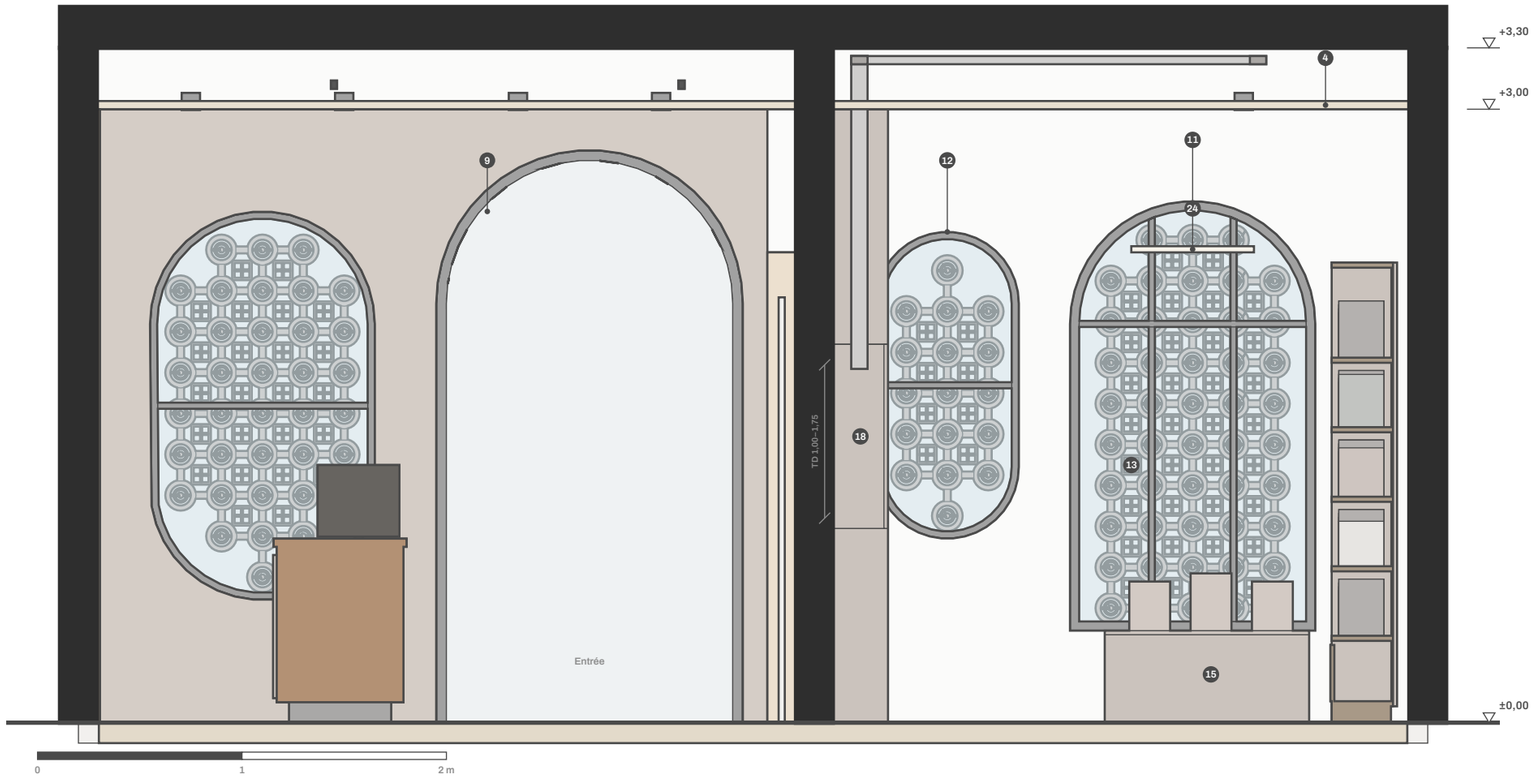

Élévation intérieure Ouest — coin lecture, réunion, rangement, WC (coupe x = 2,85)

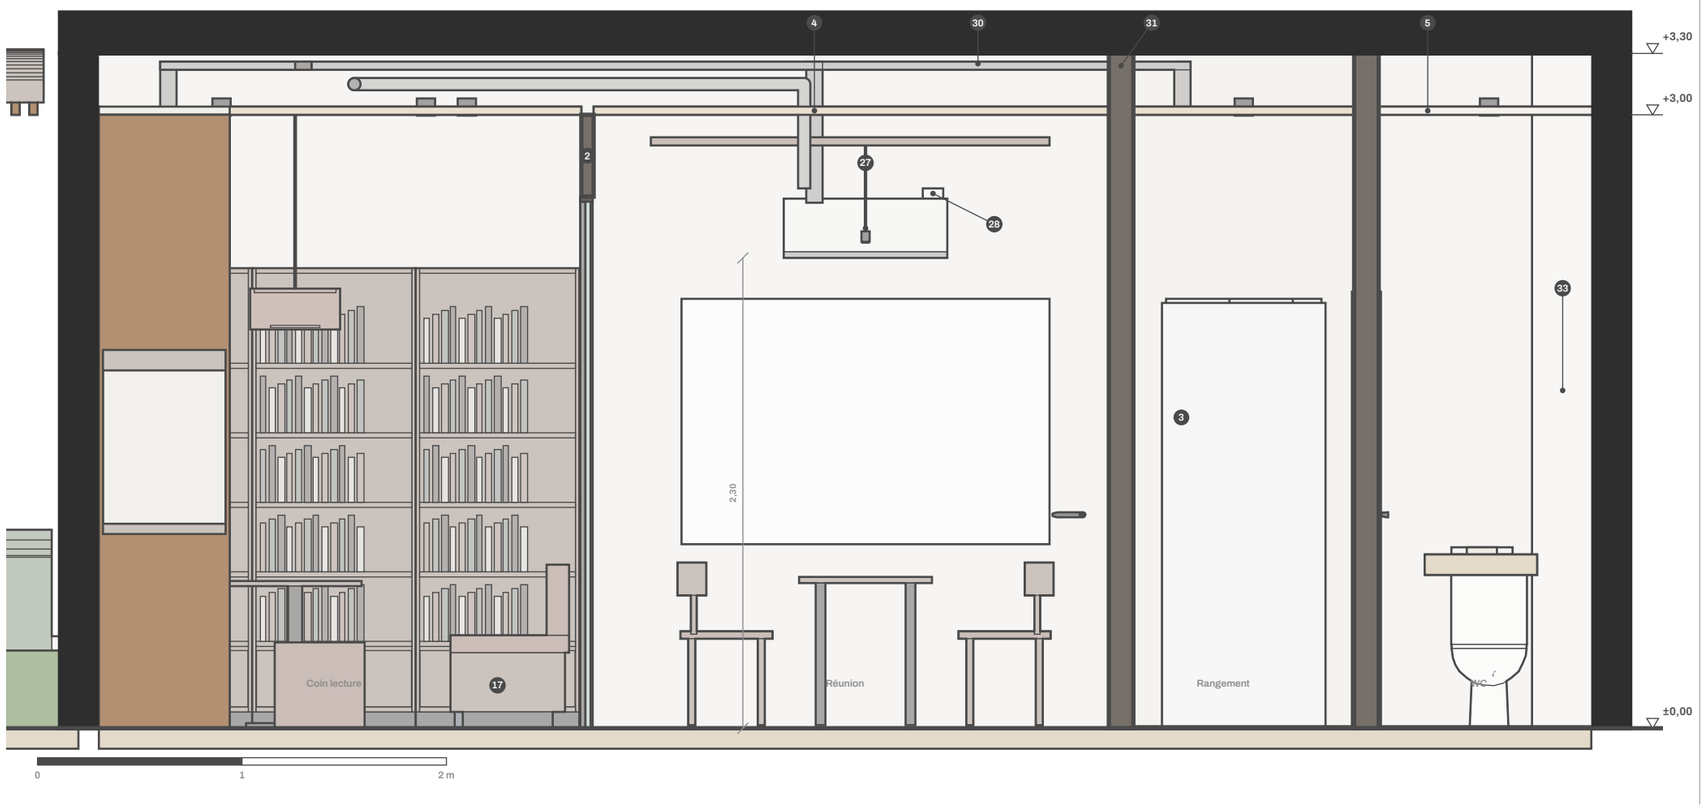

K&Démi

Bibliothèque Decimo

Élévations intérieures Sud et Ouest

Façade intérieure, coin lecture, réunion, locaux de service · Échelle 1/30 (A3)

TECHNIQUE (HYPOTHÈSES ESQ AHOUA)

Tableau divisionnaire ~0,60 × 0,25 encastré dans un habillage iroko près de l'entrée (coin lecture), 1,00 m libre devant, loin de tout point d'eau (rep. 18). Placard technique 0,60 × 0,40 net, porte pleine : arrivée électrique de l'immeuble, baie informatique, coffret des liaisons clim (rep. 3). Split 2 en partie haute du mur mitoyen de la réunion, hors aplomb de la table. Coffrages acoustiques 0,30 × 0,30 des descentes EU/EV (rep. 33) : « À relever sur site ». Pas de TGBT ni de groupe électrogène.

REPÈRES DE L'AMÉNAGEMENT V5

- **2** Cloison légère / retombée BA13 (ajout V5)
- **3** Placard technique 0,60 x 0,40 net
- **4** Faux-plafond acoustique (+3,00, plénum 0,26)
- **5** Faux-plafond hydrofuge WC (+3,00)
- **9** Enduit terre (argile locale) 15 mm
- **11** Vitrine en arche, châssis acier noir
- **12** Châssis fixes acier noir (baies B, C)
- **13** Claustras terre cuite : inserts Adinkrahene et Eban
- **15** Podium de vitrine iroko (h 0,45 = allège baie A)
- **17** Pouf de lecture indigo
- **18** Tableau divisionnaire encastré dans habillage iroko
- **24** Réglette LED de vitrine
- **27** Split mural 9 000 BTU/h (2,6 kW)
- **28** Mini-pompe de relevage des condensats
- **30** Chemin de câbles 80 x 40 en plénum
- **31** Réservation Ø 0,10 (hors structure)
- **33** Coffrage acoustique 0,30 x 0,30 descente EU/EV (à relever)

LÉGENDE

- Existant porteur coupé
- Cloison légère coupée
- Vitrage

PROJET	Bibliothèque Decimo — RDC sous logements, Abidjan
PHASE	ESQ V5 — aménagement sur existant V4
PLANCHE	A06 — Élévations intérieures Sud et Ouest
ÉCHELLE	1/30 · format A3
MAQUETTE	v5/DECIMO_ESQ_V5.ifc (IFC4) · sha256 985f48d48b…
DATE	Octobre 2026 · indice A

Esquisse : cotes et surfaces indicatives, existant V4 à relever sur site.