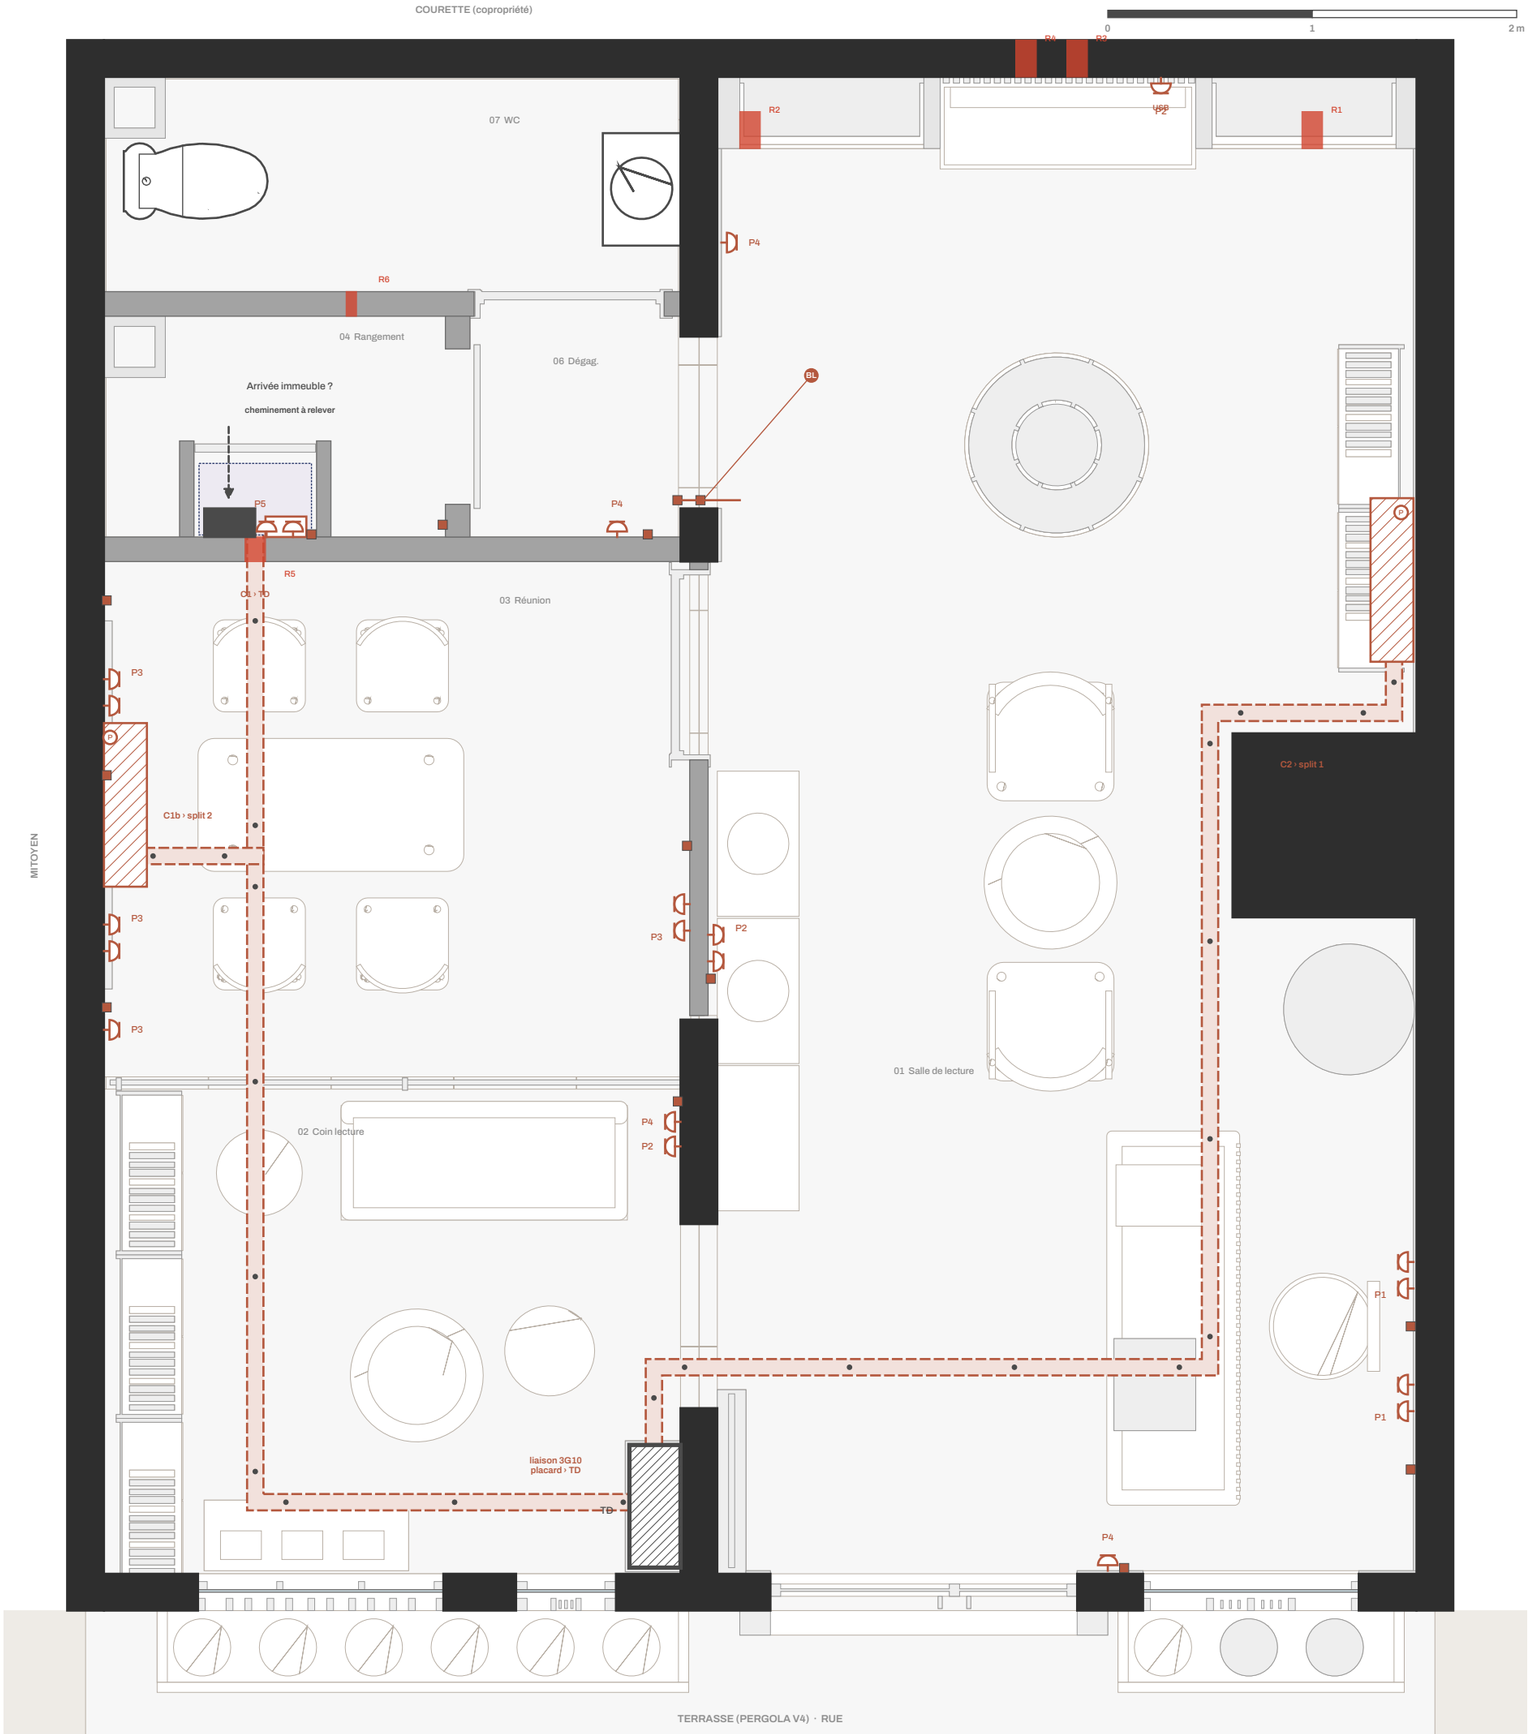


K&Démi

Bibliothèque Decimo

Électricité — courants forts

Plan de coupe +1,00, réseaux en plénum superposés · Échelle 1/30 (A3) · NF C 15-100

PRINCIPES

Tableau divisionnaire V5 (rep. TD) alimenté par le coffret d'arrivée du placard technique (disjoncteur de branchement de l'immeuble), liaison 3G10 dans C1.
Cheminement de l'arrivée immeuble › placard inconnu : à relever (point ouvert).
Câbles U1000 R2V en plénum sur chemins 80 × 40 (C1, C1b, C2), suspentes M8 à cheville courte non traversante ; descentes en goulotte 40 × 20 collée ou derrière le lambris / doublage : aucune saignée dans les porteurs.
Appareillage en saillie, axe +0,30 (prises) et +1,10 (commandes).
BL : traversée de la baie libre V4 sous le linteau (goulotte collée, h 2,08).
R6 : fourreau Ø 50 en plénum dans la cloison placo V4 4350620 (non porteuse), à valider comme R5 ; sinon goulotte franchissant l'huisserie du WC.

CIRCUITS PRISES ET SPÉCIALISÉS (LUS DANS L'IFC)

P1	PC accueil (poste agent, imprimante, caisse)	4 socles · 20 A · 2,5 mm²
P2	PC postes de lecture et d'écoute	4 socles · 20 A · 2,5 mm²
P3	PC salle de réunion (écran, portables)	7 socles · 20 A · 2,5 mm²
P4	PC ménage (entrée, coin lecture, fond, dégagement)	4 socles · 20 A · 2,5 mm²
P5	PC baie informatique (onduleur, box, switch PoE)	2 socles · 16 A · 2,5 mm²
C1	Split 1 salle de lecture + mini-pompe 1	1 split + pompe · 16 A · 2,5 mm²
C2	Split 2 salle de réunion + mini-pompe 2	1 split + pompe · 16 A · 2,5 mm²

LÉGENDE DES SYMBOLES

- Prise 16 A 2P+T en saillie (repère de circuit)
- Prise 16 A 2P+T double
- Prise 16 A + USB intégrée au mobilier
- Tableau divisionnaire (V5)
- Coffret arrivée immeuble (placard technique)
- Chemin de câbles CFO 80 × 40 en plénum
- Suspente M8, cheville courte non traversante
- Descente en goulotte 40 × 20 (collée, sans saignée)
- Split 9 000 BTU/h (circuit spécialisé C1, C2)
- Mini-pompe de relevage des condensats (sur C1, C2)
- Réservation / fourreau hors structure (R5, R6)

PROJET	Bibliothèque Decimo — RDC sous logements, Abidjan
PHASE	ESQ V5 — lots techniques sur existant V4
PLANCHE	T01 — Électricité — courants forts
ÉCHELLE	1/30 · format A3
MAQUETTE	v5/DECIMO_ESQ_V5_tech.ifc (IFC4) · sha256 2a97083fa5…
DATE	Octobre 2026 · indice A

Esquisse : cotes et surfaces indicatives, existant V4 à relever sur site.