Identité K&Démi

Logo revu, palette, typographies, grille

LOGO K&DÉMI v3 · L'ARCHE DANS LE CARRÉ, MOT-SYMBOLE MANROPE

Version principale : encre sur blanc chaux, & terre cuite. Fichiers SVG et PNG transparents.

Inversée, fond encre

Une couleur (encre)

Icône d'app et favicons 32 / 16 px

TAILLE MINIMALE

Logo complet : 30 mm en impression, 120 px à l'écran.

25 mm : pied de page seulement, jamais moins.

RÈGLE D'USAGE

Le nom K&Démi est toujours posé à côté du symbole. Le symbole seul est réservé à l'icône d'app et au favicon.

Zone de protection : la moitié de la hauteur du carré tout autour. Pas de déformation, pas d'ombre, pas de dégradé.

PALETTE AGENCE

Encre	Terre cuite	Iroko	Sable
#2B2420 · texte, traits	#B4583E · signature	#9A6B43 · bois, repères	#E6D6BF · aplats

Sable clair	Blanc chaux	Taupe	Olive
#F4EDE2 · fonds	#FBF8F3 · page	#7D7168 · texte 2	#5F7A4B · végétal, rare

TYPOGRAPHIES (LIBRES, GOOGLE FONTS, OFL)

DM Serif Display

Titres, logo, chiffres clés · corps 18 à 36 pt

Jost Regular / Medium

Texte 8 à 10 pt, légendes 7 pt, capitales espacées +12 %


GRILLE A3 PAYSAGE

12 colonnes · marges 15 mm · gouttière 5 mm · bandeau titre 17 mm · pied 6 mm

Bibliothèque Decimo

Page type du dossier : plan du rez-de-chaussée, esquisse V4, échelle 1/50

K&Démi

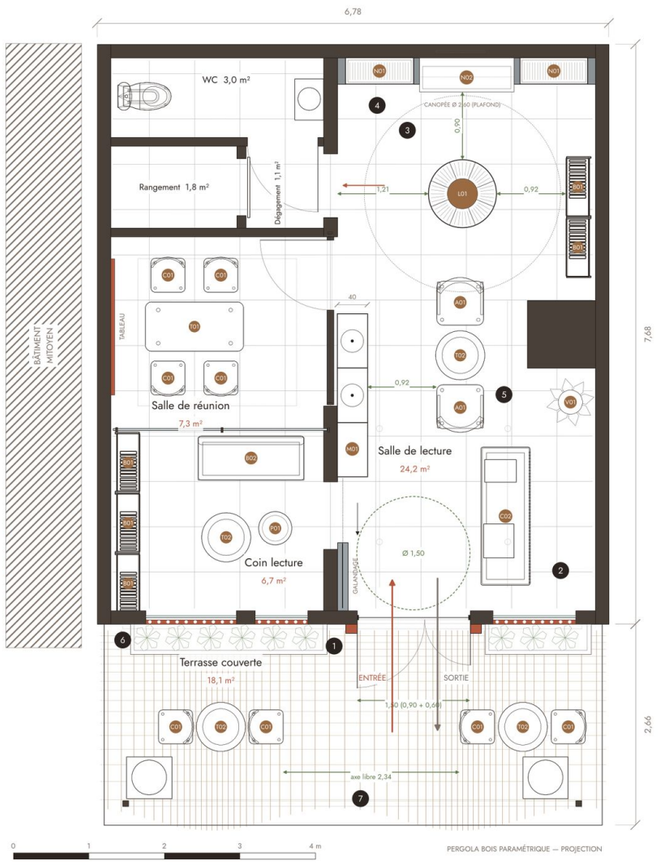

Bibliothèque Decimo

Proposition d'aménagement V4 — arbre à livres et façade cintrée

Plan du rez-de-chaussée · Esquisse V4 (sur base V3) · Échelle 1/50 (A3) · Coupe à +1,10 m

PRINCIPES D'AMÉNAGEMENT

1. Entrée principale cintrée dans un portail terre cuite : double porte vitrée 0,90 + 0,60, ouvrant vers l'extérieur, seuil plat, sans intérieur Ø 1,50
2. Accueil : le comptoir fait face au flux d'entrée ; poste agent dos à la baie à claustra (C)
3. Arbre à livres au fond, Ø 0,90 sous une canopée Ø 2,60 ; tour complet en 0,90 minimum
4. Mur du fond en 3 niches cintrées : 2 bibliothèques et 1 banquette de lecture (fond en lames bois)
5. Salon de lecture recentré entre console M01 et pilier ; passage principal 0,92 côté ouest
6. Façade : baies cintrées à claustra terre cuite (A, B coin lecture ; C accueil) et jardinières
7. Terrasse : groupe de tables est décalé de 1 m pour dégager un axe d'entrée de 2,34 m

CONTRÔLE ERGONOMIQUE

Critère	Cible	Proposé
Passage principal	min. 0,90	0,92
Tour de l'arbre à livres	min. 0,90	0,90 à 1,21
Entrée (2 UP)	min. 1,40	1,50
Vantail principal	min. 0,90	0,90
Aire de manœuvre derrière l'entrée	Ø 1,50	Ø 1,50
Hauteur libre sous canopée	min. 2,20	2,40
Axe libre en terrasse	min. 1,40	2,34

Cotes en mètres, mesurées au nu des éléments finis.

MOBILIER

AD1	Fauteuil	× 2
SO1	Rayonnage 800	× 5
NO2	Banquette	× 1
CO1	Chaise courbe	× 8
CV2	Comptoir d'accueil	× 1
LD1	Arbre à livres (Ø 0,90, canopée)	× 1
MO1	Console vinyles (40 cm)	× 1
NO1	Niche cintrée bibliothèque	× 2
NO2	Niche cintrée banquette	× 1
PO1	Pouf	× 1
TD1	Table de réunion 1300	× 1
TD2	Table ronde	× 4
VO1	Plante en pot	× 1

LÉGENDE

- Maçonnerie / cloison (coupée)
- Doublage cintré des niches
- Claustra terre cuite / portail
- Vitrage
- Lames bois (pergola)
- Au-dessus du plan de coupe
- Cote de passage / dégagement
- Bâtiment mitoyen

CHOIX INTÉGRÉS À LA MAQUETTE V4

- Le mur du fond passe du claustra V3 aux niches cintrées (lames bois en fond de niche)
- Le bureau du fond et ses 3 chaises sont remplacés par la banquette de la niche centrale
- 2 rayonnages supprimés (zone agent, niche est), compensés par les niches et l'arbre à livres
- L'ancienne porte du coin lecture devient une baie à claustra (accès par la salle de lecture)

Maquette : DECIMO_ESQ_V4.ifc (niveau N00 _ RDC) — proposition V4 reportée, matériaux et textures K&Démi appliqués.

Document d'esquisse — dimensions et surfaces indicatives, à vérifier sur site.

K&Démi · PLAN RDC — ESQ V4 · Octobre 2026

PRINCIPES

1. Un seul seuil cintré, centré sur la rue, cadre l'arbre à livres.
2. Trois baies en claustra terre cuite filtrent le soleil de l'après-midi.
3. La canopée terre cuite de l'arbre est le seul objet fort de la salle.
4. Bois iroko pour tout ce qui se touche, chaux pour tout ce qui se voit.
5. Ventilation traversante : claustra + pergola, pas de baie fermée au sud.

SURFACES (IFC V4)

Salle de lecture	24,2 m²
Salle de réunion	7,3 m²
Coin lecture	6,7 m²
WC	3,0 m²
Rangement	1,8 m²
Terrasse couverte	18,1 m²

PROJET	Bibliothèque Decimo, Abidjan
PHASE	Esquisse V4
ÉCHELLE	1/50 en A3
DATE	Octobre 2026
AGENCE	K&Démi, architecture · intérieur

D.A de la bibliothèque


Terre, ombre et bois : une salle de lecture fraîche sous le soleil d'Abidjan




Devanture : local en pied d'immeuble, portail terre cuite, vitrine, claustra



RDC : vue depuis l'entrée vers l'arbre à livres

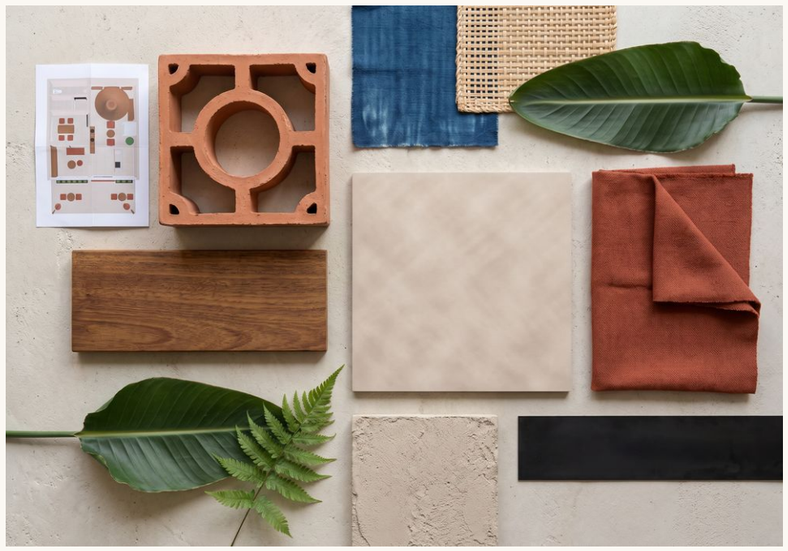

Maquette matière sur le plan V4

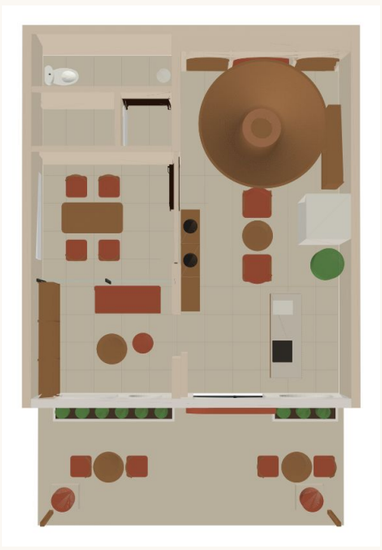


Plan RDC issu de l'IFC V4 (local commercial, logements au-dessus)

MATÉRIAUX



PALETTE INTÉRIEURE

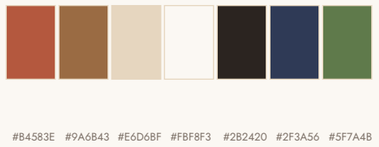

AMBIANCE

Pénombre fraîche, lumière tamisée
par la claustra, 2700 K le soir
Aucun dégradé, aucun motif plaqué

MOBILIER

Iroko sur mesure, chaises courbes
assises raphia, laine terre cuite
coussins indigo artisanaux

LUMINAIRES

Rails noirs + spots IRC 90
anneau LED sous canopée
suspensions papier, appliques IP65

VÉGÉTAL

Ficus lyrata, Strelitzia
fougères, Dracaena
bougainvillier sur pergola