
K&Démi
ARCHITECTURE · INTÉRIEUR

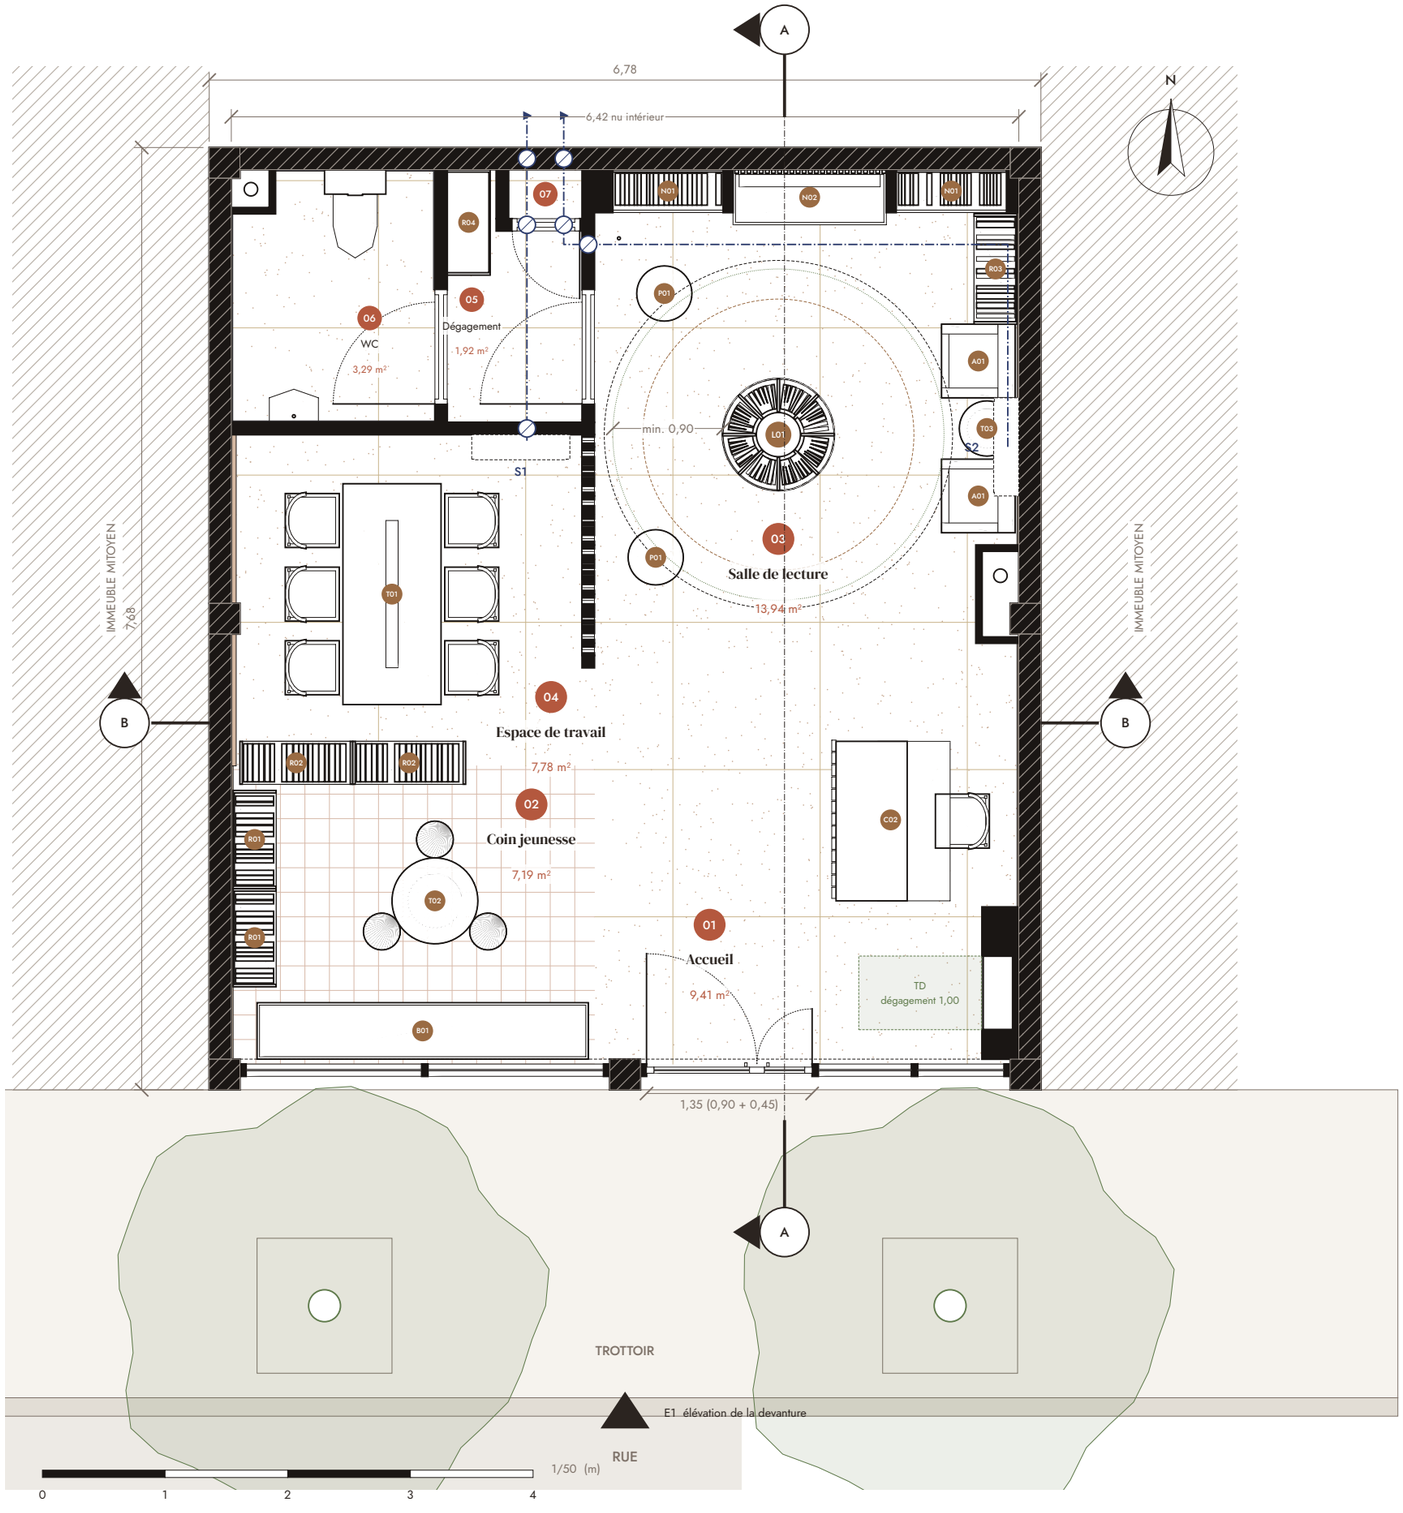

Bibliothèque Decimo

Plan du rez-de-chaussée

Esquisse V5 · Échelle 1/50 (A3) · Plan de coupe à +1,00

Local RDC d'un immeuble existant (logements aux étages) — un seul niveau, sans escalier ni toiture

Dessin généré par script depuis la maquette IFC4 (sections exactes des maillages)

ESPACES — SURFACES NETTES (Qto_SpaceBaseQuantities)

N°	Espace	Surface
01	Accueil — entrée	9,41 m²
02	Coin jeunesse — vitrine	7,19 m²
03	Salle de lecture — arbre à livres	13,94 m²
04	Espace de travail — tables de lecture	7,78 m²
05	Dégagement — réserve	1,92 m²
06	WC	3,29 m²
07	Placard technique	0,24 m²
	Total surfaces nettes	**43,77 m²**

LÉGENDE

- Existant porteur — ne pas toucher (voiles, poteaux, poutre)
- Élément coupé neuf : cloison, doublage, coffrage, claustra
- Mobilier en silhouette (repère iroko, cf. nomenclature IFC)
- Au-dessus du plan de coupe : poutre, coupole Ø 2,80, splits
- Liaisons frigorifiques (plénum) ; réservation Ø 100 (cercle)
- Dégagements : 1,00 devant TD, 0,90 autour de l'arbre
- Terrazzo à joints laiton / tomettes 20 × 20

TECHNIQUE RÉSERVÉE (hypothèses ESQ Ahoua)

- Placard technique 0,60 × 0,40 net, porte pleine : arrivée élec., baie 9U, liaisons clim
- TD encastré 0,60 × 0,25 près de l'entrée, 1,00 m dégagé, loin des points d'eau
- 2 splits muraux ~9 000 BTU (S1, S2) en hauteur sur murs pleins, hors aplomb des tables
- Liaisons en plénum vers la façade arrière / courette (jamais en toiture), Ø 100
- 2 descentes EU/EV des logements en coffrages acoustiques (BA13 ×2 + LM 45)
- Pas de local TGBT ni de groupe électrogène

Document d'esquisse — dimensions et surfaces indicatives, à vérifier sur site.

PROJET	Bibliothèque Decimo — local RDC, immeuble existant, Abidjan
PHASE	Esquisse (ESQ) · indice V5 · 14/10/2026
MAQUETTE	v5/DECIMO_ESQ_V5.ifc (IFC4, mm)
ÉQUIPE	D.A. Affoué / Stéphanie · technique : hypothèses ESQ Ahoua

PLANCHE 01