K&Démi
ARCHITECTURE · INTÉRIEUR


Bibliothèque Decimo

Coupe AA — longitudinale

Esquisse V5 · Échelle 1/50 (A3) · Regard vers l'ouest, plan de coupe x = 4,60

Coupe à travers la porte d'entrée, l'arbre à livres, la coupole et la niche banquette

Dessin généré par script depuis la maquette IFC4

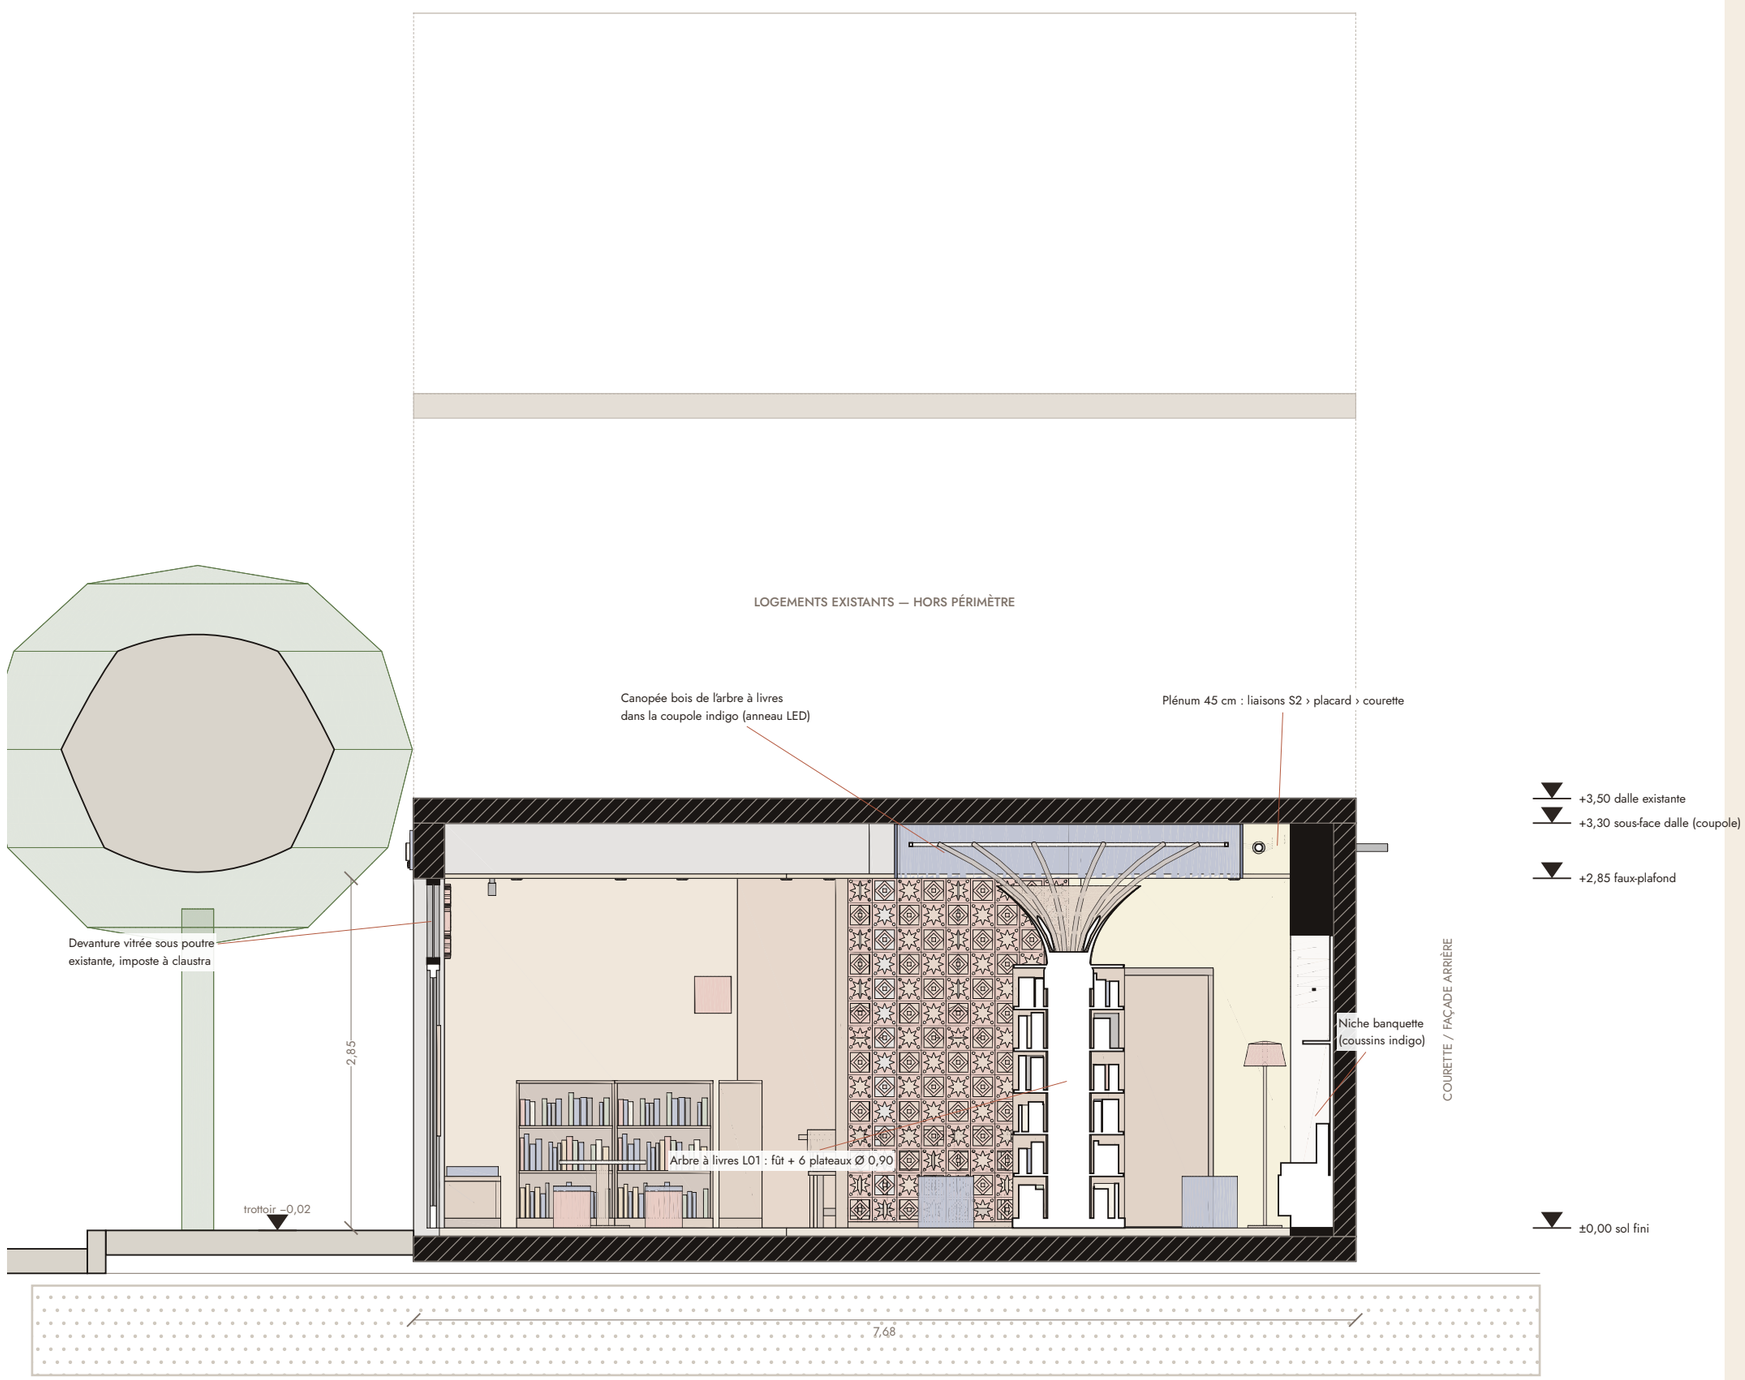

PRINCIPES

Un seul niveau : sol fini ±0,00, dalle haute existante conservée (logements au-dessus).

Faux-plafond acoustique en fibres de bois à +2,85 ; plénum de 45 cm pour les réseaux.

Au-dessus de l'arbre, le plafond s'ouvre en coupole Ø 2,80 jusqu'à la dalle (+3,30),

peinte indigo : la canopée bois s'y épanouit, éclairée par un anneau LED 2700 K.

Devanture : menuiserie acier encre sous la poutre existante, imposte en claustra

terre cuite Adinkra ; porte 0,90 + 0,45 ouvrant vers l'intérieur, seuil plat.

Descentes EU/EV des logements gardées en place, en coffrages acoustiques.

LÉGENDE

- Existant porteur coupé (dalle, poutre, voiles)
- Élément neuf coupé
- Mobilier coupé en silhouette
- Vu au-delà du plan de coupe (traits fins)

Document d'esquisse — dimensions et surfaces indicatives, à vérifier sur site.

PROJET	Bibliothèque Decimo — local RDC, immeuble existant, Abidjan
PHASE	Esquisse (ESQ) · indice V5 · 14/10/2026
MAQUETTE	v5/DECIMO_ESQ_V5.ifc (IFC4, mm)
ÉQUIPE	D.A. Affoué / Stéphanie · technique : hypothèses ESQ Ahoua

PLANCHE 02