K&Démi
ARCHITECTURE · INTÉRIEUR


Bibliothèque Decimo

Élévation de la devanture sur rue

Esquisse V5 · Échelle 1/50 (A3) · Façade sud, vue depuis la rue

Devanture dans la baie existante (poteaux P1-P2-P3, poutre PT1) ; immeuble au-dessus en contexte

Dessin généré par script depuis la maquette IFC4 (arbres d'alignement en transparence)

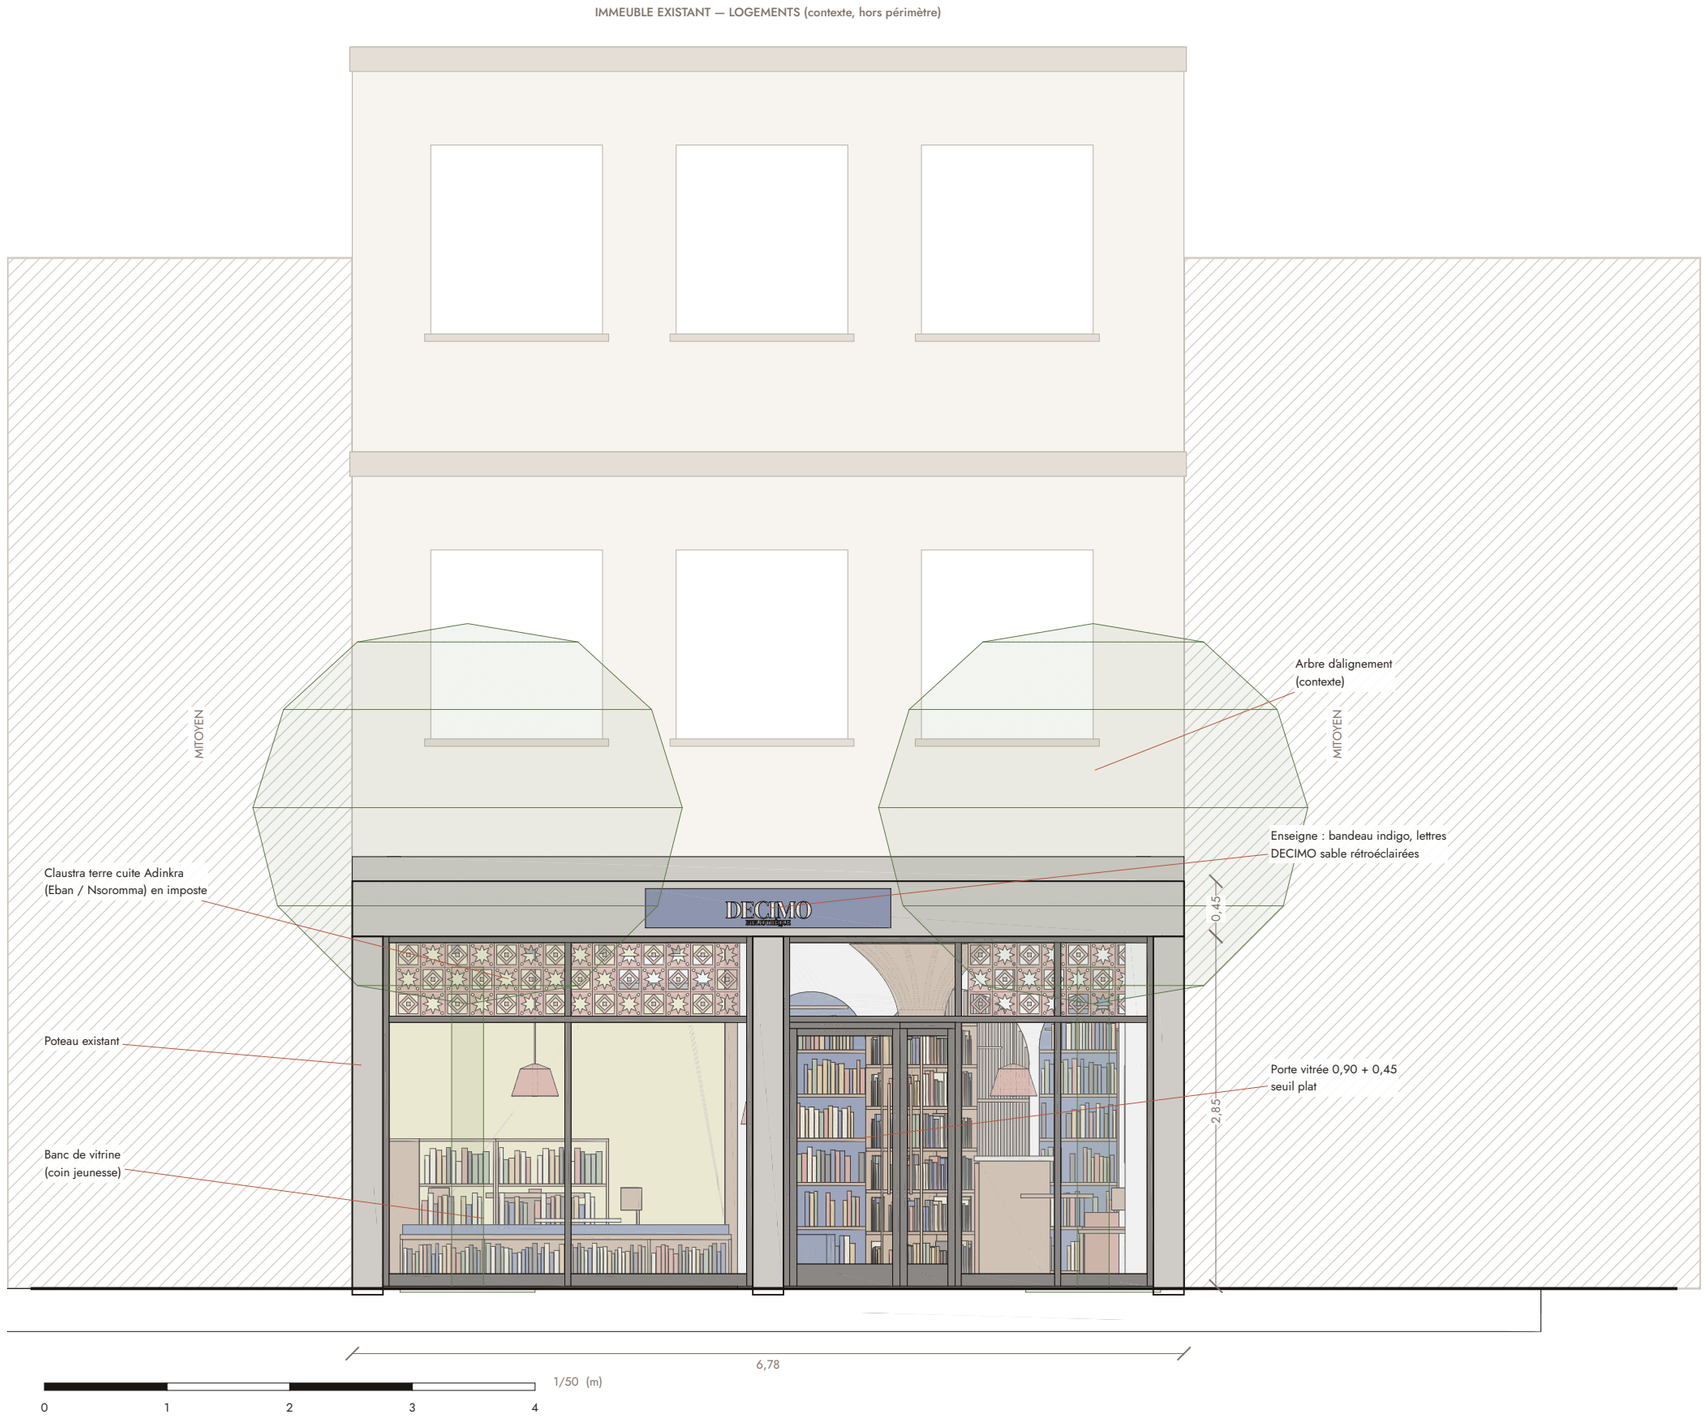

DEVANTURE — PRINCIPES

Pas de façade cintrée : la devanture reste dans la baie existante, sous la poutre.

Menuiserie acier thermolaqué encre, vitrages feuilletés, soubassement de 10 cm.

Imposte : claustra en modules terre cuite 20 × 20 à motifs Adinkra

« Eban » (la clôture) et « Nsoromma » (l'étoile) ; Gye Nyame exclu.

À l'ouest, banc de vitrine en iroko (coin jeunesse) ; à l'est, accueil.

Enseigne sur la poutre : seule touche indigo de la façade.

Fixations sur la structure existante légères, à valider (syndic, BET).

MODULES DE CLAUSTRA (20 × 20 cm)

Alternance en damier des deux modules :

— Eban : carré, losange et cœur plein

— Nsoromma : étoile à 8 branches évidée

Terre cuite, ép. 8 à 10 cm, pose collée

Même module pour le claustra intérieur

Document d'esquisse — dimensions et surfaces indicatives, à vérifier sur site.

PROJET	Bibliothèque Decimo — local RDC, immeuble existant, Abidjan
PHASE	Esquisse (ESQ) · indice V5 · 14/10/2026
MAQUETTE	v5/DECIMO_ESQ_V5.ifc (IFC4, mm)
ÉQUIPE	D.A. Affoué / Stéphanie · technique : hypothèses ESQ Ahoua

PLANCHE 03