
K&Démi
ARCHITECTURE · INTÉRIEUR

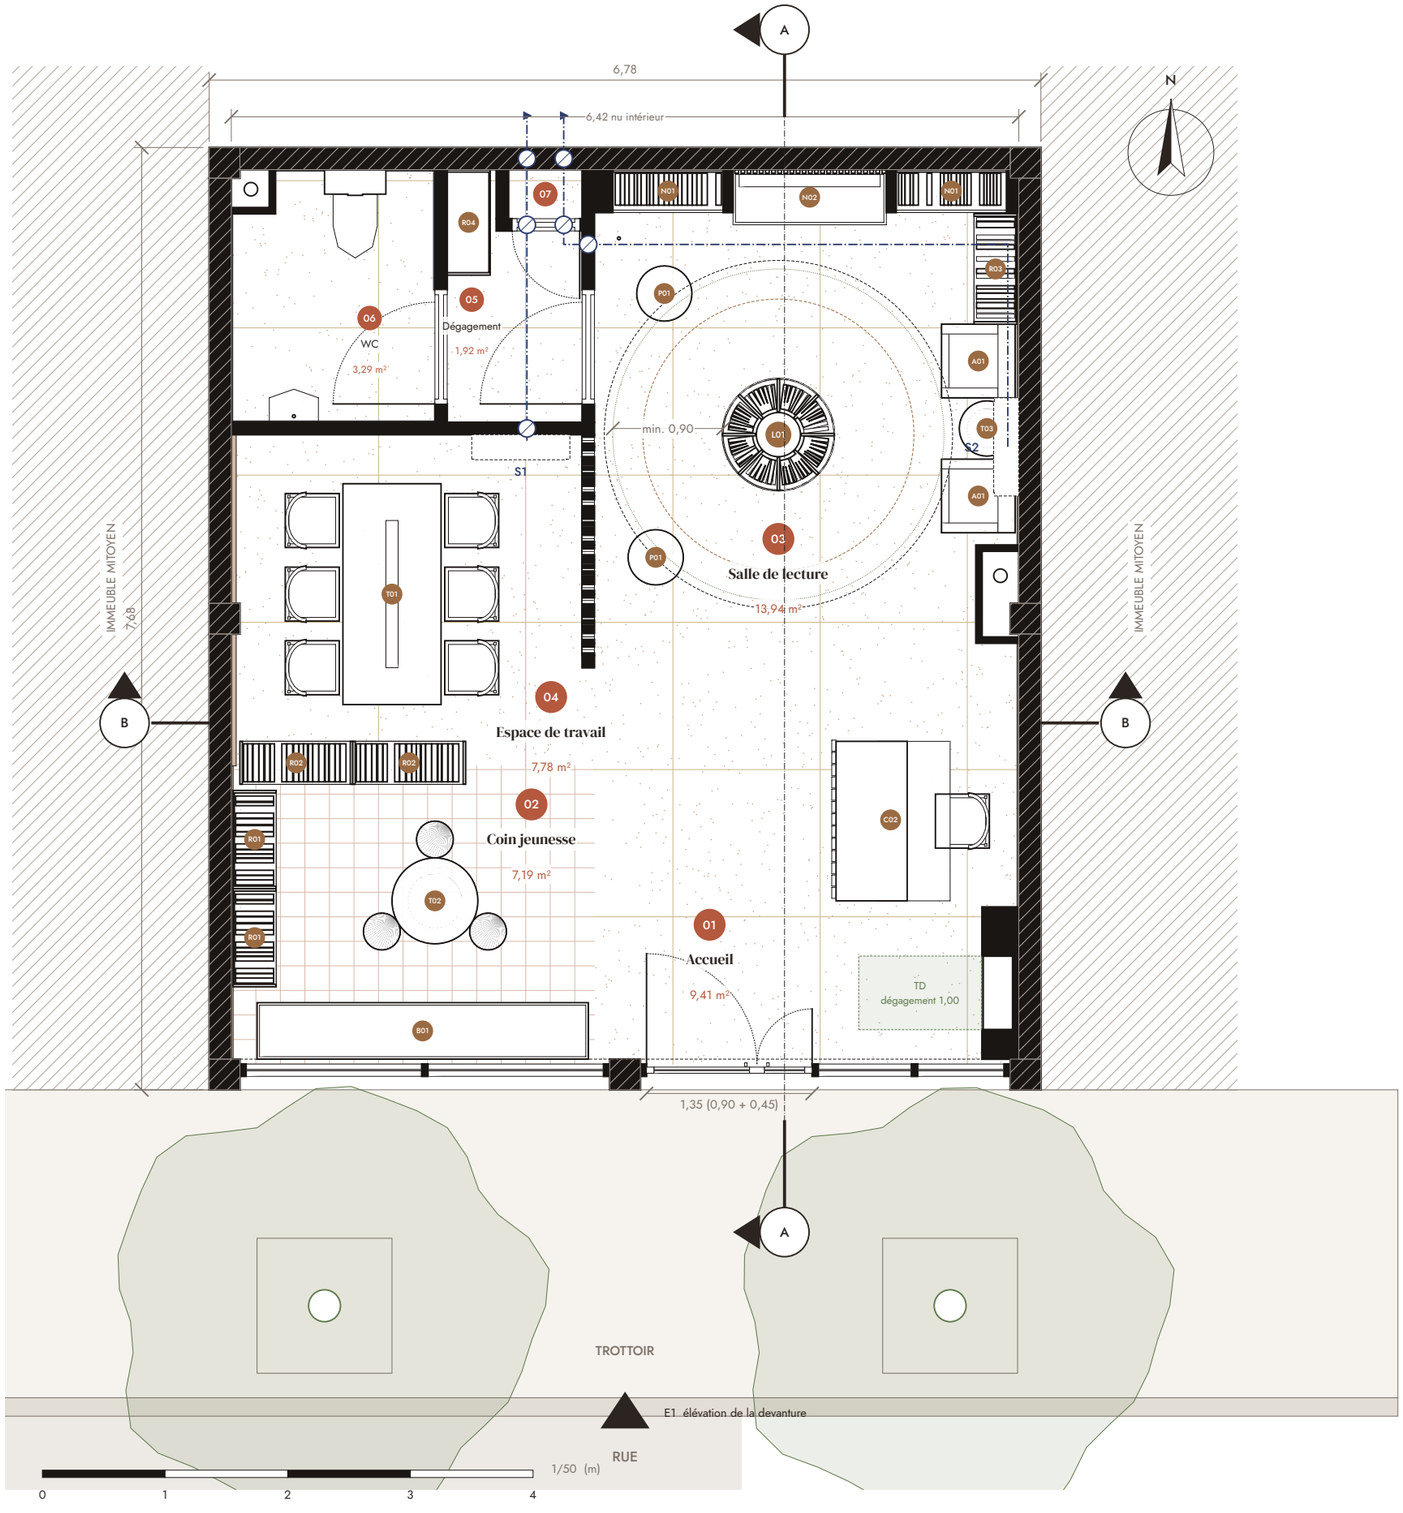

Bibliothèque Decimo

Plan du rez-de-chaussée

Esquisse V5 · Échelle 1/50 (A3) · Plan de coupe à +1,00

Local RDC d'un immeuble existant (logements aux étages) — un seul niveau, sans escalier ni toiture

Dessin généré par script depuis la maquette IFC4 (sections exactes des maillages)

ESPACES — SURFACES NETTES (Qto_SpaceBaseQuantities)

N°	Espace	Surface
01	Accueil — entrée	9,41 m²
02	Coin jeunesse — vitrine	7,19 m²
03	Salle de lecture — arbre à livres	13,94 m²
04	Espace de travail — tables de lecture	7,78 m²
05	Dégagement — réserve	1,92 m²
06	WC	3,29 m²
07	Placard technique	0,24 m²
	Total surfaces nettes	**43,77 m²**

LÉGENDE

- Existant porteur — ne pas toucher (voiles, poteaux, poutre)
- Élément coupé neuf : cloison, doublage, coffrage, claustra
- Mobilier en silhouette (repère iroko, cf. nomenclature IFC)
- Au-dessus du plan de coupe : poutre, coupole Ø 2,80, splits
- Liaisons frigorifiques (plénum) ; réservation Ø 100 (cercle)
- Dégagements : 1,00 devant TD, 0,90 autour de l'arbre
- Terrazzo à joints laiton / tomettes 20 × 20

TECHNIQUE RÉSERVÉE (hypothèses ESQ Ahoua)

- Placard technique 0,60 × 0,40 net, porte pleine : arrivée élec., baie 9U, liaisons clim
- TD encastré 0,60 × 0,25 près de l'entrée, 1,00 m dégagé, loin des points d'eau
- 2 splits muraux ~9 000 BTU (S1, S2) en hauteur sur murs pleins, hors aplomb des tables
- Liaisons en plénum vers la façade arrière / courette (jamais en toiture), Ø 100
- 2 descentes EU/EV des logements en coffrages acoustiques (BA13 ×2 + LM 45)
- Pas de local TGBT ni de groupe électrogène

Document d'esquisse — dimensions et surfaces indicatives, à vérifier sur site.

PROJET	Bibliothèque Decimo — local RDC, immeuble existant, Abidjan
PHASE	Esquisse (ESQ) · indice V5 · 14/10/2026
MAQUETTE	v5/DECIMO_ESQ_V5.ifc (IFC4, mm)
ÉQUIPE	D.A. Affoué / Stéphanie · technique : hypothèses ESQ Ahoua

PLANCHE 01

K&Démi
ARCHITECTURE · INTÉRIEUR


Bibliothèque Decimo

Coupe AA — longitudinale

Esquisse V5 · Échelle 1/50 (A3) · Regard vers l'ouest, plan de coupe x = 4,60

Coupe à travers la porte d'entrée, l'arbre à livres, la coupole et la niche banquette

Dessin généré par script depuis la maquette IFC4

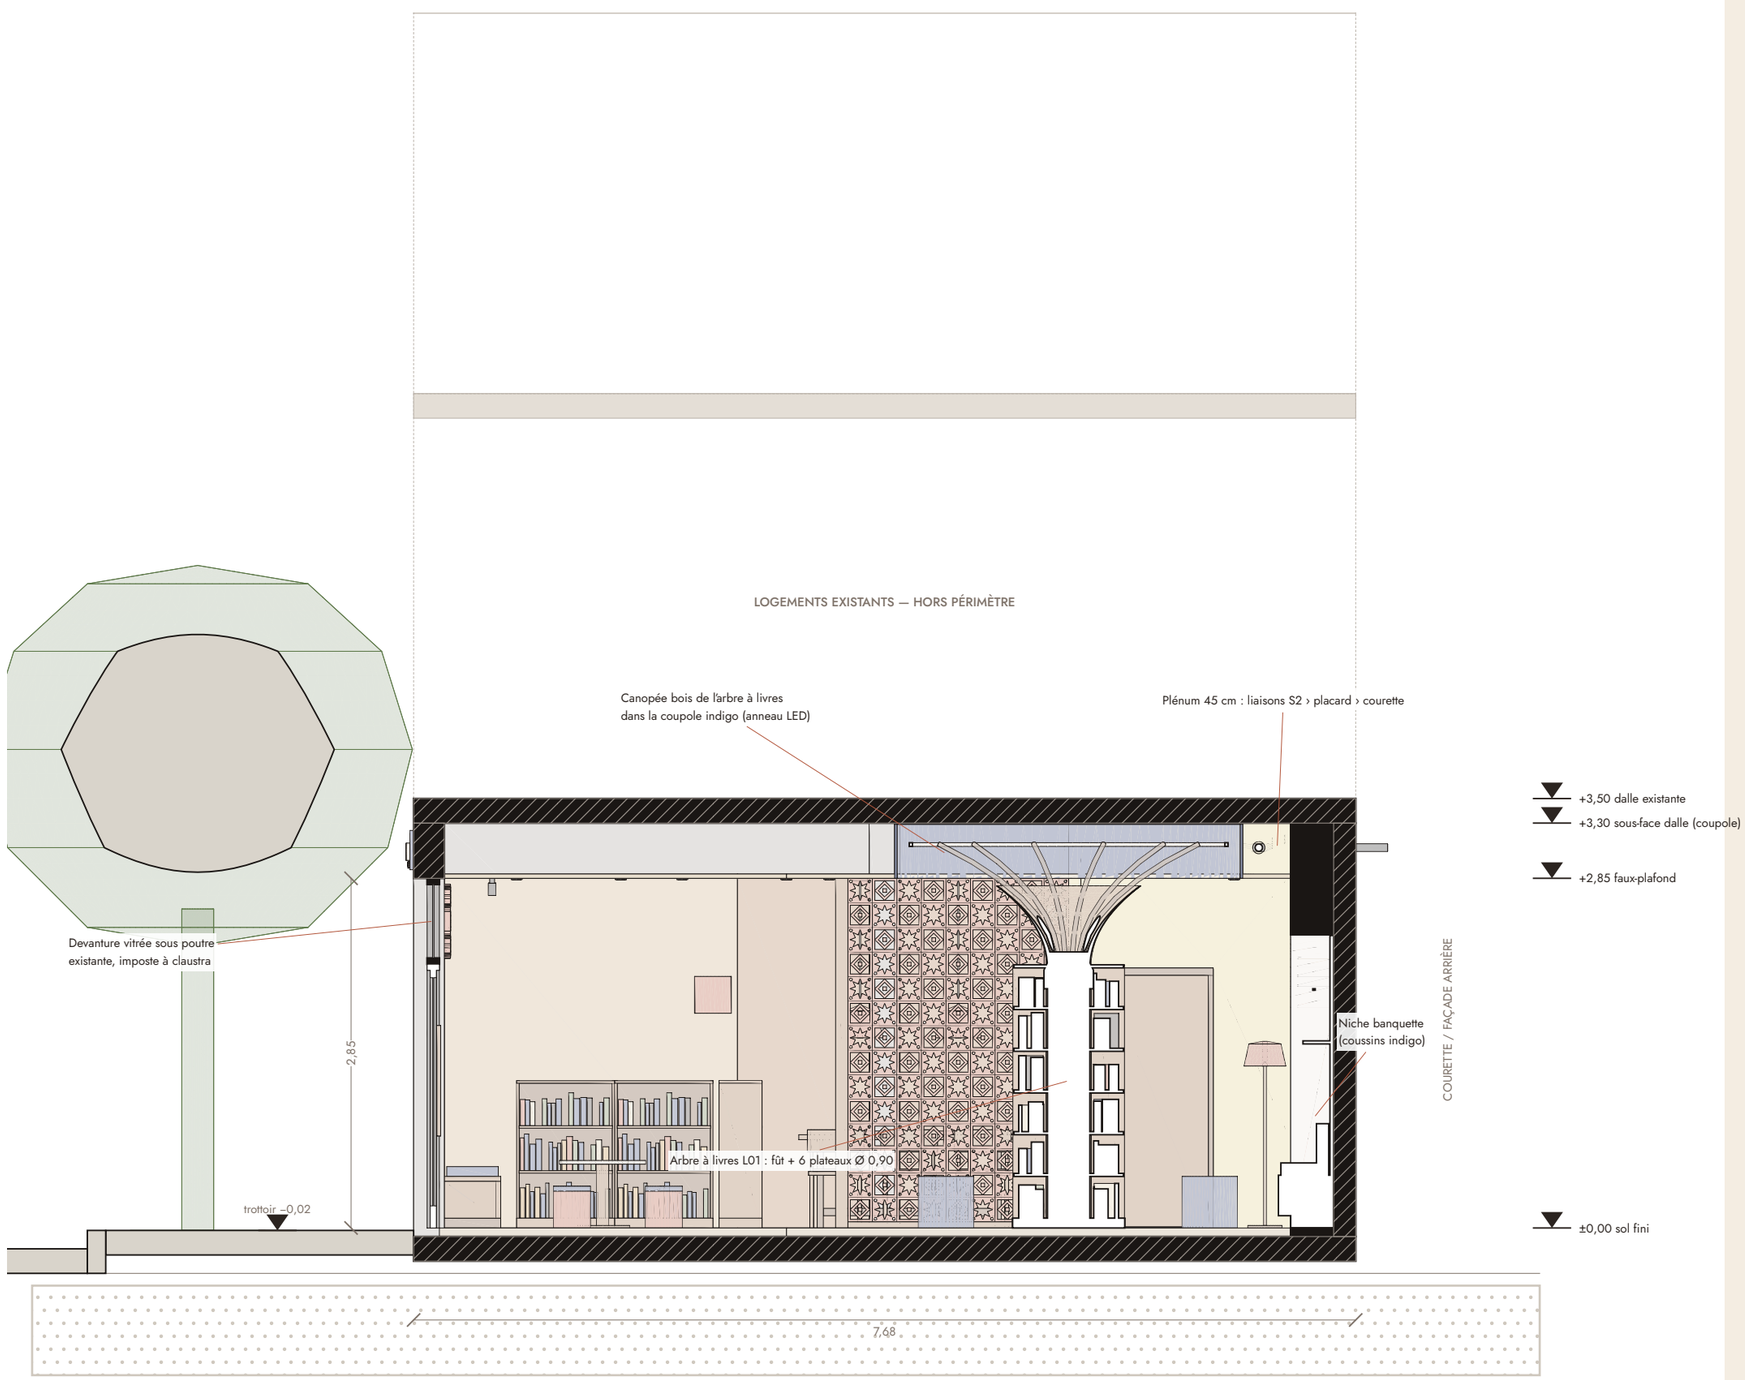

PRINCIPES

Un seul niveau : sol fini ±0,00, dalle haute existante conservée (logements au-dessus).

Faux-plafond acoustique en fibres de bois à +2,85 ; plénum de 45 cm pour les réseaux.

Au-dessus de l'arbre, le plafond s'ouvre en coupole Ø 2,80 jusqu'à la dalle (+3,30),

peinte indigo : la canopée bois s'y épanouit, éclairée par un anneau LED 2700 K.

Devanture : menuiserie acier encre sous la poutre existante, imposte en claustra

terre cuite Adinkra ; porte 0,90 + 0,45 ouvrant vers l'intérieur, seuil plat.

Descentes EU/EV des logements gardées en place, en coffrages acoustiques.

LÉGENDE

- Existant porteur coupé (dalle, poutre, voiles)
- Élément neuf coupé
- Mobilier coupé en silhouette
- Vu au-delà du plan de coupe (traits fins)

Document d'esquisse — dimensions et surfaces indicatives, à vérifier sur site.

PROJET	Bibliothèque Decimo — local RDC, immeuble existant, Abidjan
PHASE	Esquisse (ESQ) · indice V5 · 14/10/2026
MAQUETTE	v5/DECIMO_ESQ_V5.ifc (IFC4, mm)
ÉQUIPE	D.A. Affoué / Stéphanie · technique : hypothèses ESQ Ahoua

PLANCHE 02

K&Démi
ARCHITECTURE · INTÉRIEUR


Bibliothèque Decimo

Élévation de la devanture sur rue

Esquisse V5 · Échelle 1/50 (A3) · Façade sud, vue depuis la rue

Devanture dans la baie existante (poteaux P1-P2-P3, poutre PT1) ; immeuble au-dessus en contexte

Dessin généré par script depuis la maquette IFC4 (arbres d'alignement en transparence)

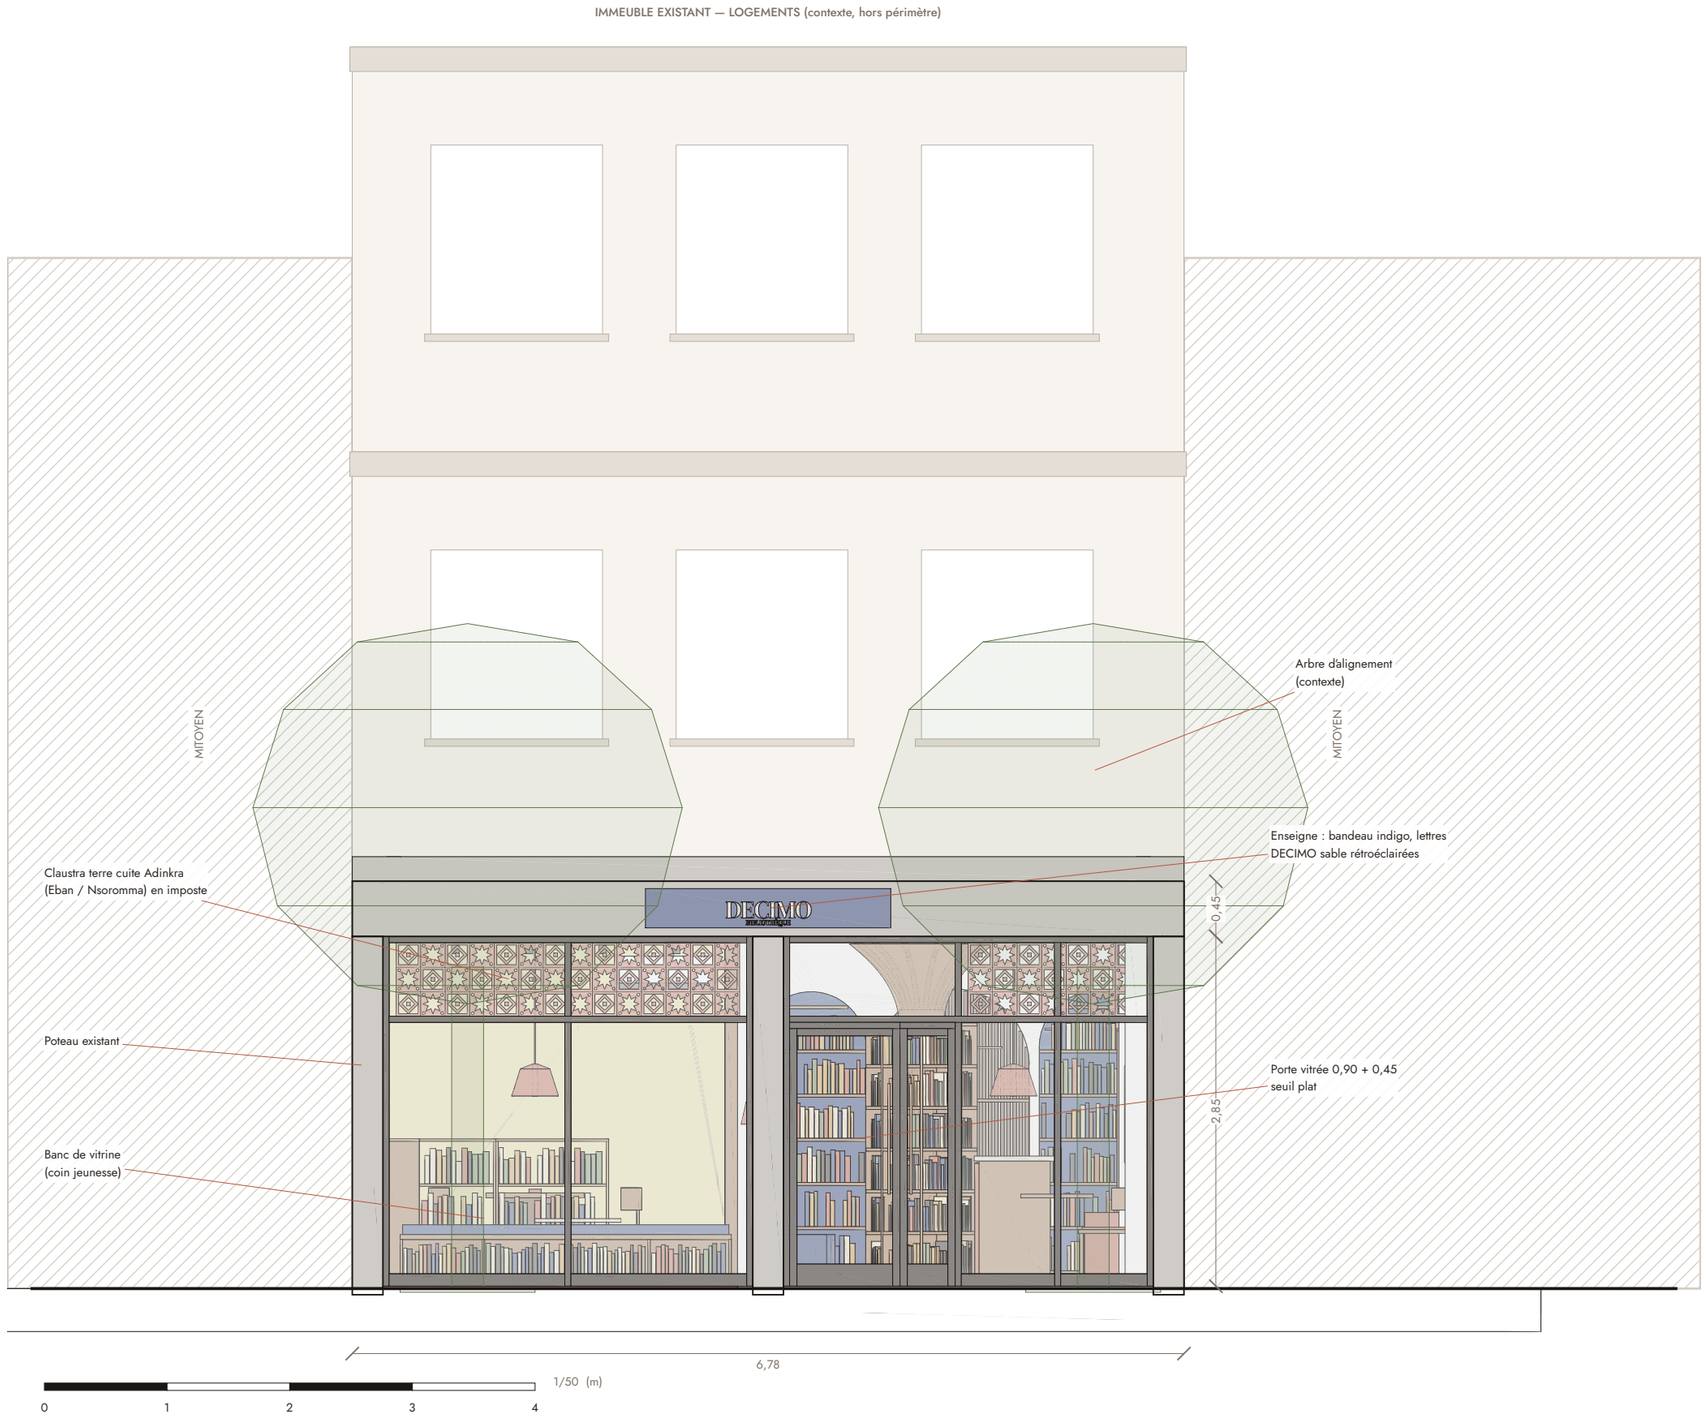

DEVANTURE — PRINCIPES

Pas de façade cintrée : la devanture reste dans la baie existante, sous la poutre.

Menuiserie acier thermolaqué encre, vitrages feuilletés, soubassement de 10 cm.

Imposte : claustra en modules terre cuite 20 × 20 à motifs Adinkra

« Eban » (la clôture) et « Nsoromma » (l'étoile) ; Gye Nyame exclu.

À l'ouest, banc de vitrine en iroko (coin jeunesse) ; à l'est, accueil.

Enseigne sur la poutre : seule touche indigo de la façade.

Fixations sur la structure existante légères, à valider (syndic, BET).

MODULES DE CLAUSTRA (20 × 20 cm)

Alternance en damier des deux modules :

— Eban : carré, losange et cœur plein

— Nsoromma : étoile à 8 branches évidée

Terre cuite, ép. 8 à 10 cm, pose collée

Même module pour le claustra intérieur

Document d'esquisse — dimensions et surfaces indicatives, à vérifier sur site.

PROJET	Bibliothèque Decimo — local RDC, immeuble existant, Abidjan
PHASE	Esquisse (ESQ) · indice V5 · 14/10/2026
MAQUETTE	v5/DECIMO_ESQ_V5.ifc (IFC4, mm)
ÉQUIPE	D.A. Affoué / Stéphanie · technique : hypothèses ESQ Ahoua

PLANCHE 03

K&Démi
ARCHITECTURE · INTÉRIEUR

Bibliothèque Decimo

Élévation intérieure — mur du fond (coupe BB)

Esquisse V5 · Échelle 1/30 (A3) · Regard vers le nord, plan de coupe y = 2,90

Arbre à livres, niches cintrées, claustra Adinkra, bloc sanitaire et splits

Dessin généré par script depuis la maquette IFC4



D.A. — TERRE, OMBRE ET BOIS

Palette encre › terre cuite, iroko, sable ; accent indigo ponctuel.

Murs : enduit terre (argile) sable ocre ; parement BTC derrière les tables.

Sol terrazzo coulé sable à granulats terre cuite ; tomettes au coin jeunesse.

Bois iroko huilé pour l'arbre, les niches, les rayonnages et la banque.

Indigo : coupole, fonds de niches, coussins, porte du placard, zellige du WC.

Lumière 2700 K, IRC 90 mini : downlights, suspensions terre cuite, anneau LED.

PALETTE (styles de surface IFC)

Enduit terre	BTC	Terre cuite	Iroko
#CDAE88	#B07D56	#B4583E	#9A6B43
Terrazzo	**Sable**	**Indigo**	**Encre**
#D9CDBB	#E6D6BF	#2F3E6E	#2B2420

Document d'esquisse — dimensions et surfaces indicatives, à vérifier sur site.

PROJET	Bibliothèque Decimo — local RDC, immeuble existant, Abidjan
PHASE	Esquisse (ESQ) · indice V5 · 14/10/2026
MAQUETTE	v5/DECIMO_ESQ_V5.ifc (IFC4, mm)
ÉQUIPE	D.A. Affoué / Stéphanie · technique : hypothèses ESQ Ahoua

PLANCHE 04

K&Démi
ARCHITECTURE · INTÉRIEUR

Bibliothèque Decimo

Axonométries


Esquisse V5 · Vues 3D générées depuis la maquette IFC4

Axonométrie coupée (dalle, plafonds et murs arasés à +2,40, arbre conservé entier) et axonométrie de la devanture depuis la rue (immeuble au-dessus en contexte)


LECTURE

Le local tient dans l'enveloppe existante : voiles, poteaux, poutre et dalle haute conservés (propriété « Existant porteur - ne pas toucher »). Au centre, l'arbre à livres s'ouvre en canopée dans la coupole indigo. À l'ouest : coin jeunesse en vitrine, espace de travail derrière le claustra Adinkra ; au fond : WC, dégagement-réserve, placard technique. À l'est : accueil près de l'entrée (TD encastré), salon de lecture et coffrage acoustique des descentes EU/EV. Volumes gris clair des vues : contexte non modélisé dans l'IFC.

Axonométrie coupée depuis le sud-est (arasé à +2,40)

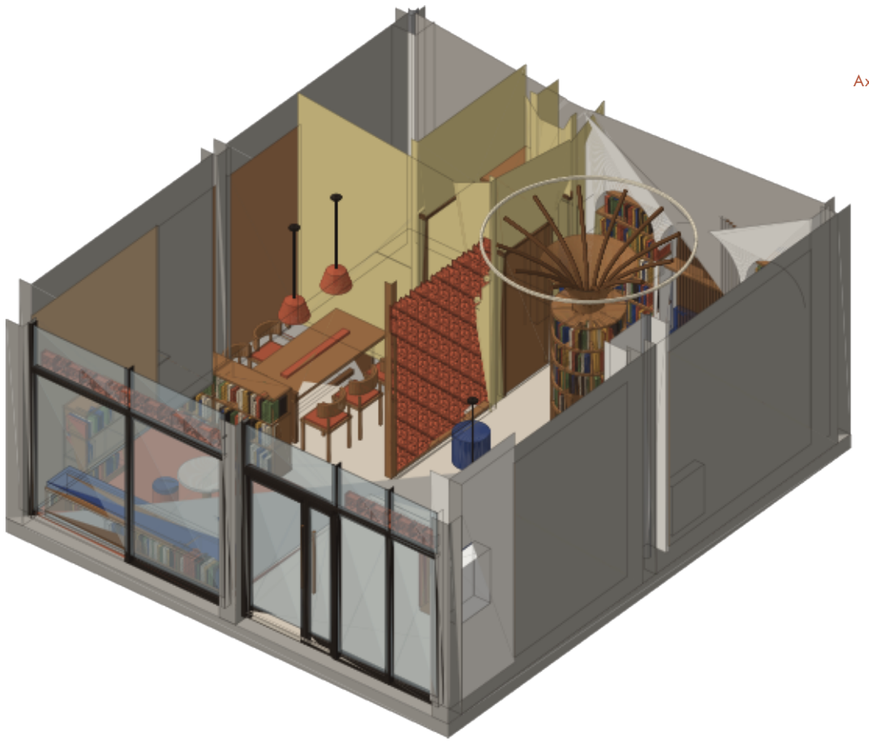

Axonométrie de la devanture depuis la rue (sud-ouest)

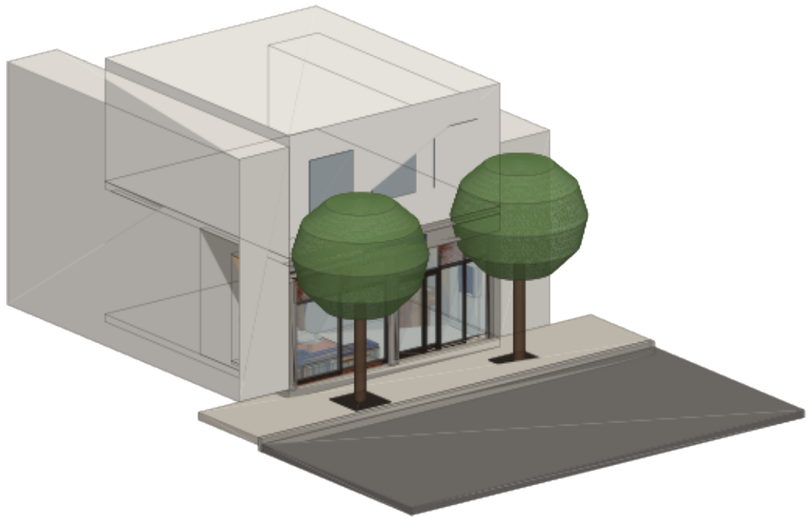

Document d'esquisse — dimensions et surfaces indicatives, à vérifier sur site.

PROJET	Bibliothèque Decimo — local RDC, immeuble existant, Abidjan
PHASE	Esquisse (ESQ) · indice V5 · 14/10/2026
MAQUETTE	v5/DECIMO_ESQ_V5.ifc (IFC4, mm)
ÉQUIPE	D.A. Affoué / Stéphanie · technique : hypothèses ESQ Ahoua

PLANCHE 05

K&Démi
ARCHITECTURE · INTÉRIEUR

Depuis l'entrée : accueil, arbre à livres, niches cintrées



Depuis le trottoir d'en face



Bibliothèque Decimo

Perspectives

Esquisse V5 · Vues 3D générées depuis la maquette IFC4

Perspective intérieure depuis l'entrée vers l'arbre à livres et le mur des niches

Perspective depuis le trottoir d'en face (arbres d'alignement, immeuble en contexte)

AMBIANCE

Terre, ombre et bois : enduit terre, BTC, terrazzo, tomettes et iroko,
lumière chaude 2700 K, accent indigo pour la coupole et les assises.
Rendu schématique (couleurs des styles IFC, ombrage simple),
sans textures ni éclairage calculé : à reprendre en APS (Twinmotion,
Enscape ou Blender) à partir de la maquette IFC.

Document d'esquisse — dimensions et surfaces indicatives, à vérifier sur site.

PROJET	Bibliothèque Decimo — local RDC, immeuble existant, Abidjan
PHASE	Esquisse (ESQ) · indice V5 · 14/10/2026
MAQUETTE	v5/DECIMO_ESQ_V5.ifc (IFC4, mm)
ÉQUIPE	D.A. Affoué / Stéphanie · technique : hypothèses ESQ Ahoua

PLANCHE 06