K&Démi
ARCHITECTURE · INTÉRIEUR

Identité K&Démi

Logo revu, palette, typographies, grille

LOGO, 3 PISTES DESSINÉES À LA MAIN (SVG)

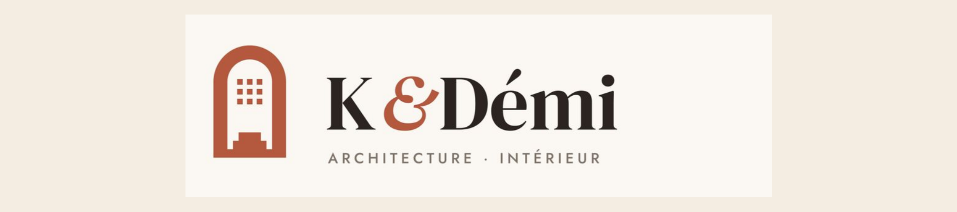

A · Arche-seuil : arche évidée, seuil à 3 marches, claustra 3x3

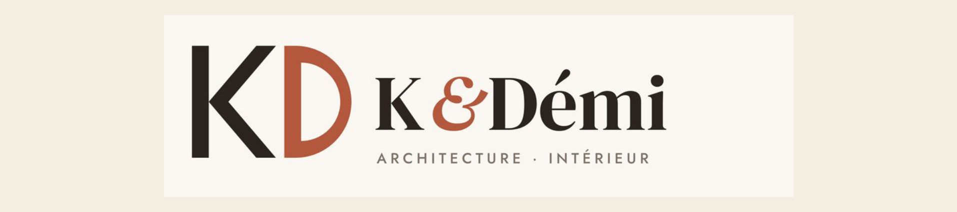

B · Monogramme KD : fût du K, D en demi-arche

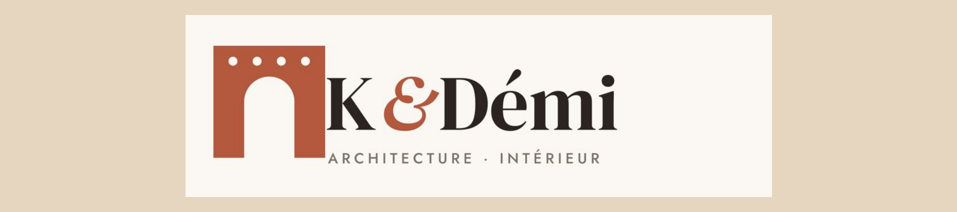

C · Module claustra : arche creusée dans un bloc percé (recommandé)

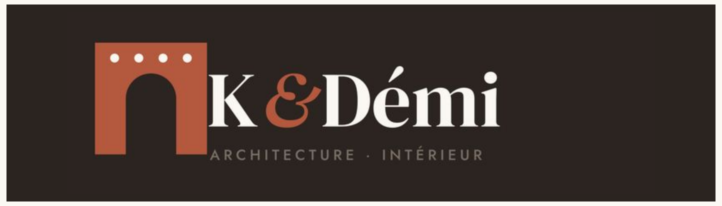

Symbole seul : avatar, tampon, favicon

Pourquoi C : le bloc reprend la claustra et la baie cintrée du projet. Lisible à 8 mm, une seule couleur, pas de dégradé. Le & italique terre cuite reste la signature du mot.

PALETTE AGENCE

Encre	#2B2420	texte, traits
Terre cuite	#B4583E	signature
Iroko	#9A6B43	bois, repères
Sable	#E6D6BF	aplats
Sable clair	#F4EDE2	fonds
Blanc chaux	#FBF8F3	page
Taupe	#7D7168	texte 2
Olive	#5F7A4B	végétal, rare

TYPOGRAPHIES (LIBRES, GOOGLE FONTS, OFL)

DM Serif Display

Titres, logo, chiffres clés · corps 18 à 36 pt

Jost Regular / Medium

Texte 8 à 10 pt, légendes 7 pt, capitales espacées +12 %

GRILLE A3 PAYSAGE

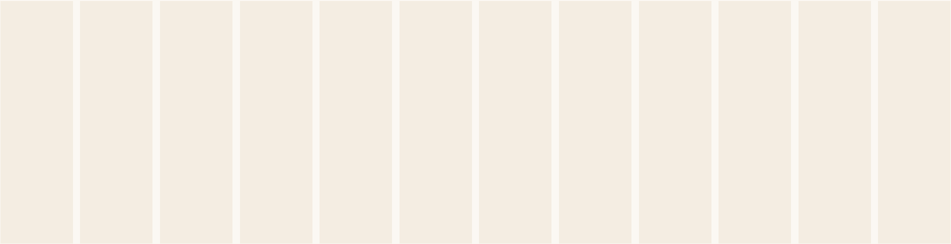

12 colonnes · marges 15 mm · gouttière 5 mm · bandeau titre 17 mm · pied 6 mm

Bibliothèque Decimo

Page type du dossier : plan du rez-de-chaussée, esquisse V4, échelle 1/50

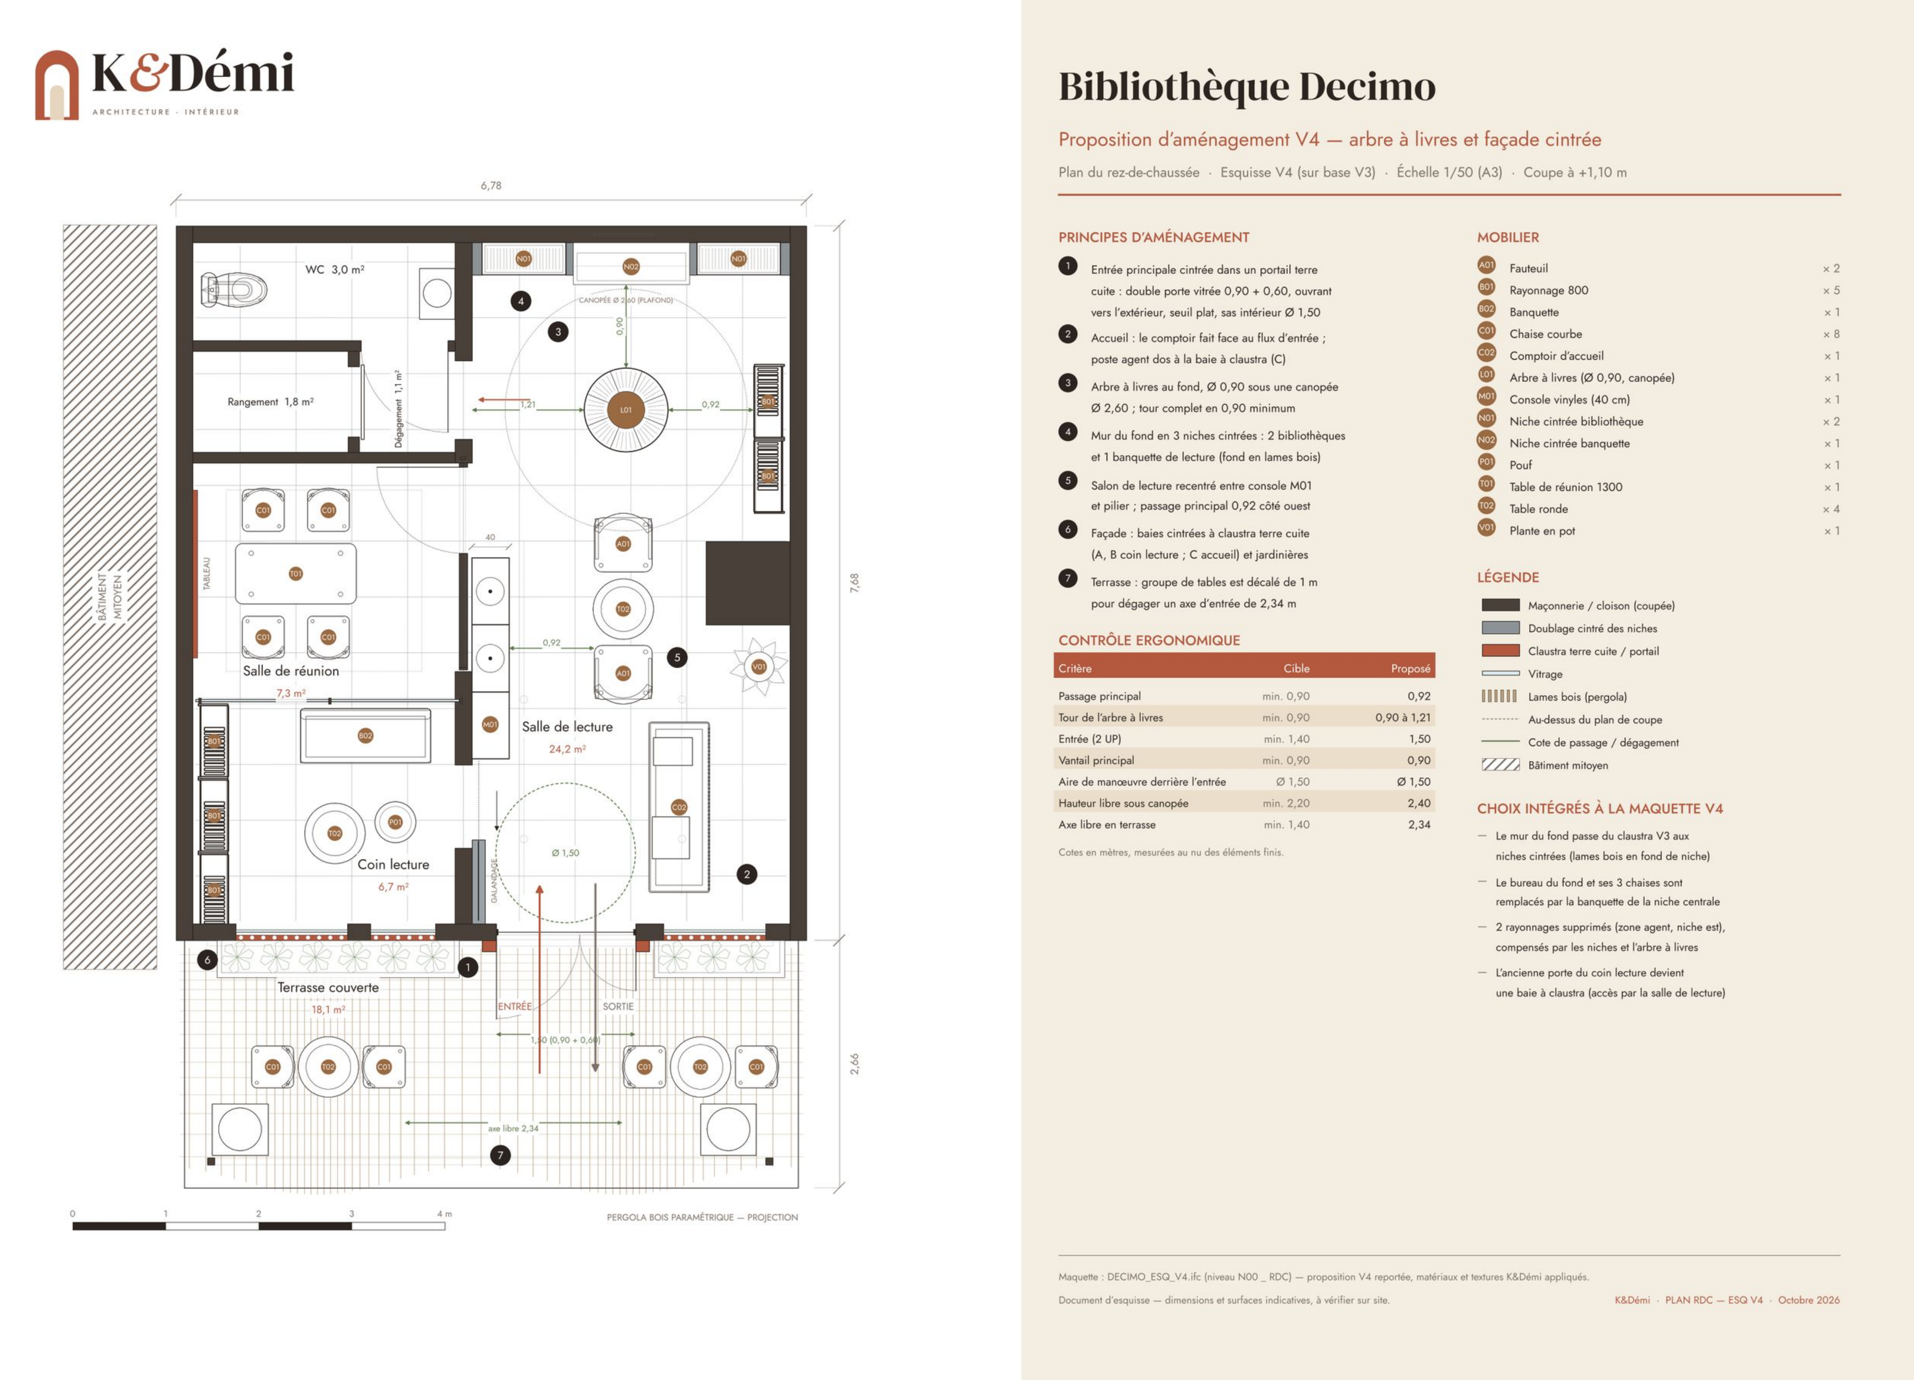

Bibliothèque Decimo

Proposition d'aménagement V4 — arbre à livres et façade cintrée

Plan du rez-de-chaussée · Esquisse V4 (sur base V3) · Échelle 1/50 (A3) · Coupe à +1,10 m

PRINCIPES D'AMÉNAGEMENT

❶ Entrée principale cintrée dans un portail terre cuite : double porte vitrée 0,90 + 0,60, ouvrant vers l'extérieur, seuil plat, sas intérieur Ø 1,50

❷ Accueil : le comptoir fait face au flux d'entrée ; poste agent dos à la baie à claustra (C)

❸ Arbre à livres au fond, Ø 0,90 sous une canopée Ø 2,60 ; tour complet en 0,90 minimum

❹ Mur du fond en 3 niches cintrées : 2 bibliothèques et 1 banquette de lecture (fond en lames bois)

❺ Salon de lecture recentré entre console M01 et pilier ; passage principal 0,92 côté ouest

❻ Façade : baies cintrées à claustra terre cuite (A, B coin lecture ; C accueil) et jardinières

❼ Terrasse : groupe de tables est décalé de 1 m pour dégager un axe d'entrée de 2,34 m

CONTRÔLE ERGONOMIQUE

Critère	Cible	Proposé
Passage principal	min. 0,90	0,92
Tour de l'arbre à livres	min. 0,90	0,90 à 1,21
Entrée (2 UP)	min. 1,40	1,50
Vantail principal	min. 0,90	0,90
Aire de manœuvre derrière l'entrée	Ø 1,50	Ø 1,50
Hauteur libre sous canopée	min. 2,20	2,40
Axe libre en terrasse	min. 1,40	2,34

Cotes en mètres, mesurées au nu des éléments finis.

MOBILIER

A01	Fauteuil	× 2
B01	Rayonnage 800	× 5
B02	Banquette	× 1
C01	Chaise courbe	× 8
C02	Comptoir d'accueil	× 1
L01	Arbre à livres (Ø 0,90, canopée)	× 1
M01	Console vinyles (40 cm)	× 1
N01	Niche cintrée bibliothèque	× 2
N02	Niche cintrée banquette	× 1
P01	Pouf	× 1
T01	Table de réunion 1300	× 1
T02	Table ronde	× 4
V01	Plante en pot	× 1

LÉGENDE

■	Maçonnerie / cloison (coupée)
■	Doublage cintré des niches
🟥	Claustra terre cuite / portail
▭	Vitrage
▥	Lames bois (pergola)
┈	Au-dessus du plan de coupe
—	Cote de passage / dégagement
▨	Bâtiment mitoyen

CHOIX INTÉGRÉS À LA MAQUETTE V4

- Le mur du fond passe du claustra V3 aux niches cintrées (lames bois en fond de niche)
- Le bureau du fond et ses 3 chaises sont remplacés par la banquette de la niche centrale
- 2 rayonnages supprimés (zone agent, niche est), compensés par les niches et l'arbre à livres
- L'ancienne porte du coin lecture devient une baie à claustra (accès par la salle de lecture)

Maquette : DECIMO_ESQ_V4.ifc (niveau N00 _ RDC) — proposition V4 reportée, matériaux et textures K&Démi appliqués.

Document d'esquisse — dimensions et surfaces indicatives, à vérifier sur site.

K&Démi · PLAN RDC — ESQ V4 · Octobre 2026

PRINCIPES

① Un seul seuil cintré, centré sur la rue, cadre l'arbre à livres.

② Trois baies en claustra terre cuite filtrent le soleil de l'après-midi.

③ La canopée terre cuite de l'arbre est le seul objet fort de la salle.

④ Bois iroko pour tout ce qui se touche, chaux pour tout ce qui se voit.

⑤ Ventilation traversante : claustra + pergola, pas de baie fermée au sud.

SURFACES (IFC V4)

Salle de lecture	24,2 m²
Salle de réunion	7,3 m²
Coin lecture	6,7 m²
WC	3,0 m²
Rangement	1,8 m²
Terrasse couverte	18,1 m²

PROJET	Bibliothèque Decimo, Abidjan
PHASE	Esquisse V4
ÉCHELLE	1/50 en A3
DATE	Octobre 2026
AGENCE	K&Démi, architecture · intérieur

K&Démi
ARCHITECTURE · INTÉRIEUR

D.A de la bibliothèque

Terre, ombre et bois : une salle de lecture fraîche sous le soleil d'Abidjan

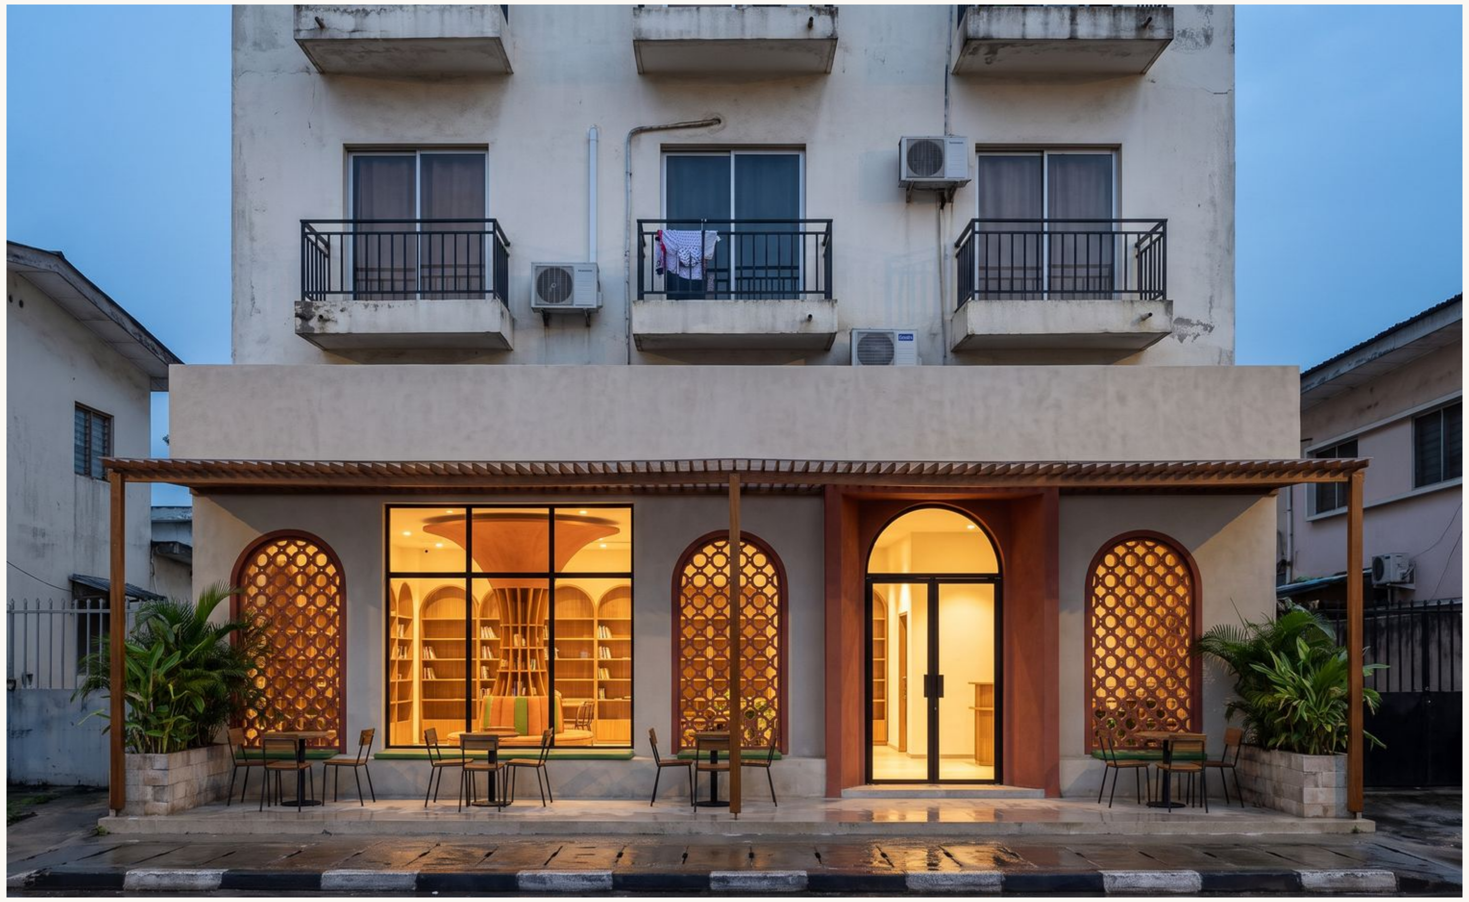

Devanture : local en pied d'immeuble, portail terre cuite, vitrine, claustra

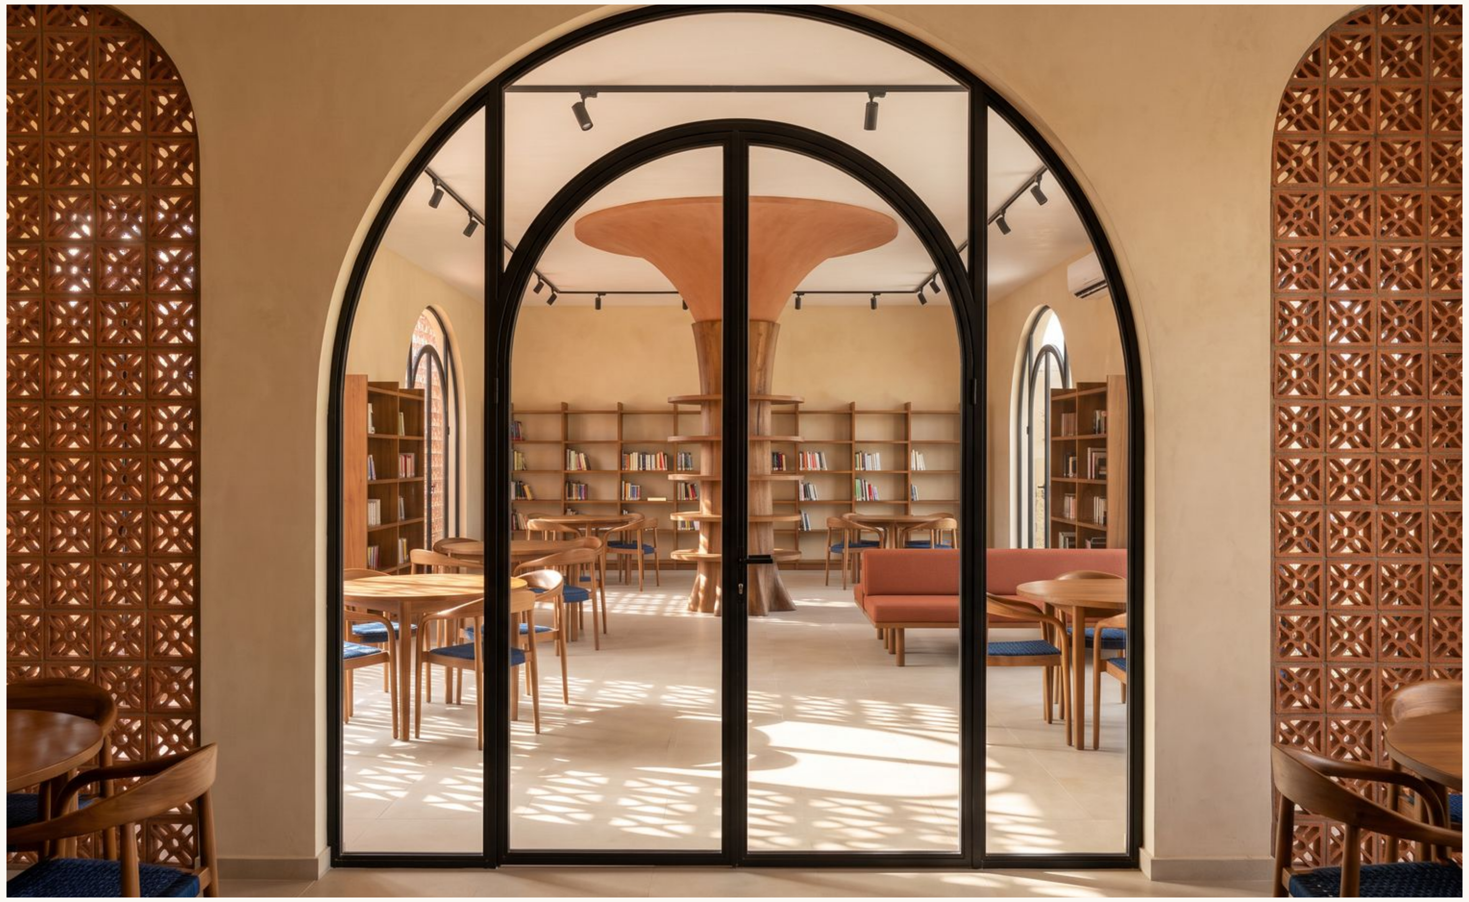

RDC : vue depuis l'entrée vers l'arbre à livres

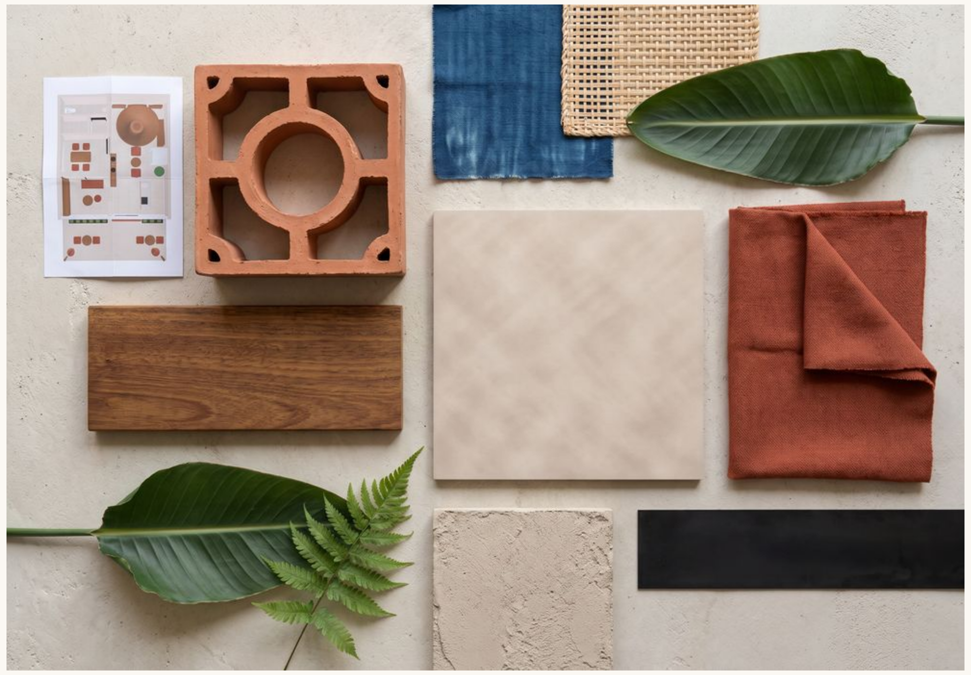

Maquette matière sur le plan V4

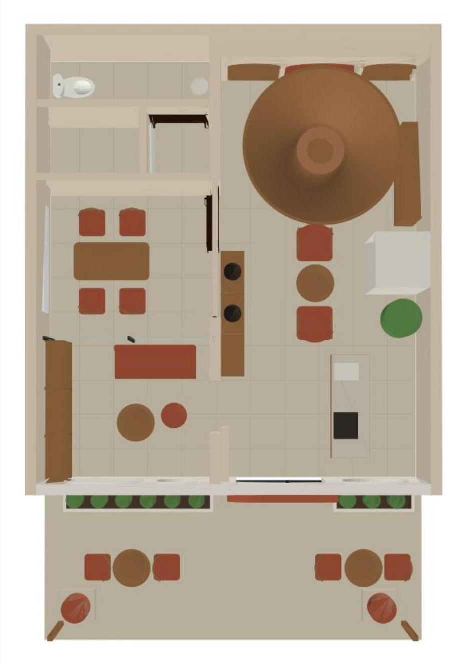

Plan RDC issu de l'IFC V4 (local commercial, logements au-dessus)

MATÉRIAUX

Claustra terre cuite	Iroko huilé	Chaux sable	Enduit terre cuite
Grès cérame sable	Acier noir mat	Laine terre cuite	Indigo #2F3A56

PALETTE INTÉRIEURE

#B4583E #9A6B43 #E6D6BF #FBF8F3 #2B2420 #2F3A56 #5F7A4B

AMBIANCE

Pénombre fraîche, lumière tamisée
par la claustra, 2700 K le soir
Aucun dégradé, aucun motif plaqué

MOBILIER

Iroko sur mesure, chaises courbes
assises raphia, laine terre cuite
coussins indigo artisanaux

LUMINAIRES

Rails noirs + spots IRC 90
anneau LED sous canopée
suspensions papier, appliques IP65

VÉGÉTAL

Ficus lyrata, Strelitzia
fougères, Dracaena
bougainvillier sur pergola