

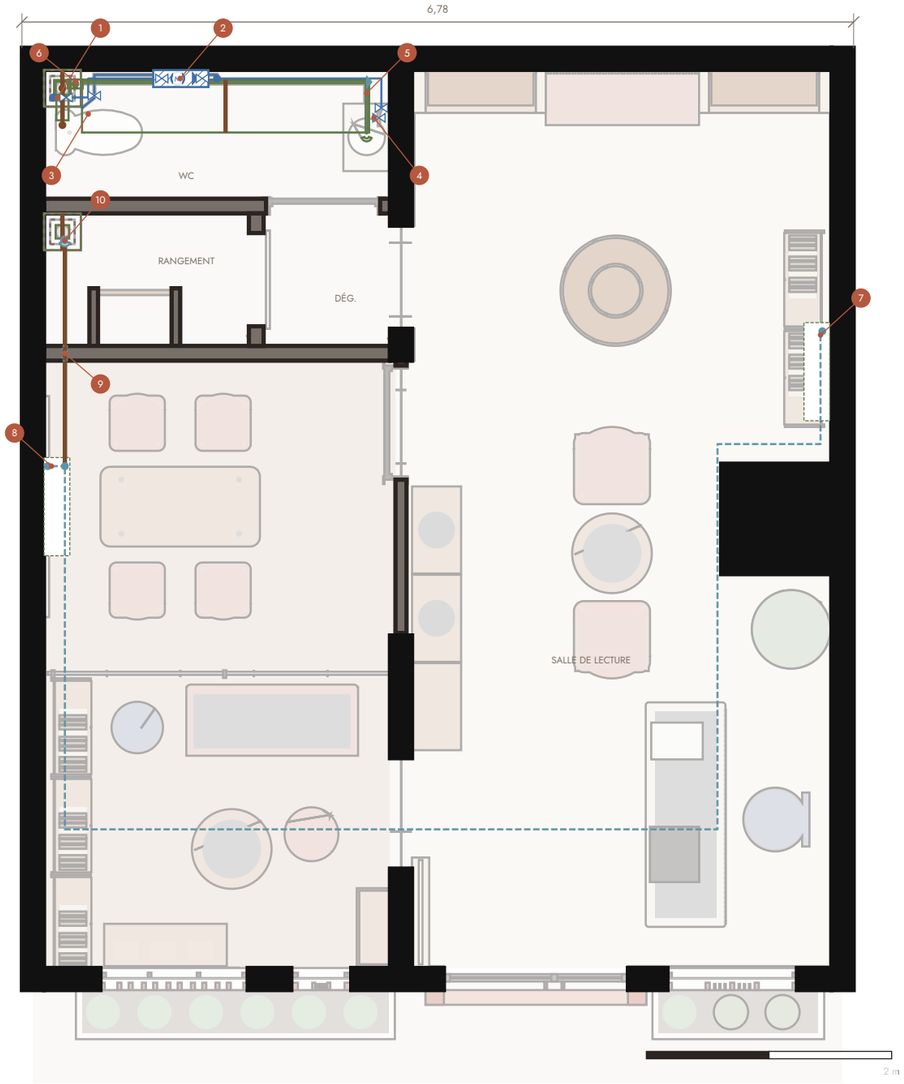


ZOOM WC / RANGEMENT — 1/25

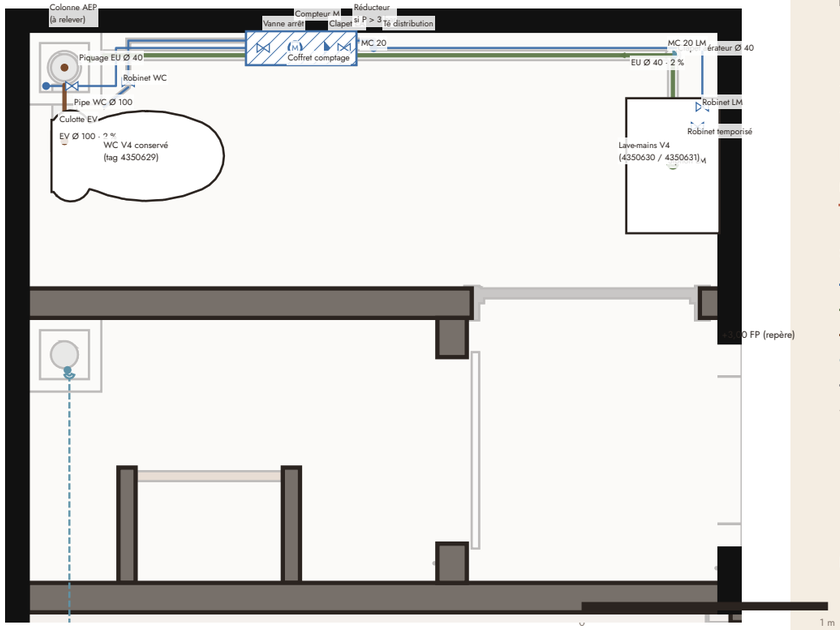

ÉLÉVATION MUR NORD WC — 1/25

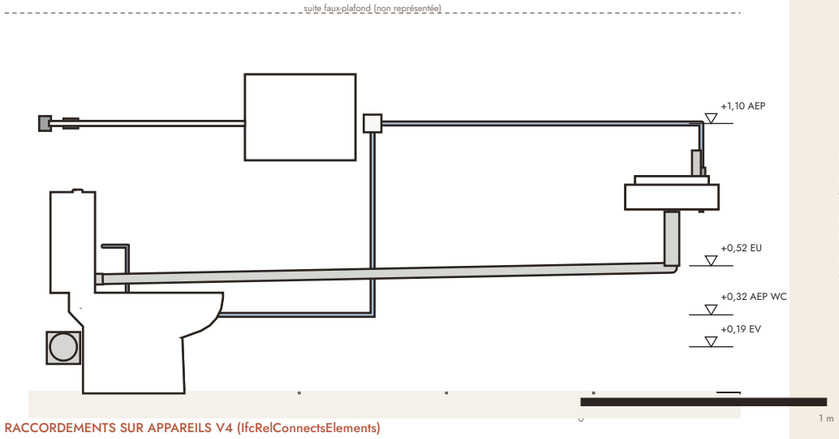

RÉSEAUX IFC — KDEMI_Reseau / KDEMI_Plomberie

RÉSEAU	OBJ.	L.M. DN	MATÉRIAU	PENTE	STATUT
CFO - Courants forts	4	0,0 —	—	—	À relever sur site
AEP - Eau froide	15	8,6 10 / 12 / 15…	Acier galvanisé / PEH…	—	À relever sur site
EU - Eaux usées	4	2,7 32	PVC M1 NF Me	1.9 %	À relever sur site
EV - Eaux vannes	4	0,2 100	PVC M1 NF Me	2.0 %	À relever sur site
Condensats des 2 splits	9	2,7 32	PVC M1 NF Me	1.9 %	À relever sur site
VP - Ventilation primaire d…	3	0,0 —	—	—	À vérifier avec l…

RACCORDEMENTS SUR APPAREILS V4 (IfcRelConnectsElements)

ÉLÉMENT V5	APPAREIL V4	TAG	DESCRIPTION
Flexible d'alimentation du rése…	WC à réservoir:WC à réservo…	4350629	Alimentation eau froide du réservoir
Robinet temporisé eau froide (l…	4350630	4350630	Robinet temporisé posé sur le plan…
Siphon du lave-mains V4	4350631	4350631	Raccordement de la bonde de la vasq…
Pipe WC Ø 100 (raccord cuvette…	WC à réservoir:WC à réservo…	4350629	Raccordement de la sortie de cuvette

PAS DE CHAUFFE-EAU

Un seul lave-mains, eau froide réseau (26-30 °C à Abidjan).
Pas de circuit 20 A dédié ni de stockage d'eau chaude (légionelles).
WC et lave-mains V4 conservés, raccordés en V5 sans duplication.

K&Démi

Bibliothèque Decimo

Plomberie — AEP, EU, EV et condensats

Plan sanitaire · Échelle 1/50 et 1/25 (A3) · Coupe à +1,00

SYMBOLES

- Eau froide AEP (multicouche)
- Eaux usées EU (PVC)
- Eaux vannes EV (PVC)
- Condensats (refoulement mini-pompes)
- Ventilation primaire / clapet aérateur
- Tronçon en plénum (z > 2,00) : tirets
- Vanne / robinet d'arrêt
- Compteur divisionnaire
- Clapet (EA, aérateur)
- Té / culotte / piquage
- Siphon / siphon sec

POINTS SINGULIERS

1. Colonne / piquage AEP immeuble (position, DN, pression à relever)
2. Coffret de comptage (vanne, compteur, clapet EA, réducteur si P > 3 bar)
3. WC V4 conservé (4350629), alimentation flexible — non dupliqué
4. Lave-mains V4 conservé (plan 4350630, vasque 4350631), robinet temporisé
5. Siphon lave-mains + clapet aérateur Ø 40 sur antenne EU
6. Culotte / piquage Ø 40 sur descente EU/EV 1 (à relever)
7. Mini-pompe condensats split 1 (refoulement vers collecteur)
8. Mini-pompe condensats split 2
9. R8 Ø 0,04 : passage condensats (cloison placo non porteuse)
10. Siphon sec condensats + piquage sur descente EU/EV 2

PRINCIPES

Pas de chauffe-eau : un seul lave-mains, eau froide réseau (26-30 °C à Abidjan), pas de circuit 20 A dédié ni de stockage d'eau chaude (légionelles).
WC et lave-mains V4 conservés, non dupliqués : raccordements V5 via IfcRelConnectsElements « Raccordement V5 sur appareil V4 conservé ».
Branchements immeuble / descentes EU·EV : position et diamètres à relever.
Réducteur de pression posé seulement si P mesurée > 3 bar.
Condensats refoulés par mini-pompes vers la descente EU/EV 2 (siphon sec).

PROJET	Bibliothèque Decimo — RDC sous logements, Abidjan
PHASE	ESQ V5 — aménagement sur existant V4
PLANCHE	A10 — Plomberie — AEP, EU, EV et condensats
ÉCHELLE	1/50 et 1/25 · format A3
MAQUETTE	v5/DECIMO_ESQ_V5.ifc (IFC4) · sha256 34152b66f6…
DATE	Octobre 2026 · indice A

Esquisse : cotes et surfaces indicatives, existant V4 à relever sur site.