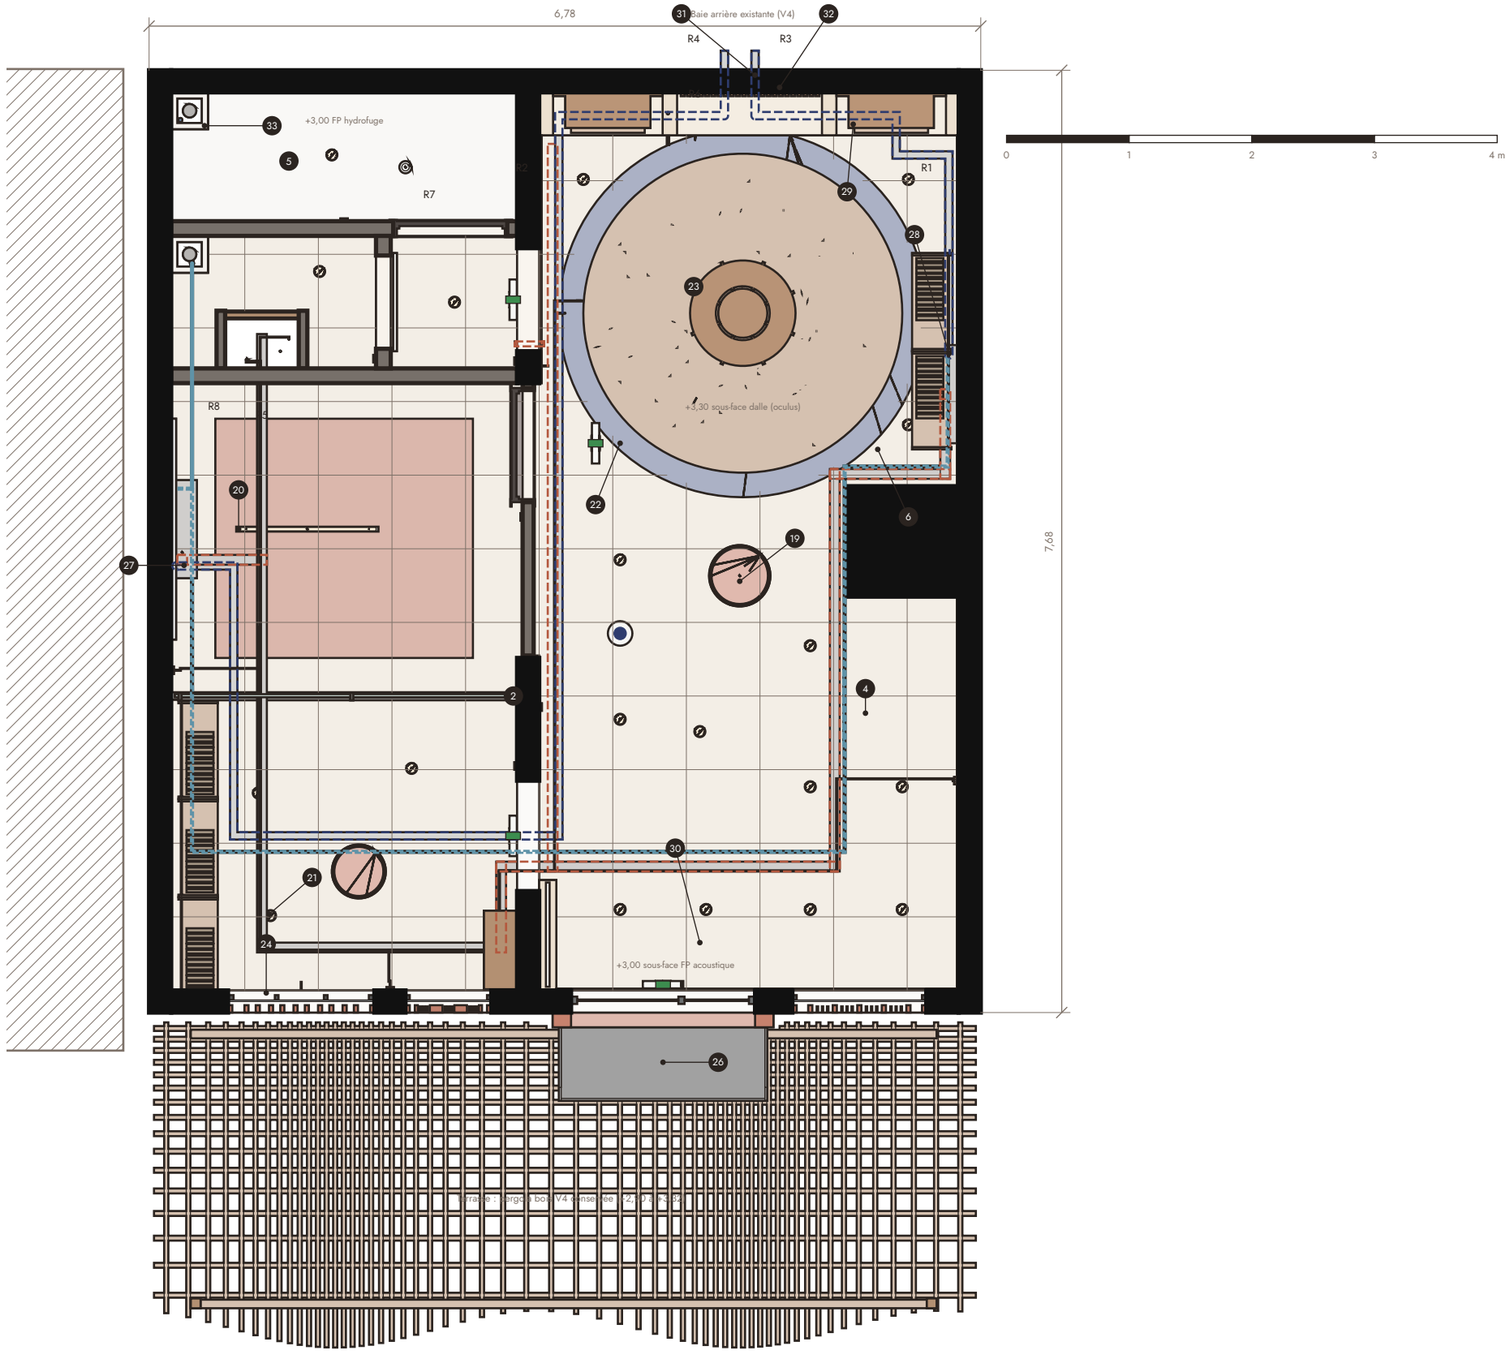


K&Démi

Bibliothèque Decimo

Plan de faux-plafond et réseaux

Vu de dessous (plan réfléchi) · Échelle 1/50 (A3) · Coupe à +2,00

PRINCIPES (HYPOTHÈSES ESQ AHOUA)

Faux-plafond acoustique +3,00 (dalles 0,60, ép. 40 mm) ; plénum 0,26 sous dalle haute (minimum 0,25).
Aucun percement dans poteaux, voiles ni dalle haute : liaisons splits et câbles
cheminent en plénum puis dans le doublage des niches, et sortent par la baie arrière
EXISTANTE (imposte : panneau passe-liaisons 32, réservations R3, R4 Ø 0,10).
Splits 9 000 BTU/h en partie haute de murs pleins, hors aplomb des tables ;
condensats refoulés par mini-pompe vers la descente EU/EV 2 (siphon sec).
Câbles : placard technique › plénum (R5 dans cloison placo) › tableau divisionnaire.
Descentes EU/EV de l'immeuble : coffrages 0,30 × 0,30, position à relever sur site.
Réseaux détaillés : voir planches A09 (électricité), A10 (plomberie), A11 (détails).

REPÈRES DE L'AMÉNAGEMENT V5

- 2 Cloison légère / retombée BA13 (ajout V5)
- 4 Faux-plafond acoustique (+3,00, plénum 0,26)
- 5 Faux-plafond hydrofuge WC (+3,00)
- 6 Oculus Ø 2,80 : bandeau iroko, sous-face de dalle indigo
- 19 Suspension terre cuite 2700 K
- 20 Linéaire suspendu acier noir 2700 K
- 21 Downlight encastré Ø 90, 2700 K
- 22 Anneau LED indirect de l'oculus
- 23 Anneau LED sous la canopée
- 24 Réglette LED de vitrine
- 26 Spot sous marquise IP65
- 27 Split mural 9 000 BTU/h (2,6 kW)
- 28 Mini-pompe de relevage des condensats
- 29 Liaisons split (faux-plafond -> doublage -> baie arrière)
- 30 Chemin de câbles 80 x 40 en plénum
- 31 Réservation Ø 0,10 (hors structure)
- 32 Panneau passe-liaisons en imposte de la baie arrière
- 33 Coffrage acoustique 0,30 x 0,30 descente EU/EV (à relever)

LÉGENDE

- Existant porteur coupé à +2,00
- Faux-plafond acoustique, trame 0,60
- Liaisons frigorifiques (plénum, doublage)
- Condensats refoulés (plénum, R8)
- Chemin de câbles 80 × 40 en plénum
- Descente EU/EV Ø 100 en coffrage (hypothèse)
- BAES (E7) / AP Wi-Fi (VDI)

PROJET	Bibliothèque Decimo — RDC sous logements, Abidjan
PHASE	ESQ V5 — aménagement sur existant V4
PLANCHE	A02 — Plan de faux-plafond et réseaux
ÉCHELLE	1/50 · format A3
MAQUETTE	v5/DECIMO_ESQ_V5.ifc (IFC4) · sha256 34152b66f6…
DATE	Octobre 2026 · indice A

Esquisse : cotes et surfaces indicatives, existant V4 à relever sur site.