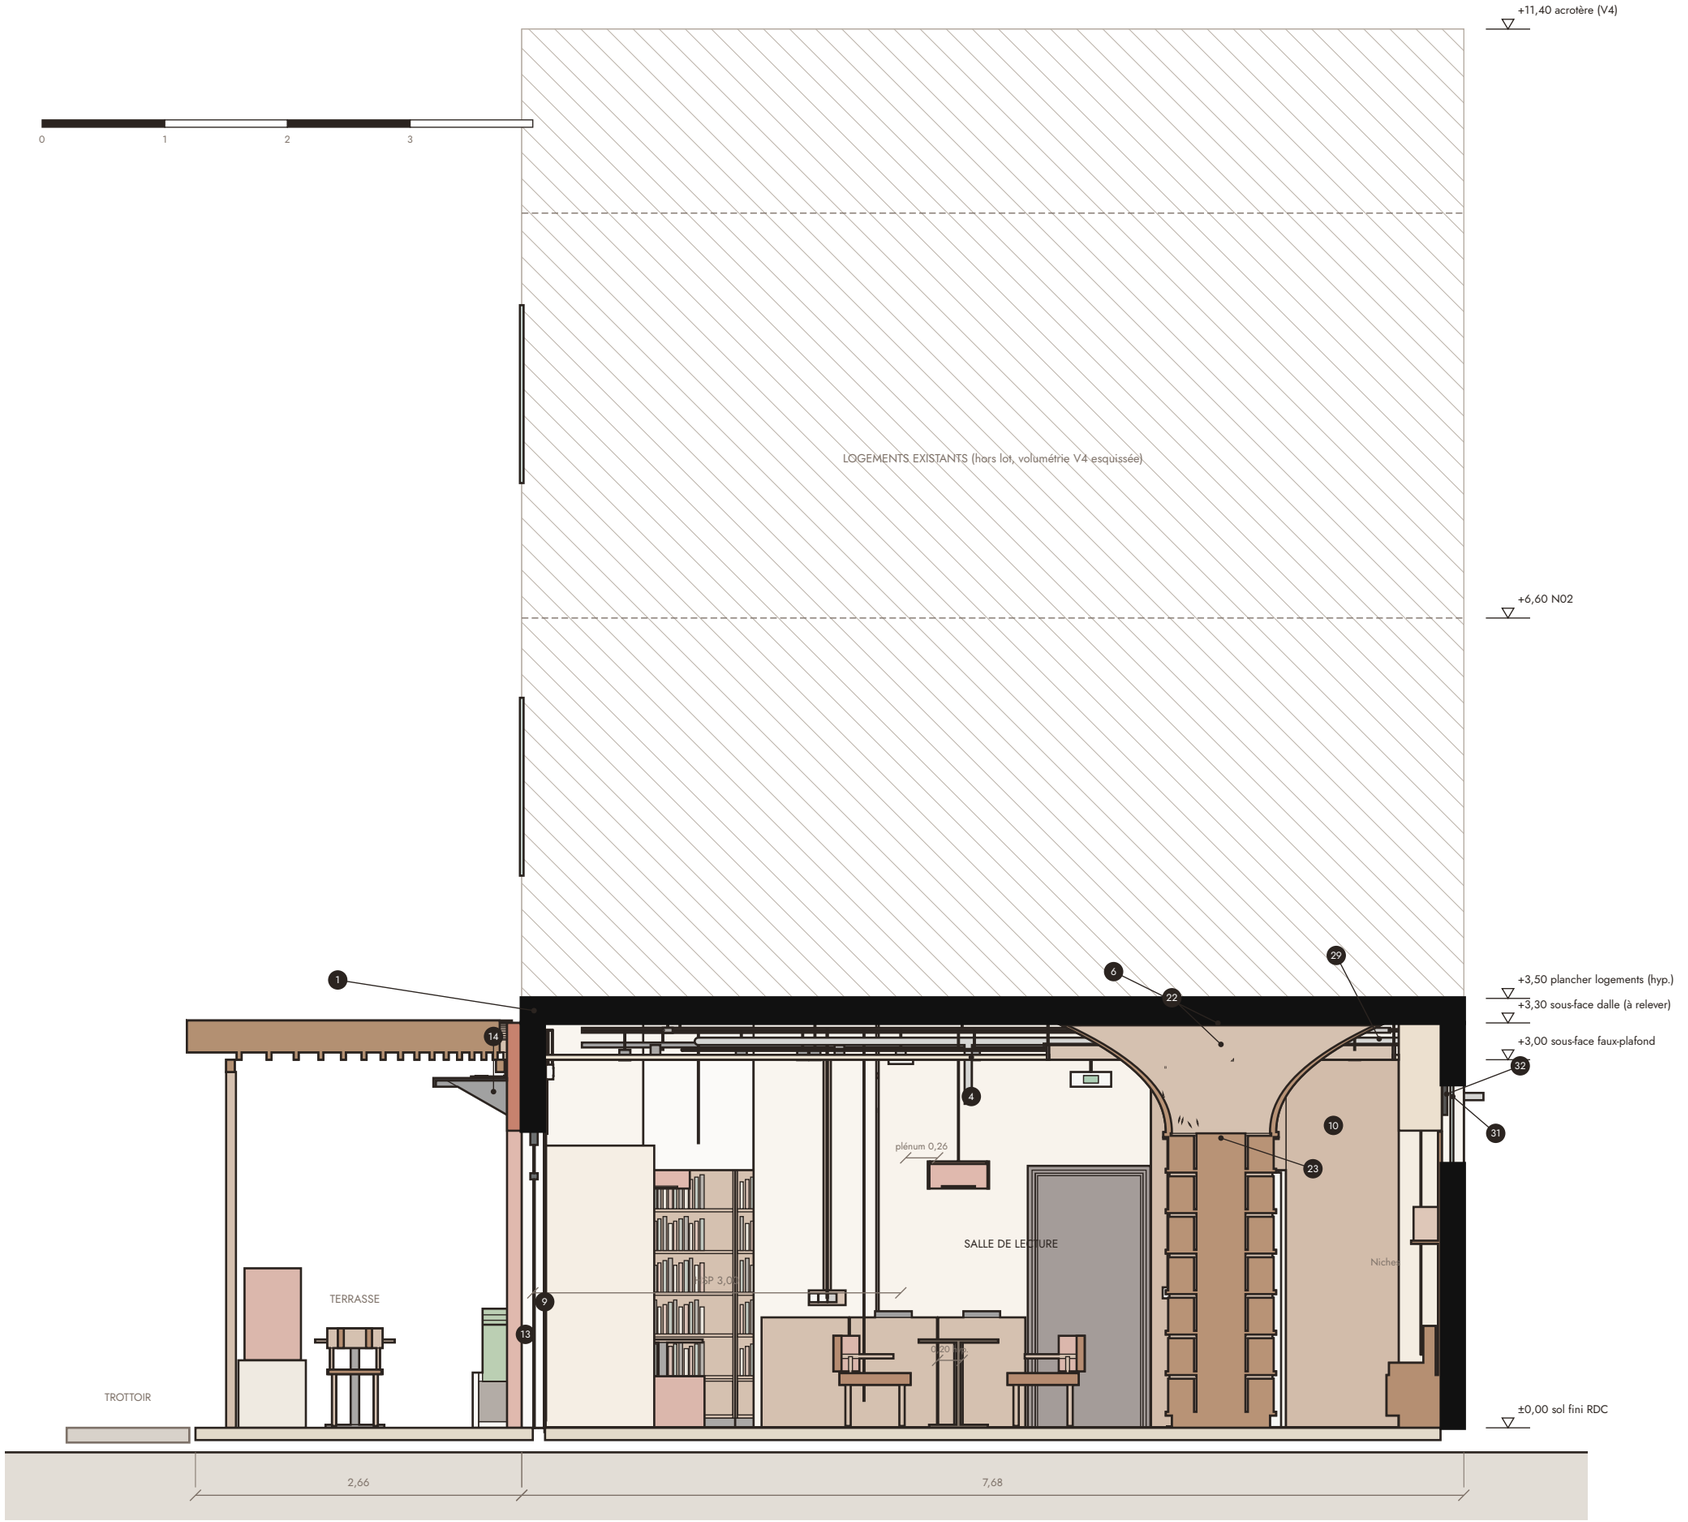


K&Démi

Bibliothèque Decimo

Coupe AA sur l'arbre à livres

Coupe x = 4,75 vers l'ouest · Échelle 1/50 (A3) · Logements existants esquissés

LECTURE DE LA COUPE

Gros œuvre V4 repris tel quel (GlobalId, placements, géométrie : écarts nuls).
Dalle haute absente de la V4 : ajoutée sans modifier l'emprise (rep. 1),
épaisseur 0,20 en hypothèse ; elle double la base du volume « logements » V4.
Faux-plafond acoustique abaissé à +3,00 : plénum 0,26 (minimum exigé 0,25).
Oculus Ø 2,80 autour de l'arbre à livres : sous-face de dalle laquée indigo,
bandeau iroko et anneau LED indirect 2700 K (rep. 6, 22).
Liaisons split en plénum › doublage cintré des niches › imposte de la baie
arrière existante (panneau 32, réservations R3/R4 Ø 0,10) : aucune traversée
de poteau, voile ou dalle.

REPÈRES DE L'AMÉNAGEMENT V5

1. Dalle haute existante (ajoutée, hypothèse ép. 0,20)
4. Faux-plafond acoustique (+3,00, plénum 0,26)
6. Oculus Ø 2,80 : bandeau iroko, sous-face de dalle indigo
9. Enduit terre (argile locale) 15 mm
10. Lambris iroko à claire-voie
13. Claustras terre cuite : inserts Adinkrahene et Eban
14. Marquise acier noir (débord 0,60)
22. Anneau LED indirect de l'oculus
23. Anneau LED sous la canopée
29. Liaisons split (faux-plafond -> doublage -> baie arrière)
31. Réservation Ø 0,10 (hors structure)
32. Panneau passe-liaisons en imposte de la baie arrière

LÉGENDE

- Existant porteur coupé et dalle haute (hypothèse)
- Logements existants (volumétrie V4, hors lot)
- Planchers des logements (esquisse)

PROJET	Bibliothèque Decimo — RDC sous logements, Abidjan
PHASE	ESQ V5 — aménagement sur existant V4
PLANCHE	A03 — Coupe AA sur l'arbre à livres
ÉCHELLE	1/50 · format A3
MAQUETTE	v5/DECIMO_ESQ_V5.ifc (IFC4) · sha256 34152b66f6…
DATE	Octobre 2026 · indice A

Esquisse : cotes et surfaces indicatives, existant V4 à relever sur site.