

Élévation intérieure Sud — façade vue de l'intérieur (coupe y = 0,80)

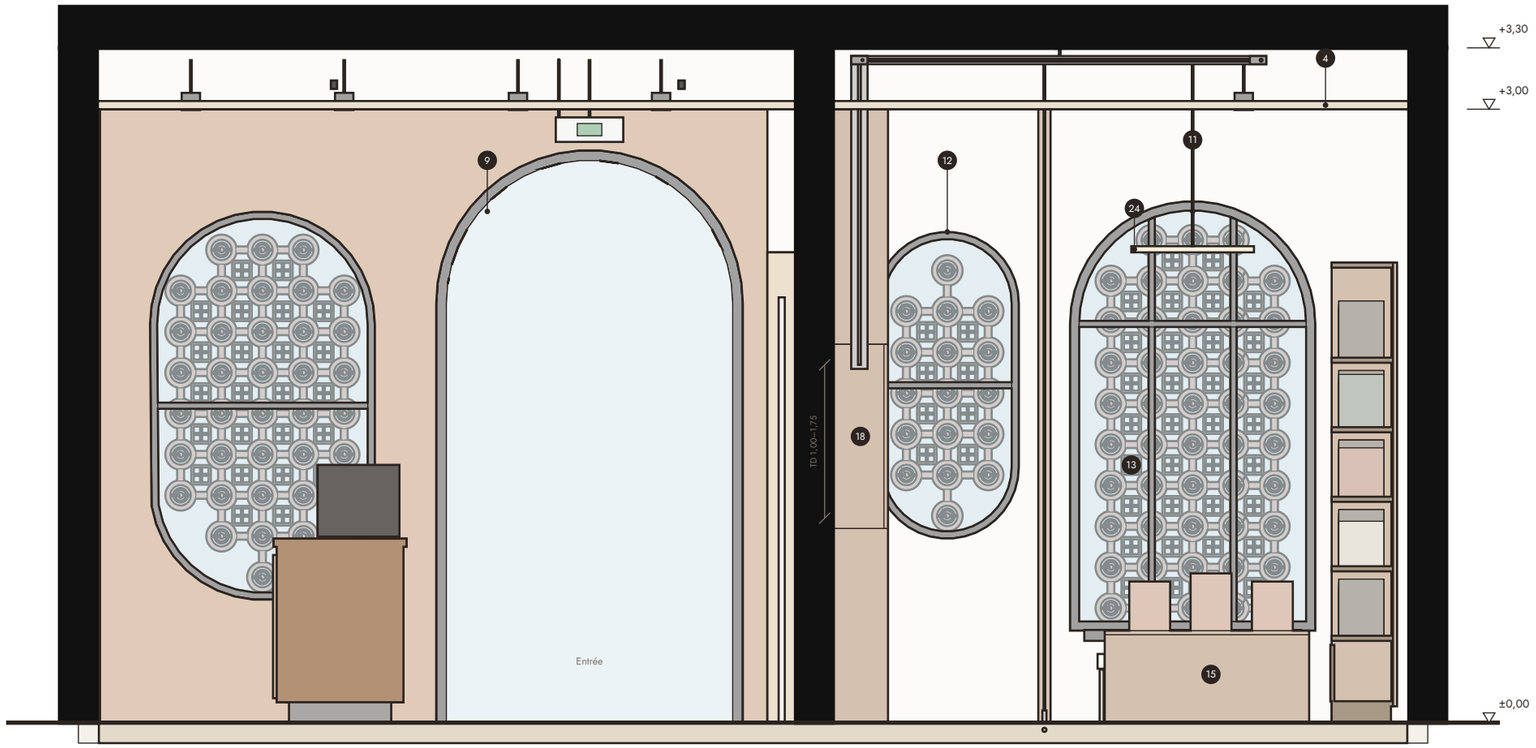

Élévation intérieure Ouest — coin lecture, réunion, rangement, WC (coupe x = 2,85)

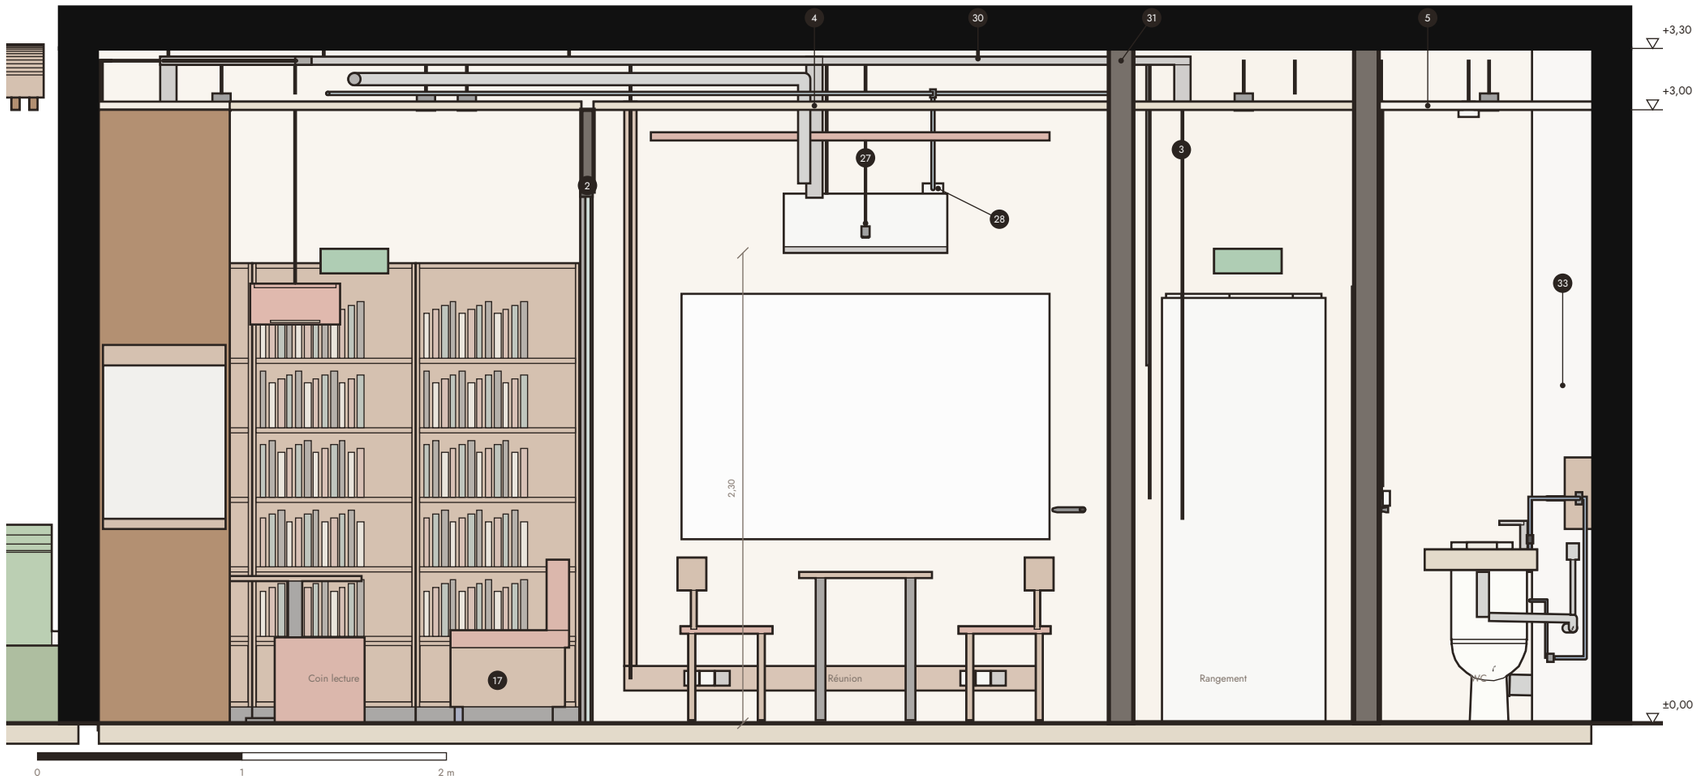

K&Démi

Bibliothèque Decimo

Élévations intérieures Sud et Ouest

Façade intérieure, coin lecture, réunion, locaux de service · Échelle 1/30 (A3)

TECHNIQUE (HYPOTHÈSES ESQ AHOUA)

Tableau divisionnaire ~0,60 × 0,25 encastré dans un habillage iroko près de l'entrée (coin lecture), 1,00 m libre devant, loin de tout point d'eau (rep. 18).
Placard technique 0,60 × 0,40 net, porte pleine : arrivée électrique de l'immeuble, baie informatique, coffret des liaisons clim (rep. 3).
Split 2 en partie haute du mur mitoyen de la réunion, hors aplomb de la table.
Coffrages acoustiques 0,30 × 0,30 des descentes EU/EV (rep. 33) : « À relever sur site ». Pas de TGBT ni de groupe électrogène.
Réseaux : voir A09 (électricité), A10 (plomberie), A11 (détails).

REPÈRES DE L'AMÉNAGEMENT V5

- 2 Cloison légère / retombée BA13 (ajout V5)
- 3 Placard technique 0,60 x 0,40 net
- 4 Faux-plafond acoustique (+3,00, plénum 0,26)
- 5 Faux-plafond hydrofuge WC (+3,00)
- 9 Enduit terre (argile locale) 15 mm
- 11 Vitrine en arche, châssis acier noir
- 12 Châssis fixes acier noir (baies B, C)
- 13 Claustras terre cuite : inserts Adinkrahene et Eban
- 15 Podium de vitrine iroko (h 0,45 = allège baie A)
- 17 Pouf de lecture indigo
- 18 Tableau divisionnaire encastré dans habillage iroko
- 24 Réglette LED de vitrine
- 27 Split mural 9 000 BTU/h (2,6 kW)
- 28 Mini-pompe de relevage des condensats
- 30 Chemin de câbles 80 x 40 en plénum
- 31 Réservation Ø 0,10 (hors structure)
- 33 Coffrage acoustique 0,30 x 0,30 descente EU/EV (à relever)

LÉGENDE

- Existant porteur coupé
- Cloison légère coupée
- Vitrage

PROJET	Bibliothèque Decimo — RDC sous logements, Abidjan
PHASE	ESQ V5 — aménagement sur existant V4
PLANCHE	A06 — Élévations intérieures Sud et Ouest
ÉCHELLE	1/30 · format A3
MAQUETTE	v5/DECIMO_ESQ_V5.ifc (IFC4) · sha256 34152b66f6…
DATE	Octobre 2026 · indice A

Esquisse : cotes et surfaces indicatives, existant V4 à relever sur site.