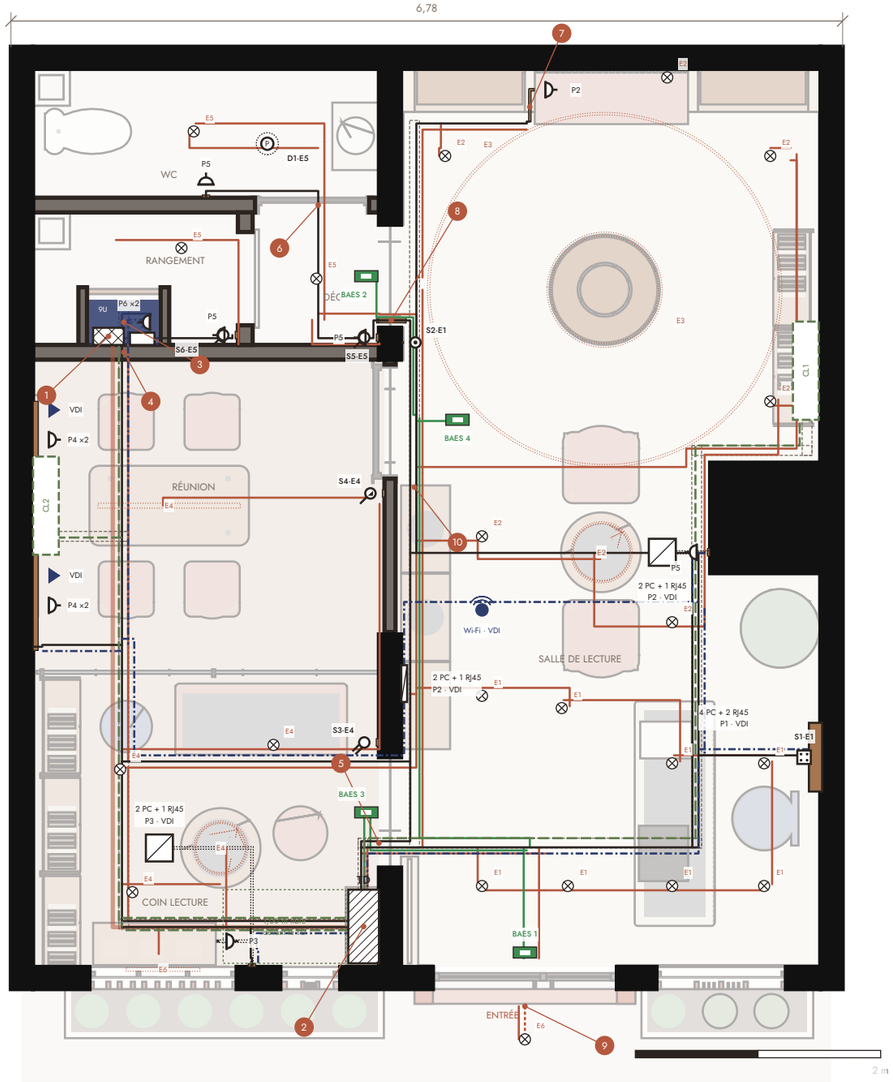


TABLEAU DES CIRCUITS — TD (HYPOTHÈSE ESQ, NF C 15-100)

CIRC.	DÉSIGNATION	PROTECTION	ID	CÂBLE	POINTS	L M
E1	Éclairage salle de lecture - accueil et entrée	Dj 10 A C	ID1	3G1,5	8 lum. + 2 cde	12,7
E2	Éclairage salle de lecture - fond, salon, niche	Dj 10 A C	ID1	3G1,5	7 lum.	22,2
E3	Éclairage scénographique arbre à livres (gradable)	Dj 10 A C	ID1	3G1,5	2 lum.	5,8
E4	Éclairage coin lecture et salle de réunion	Dj 10 A C	ID1	3G1,5	5 lum. + 2 cde	10,2
E5	Éclairage locaux de service (rangement, dégagement, WC)	Dj 10 A C	ID1	3G1,5	3 lum. + 3 cde	26,0
E6	Vitrine et marquise (horloge + interrupteur crépuscula…	Dj 10 A C	ID1	3G1,5	2 lum.	8,0
E7	BAES (alimentation non commandée, télécommande de repo…	Dj 2 A	ID1	3G1,5	4 lum.	11,0
P1	Prises banque d'accueil	Dj 20 A	ID2	3G2,5	4 PC	5,2
P2	Prises postes de lecture - salle	Dj 20 A	ID2	3G2,5	5 PC	12,7
P3	Prises coin lecture et vitrine	Dj 20 A	ID2	3G2,5	3 PC	1,3
P4	Prises salle de réunion	Dj 20 A	ID2	3G2,5	4 PC	5,0
P5	Prises ménage et locaux de service (WC hors volumes)	Dj 20 A	ID3	3G2,5	4 PC	32,7
P6	Baie informatique (onduleur) - circuit spécialisé	Dj 16 A	ID2	3G2,5	2 PC	7,2
CL1	Split 1 salle de lecture (unité int. + mini-pompe) - s…	Dj 16 A D	ID3	3G2,5	2 app.	22,1
CL2	Split 2 salle de réunion (unité int. + mini-pompe) - s…	Dj 16 A D	ID3	3G2,5	2 app.	8,5
VDI	Courants faibles : RJ45 cat. 6A depuis la baie 9U (1 c…	-	-	cat. 6A	8 RJ45 + 2 app.	20,7

ID1 interrupteur différentiel 40 A 30 mA type AC (éclairage, BAES) · ID2 40 A 30 mA type A (prises, baie VDI) · ID3 40 A 30 mA type A (ménage, splits). Dj courbe C, splits courbe D.
L m : longueur en plénum mesurée sur la directrice IFC (hors descentes). Réserve TD 20 % mini.
Arrivée : U1000 R2V 3G10 depuis le disjoncteur de branchement CIE (placard technique).

HAUTEURS DE POSE (AXE, DEPUIS LE SOL FINI) ET QUANTITÉS TIRÉES DE L'IFC

OUVRAGE	QTÉ	HAUTEUR D'AXE (M)
PC 16 A 2P+T	18	0,22 / 0,30 / 0,31 / 0,60 / 1,00 …
Commandes (interrupteurs, poussoirs, clavier)	6	1,10
RJ45 cat. 6A	5	0,22 / 0,31 / 1,06
BAES évacuation SATI 45 lm 1 h	4	2,26 / 2,84 / 2,90
PC 16 A 2P+T en boîte de sol	4	0,00
Unité intérieure split 9 000 BTU/h	2	
Nourrices de goulotte	2	0,31 / 1,06
Boîtes de sol	2	0,00
RJ45 cat. 6A en boîte de sol	2	0,00
Détecteur de présence encastré	1	3,00
Point d'accès Wi-Fi 6 PoE	1	3,00
RJ45 cat. 6A en plénum	1	3,04
Luminaires LED 2700 K de la V5 (conservés, raccordés)	27	plafond / suspension
Goulottes iroko et moulures (longueur cumulée)	27,4 m	12 tronçons
Câbles (directrices IFC, descentes comprises)	215 m	hors réserve de raccordement

K&Démi

Bibliothèque Decimo

Électricité — courants forts et faibles

Plan CFO / CFA · Échelle 1/50 (A3) · Coupe à +1,00, réseaux du plénum projetés

SYMBOLES

- Prise de courant 16 A 2P+T (circuit P, ×n)
- Prise RJ45 cat. 6A (VDI)
- Nourrice / goulotte iroko en applique
- Boîte de sol (dans la chape du sol fini)
- Interrupteur (S5, S6) — double : S3
- Bouton-poussoir sur télérupteur (S2, va-et-vient)
- Interrupteur variateur (S4)
- Clavier de commande éclairage (S1, accueil)
- Détecteur de présence (WC)
- BAES évacuation / balisage SATI 1 h (E7)
- Luminaire LED 2700 K V5 conservé (circuit)
- Point d'accès Wi-Fi PoE plafond
- Éclairage E1-E6 : câbles en plénum
- BAES E7 : câbles en plénum
- Prises P1-P6 : câbles en plénum
- Splits CL1-CL2 : câbles en plénum
- Courants faibles VDI : câbles en plénum
- Chemin de câbles 80 × 40 (plénum)
- Conduit sous le sol fini (boîtes de sol)

POINTS SINGULIERS

1. Arrivée immeuble : disjoncteur de branchement (placard), 3G10 vers le TD
2. TD encastré (habillage iroko), nappe des départs vers le plénum
3. Baie VDI 9U murale (onduleur, P6), départs RJ45 cat. 6A en étoile
4. R5 Ø 0,10 : cloison placo 4350621, placard -> réunion (plénum)
5. Passage du galandage au-dessus de la retombée BA13 (plénum)
6. R7 Ø 0,04 : cloison placo 4350620, dégagement -> WC
7. R6 Ø 0,04 : entrée du conduit dans le doublage V4 (niche)
8. Baie libre V4 : moulure sous linteau, goulotte sur le lambris
9. Fourreau existant de l'enseigne V4 (traversée de façade sans percement)
10. Chemin de câbles C3 80 × 40 en plénum (chevilles 40 mm)

PRINCIPES (HYPOTHÈSES ESQ AHOUA)

Réseau de l'immeuble seul : pas de TGBT, pas de groupe électrogène.
Aucun percement de poteau, voile ni dalle : descentes en goulottes iroko en applique, câbles en plénum (+3,24) sur chemins de câbles ; R5 à R8 dans des cloisons et doublages V4 non porteurs.
Boîtes de sol dans l'épaisseur du sol fini (chape 7 cm, à relever) : aucun carottage du dallage existant.
Éclairage : 27 luminaires 2700 K V5 conservés, 6 circuits E1-E6 ; fond de salle en va-et-vient (télérupteur, S1 / S2), WC sur détecteur.
BAES SATI 1 h : sortie au-dessus de la porte, balisage dégagement, coin lecture et circulation (télécommande de mise au repos au TD).
Prise du WC à 1,03 m du lave-mains (hors volumes 0 à 2).
Courants faibles : baie 9U, RJ45 cat. 6A en étoile, Wi-Fi PoE.

PROJET	Bibliothèque Decimo — RDC sous logements, Abidjan
PHASE	ESQ V5 — aménagement sur existant V4
PLANCHE	A09 — Électricité — courants forts et faibles
ÉCHELLE	1/50 · format A3
MAQUETTE	v5/DECIMO_ESQ_V5.ifc (IFC4) · sha256 34152b66f6…
DATE	Octobre 2026 · indice A

Esquisse : cotes et surfaces indicatives, existant V4 à relever sur site.